

COZINHA - PLANTA BAIXA

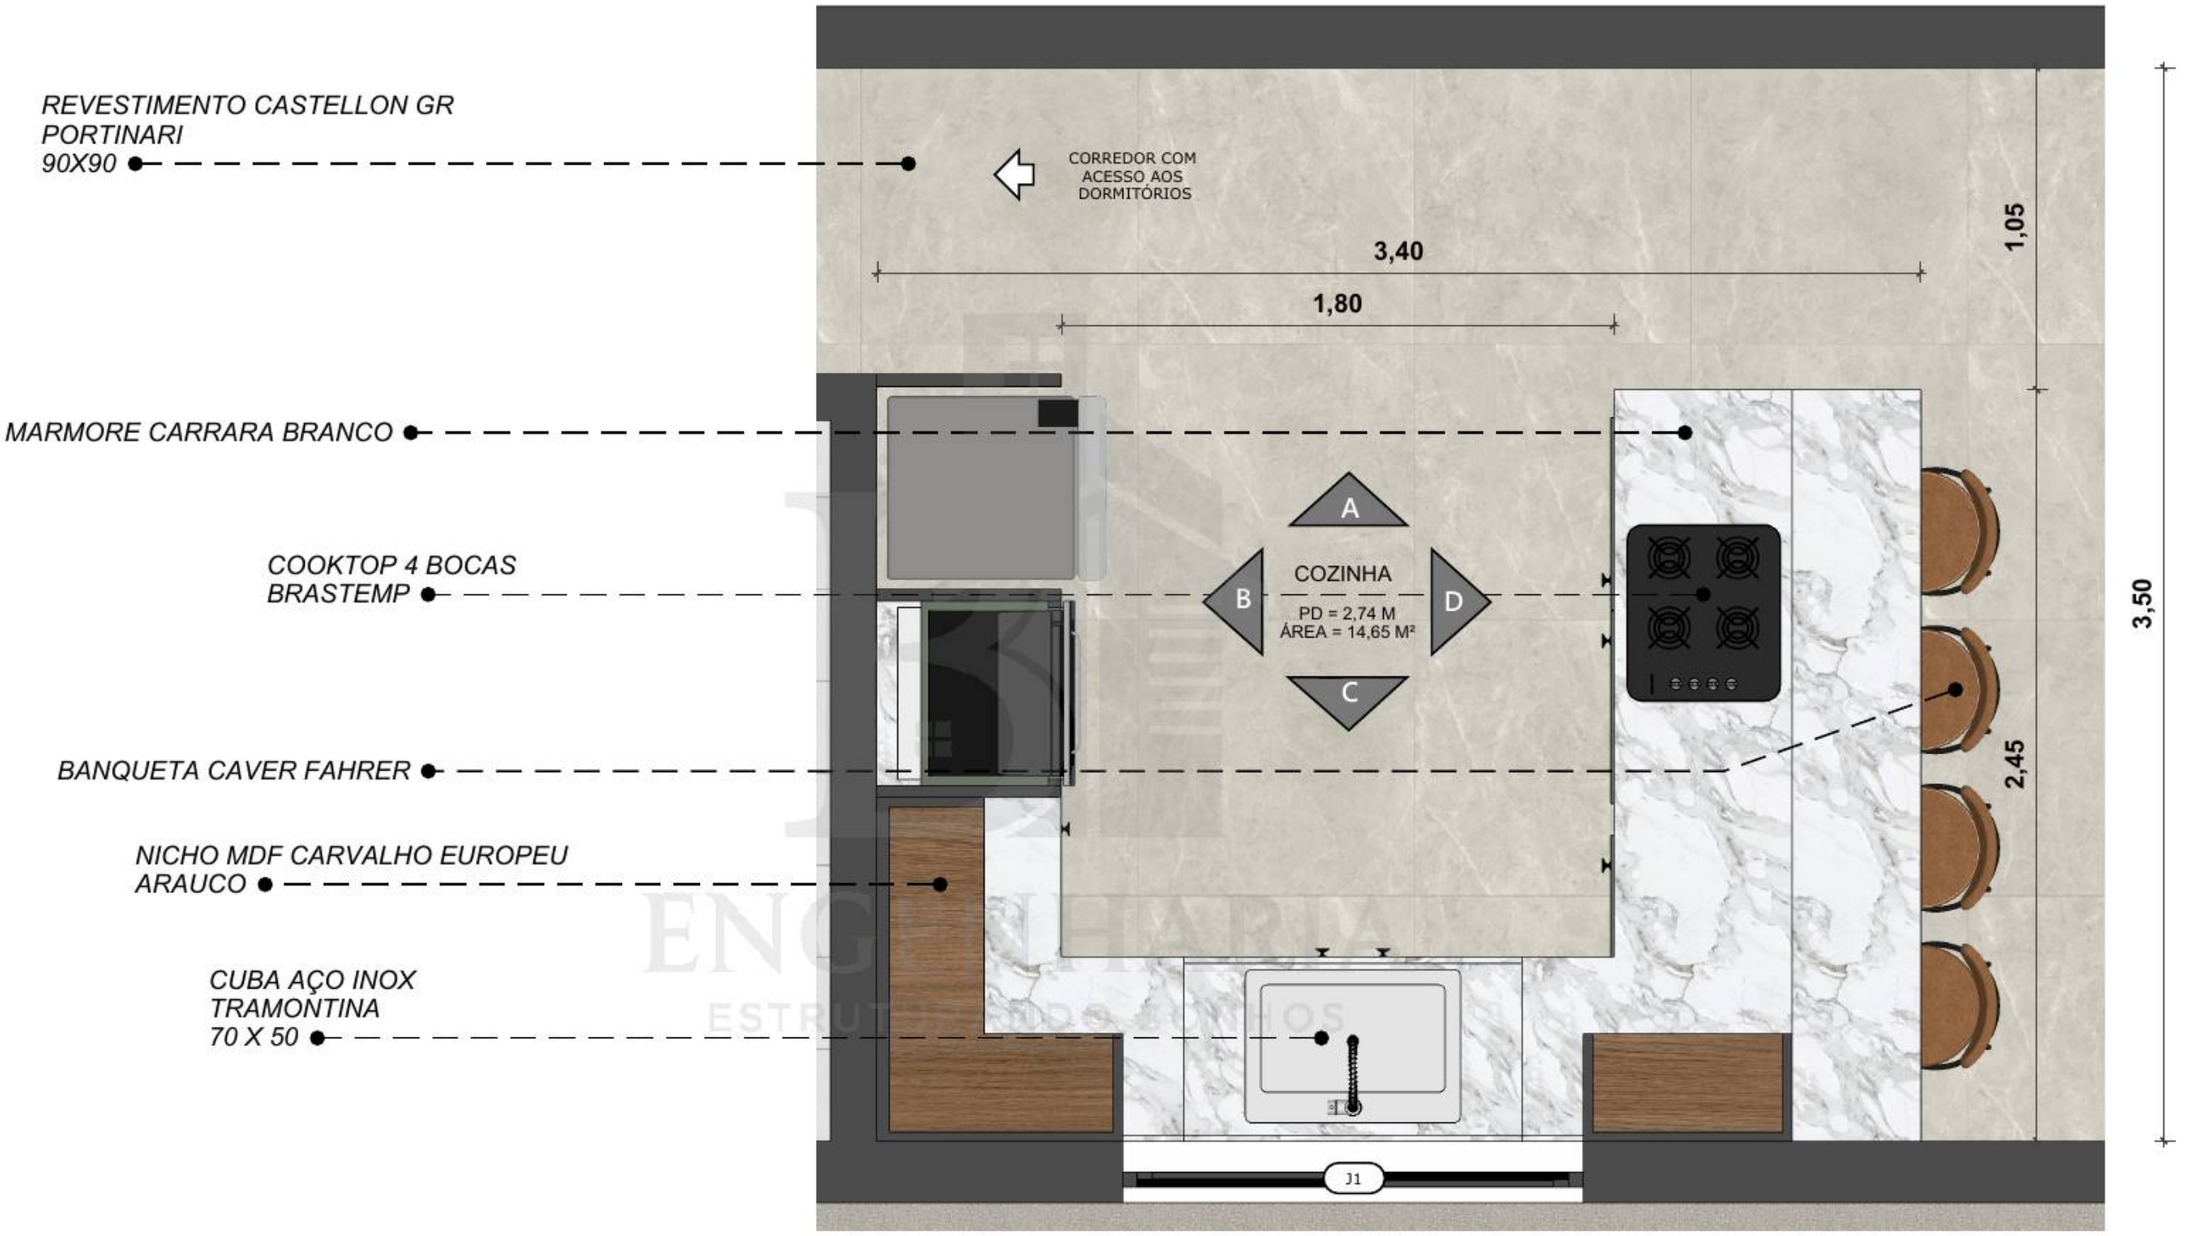

01 **PLANTA BAIXA - COZINHA**
Esc: 1/20

LOGO	**ARQUITETURA E INTERIORES** DETALHAMENTO - PROJETO BERNARDO	ESCRITÓRIO: ... ARQUITETO: ..... CAU:	PROPRIETÁRIA: - PROJETO: ARQUITETÔNICO E INTERIORES DATA: 01/04/2026	CONTEÚDO DETALHAMENTO DE INTERIORES MARCENARIA - RV_01	PRANCHA **01/60**

COZINHA - VISTA A

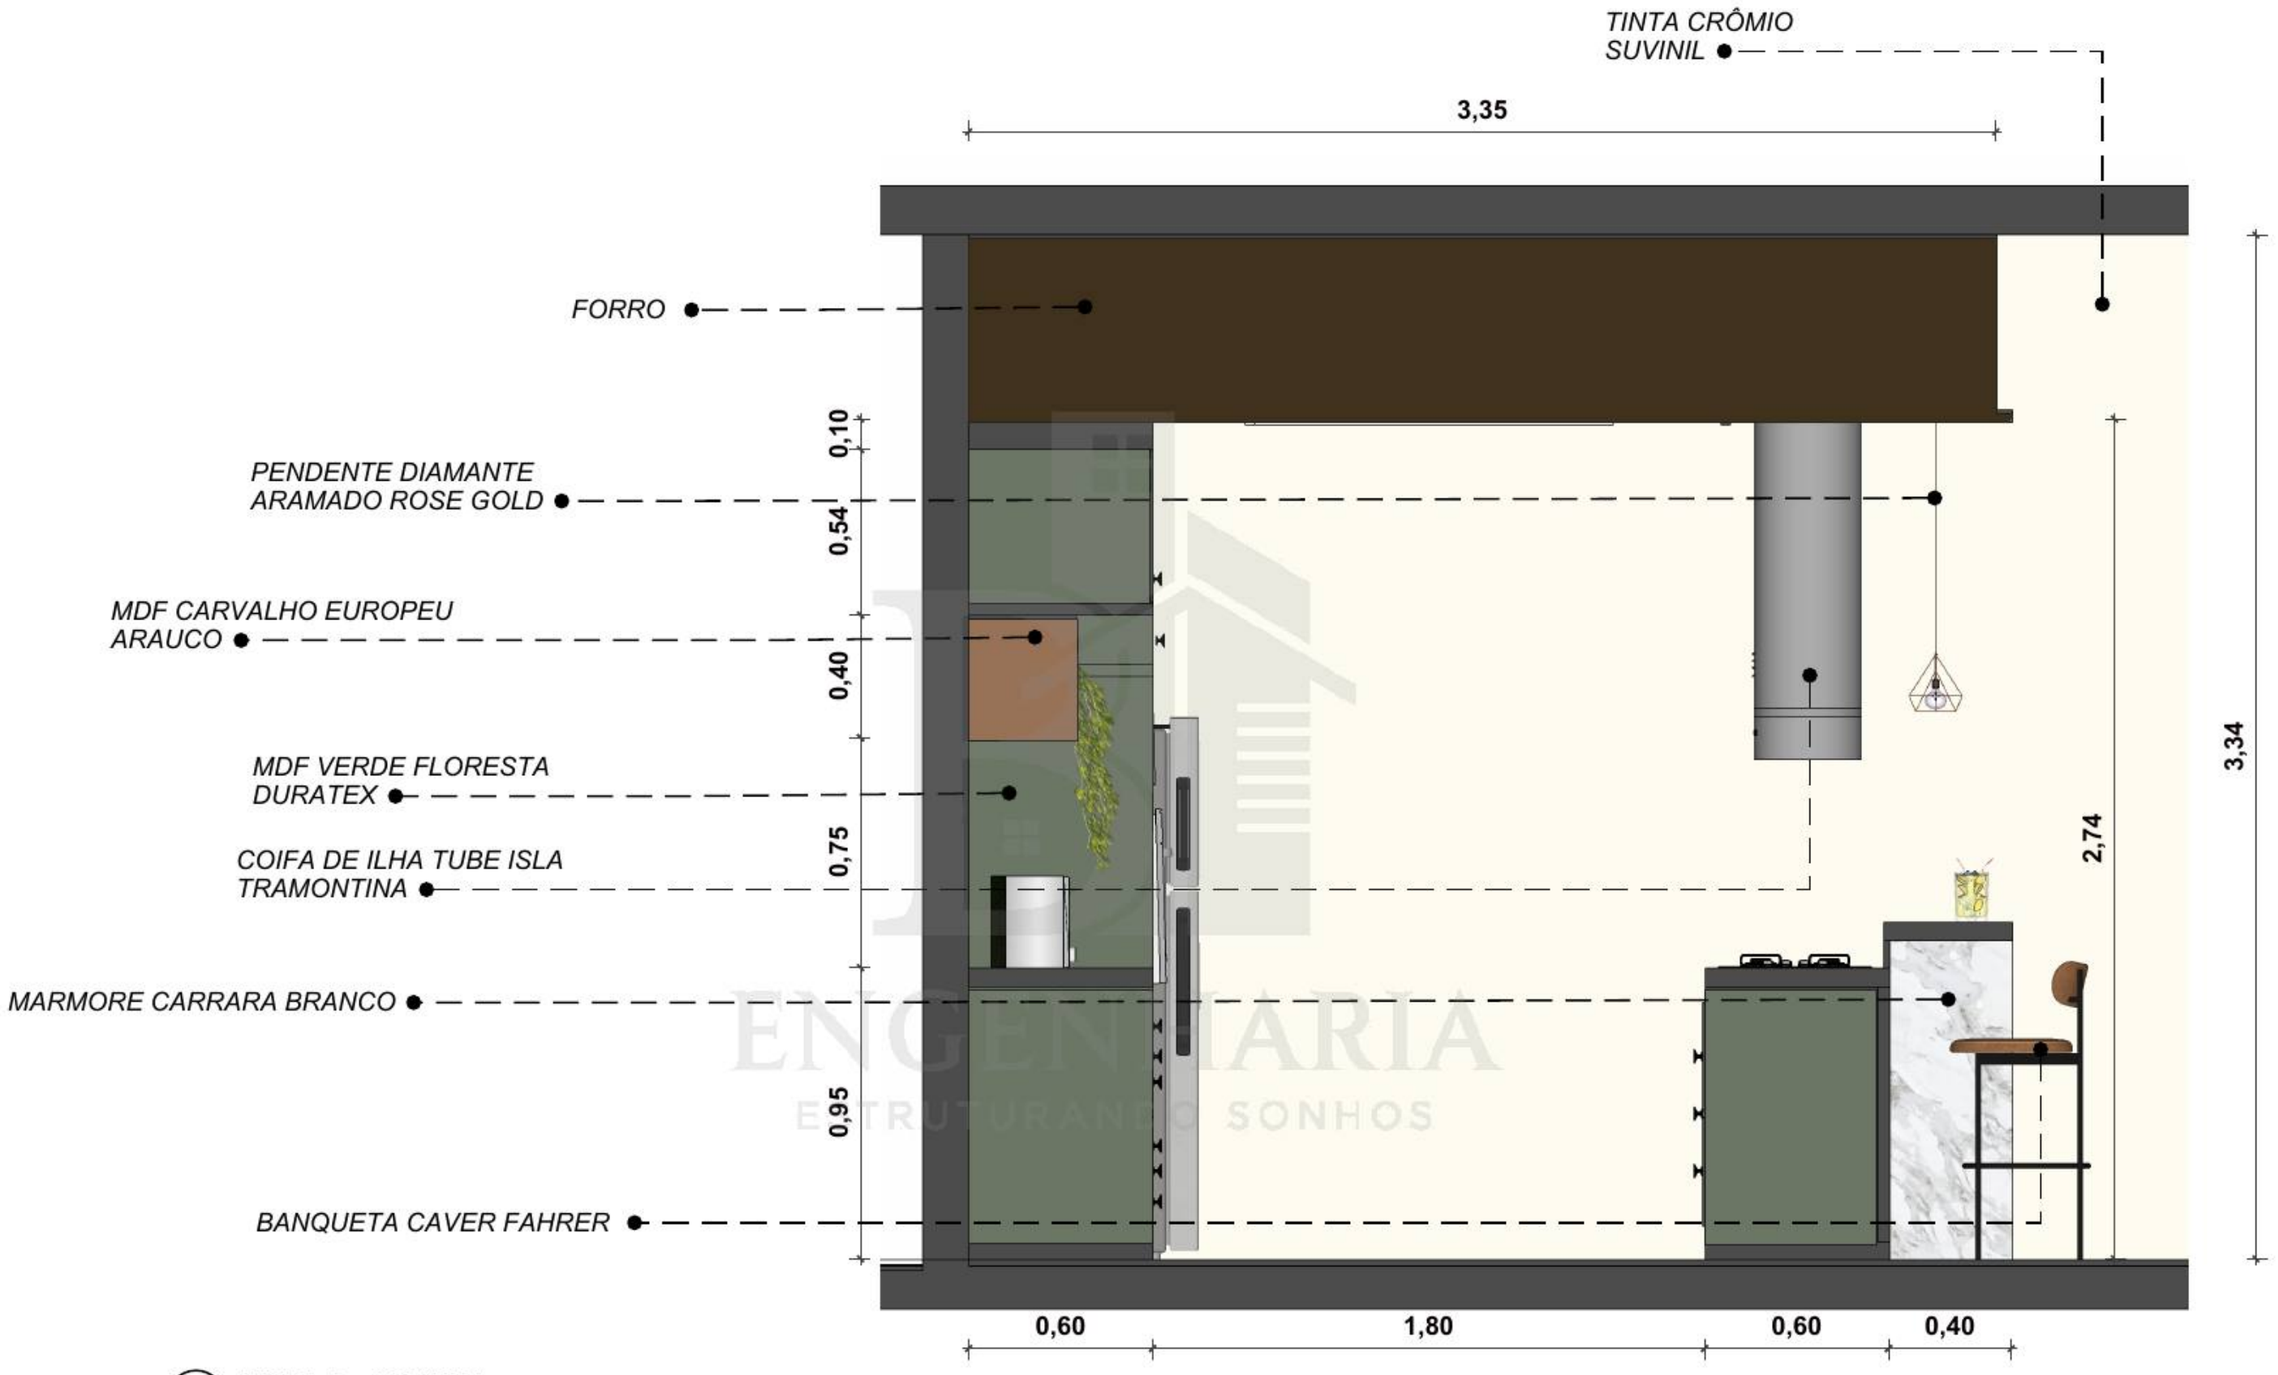

02 **VISTA A - COZINHA**
Esc: 1/20

ENGENHARIA
ESTRUTURANDO SONHOS

COZINHA - VISTA B

MC CAMINHO CURVÊ MIX NAT
30 X 30
PORTINARI

TINTA CRÔMIO
SUVINIL

FORRO
CARVALHO EUROPEU

MDF VERDE FLORESTA
DURATEX

NICHO
MDF CARVALHO EUROPEU
ARAUCO

REVESTIMENTO METRO WHITE
ELIANE
10 X 20

MICROONDAS 32L
INOX ESPELHADO
BRASTEMP

FORNO ELÉTRICO DE EMBUTIR 67L
BRASTEMP GOURMAND
COR INOX


GELADEIRA
COR INOX
ELETROLUX



03 **VISTA B - COZINHA**
Esc: 1/20

PRANCHA
03/60


COZINHA - VISTA C

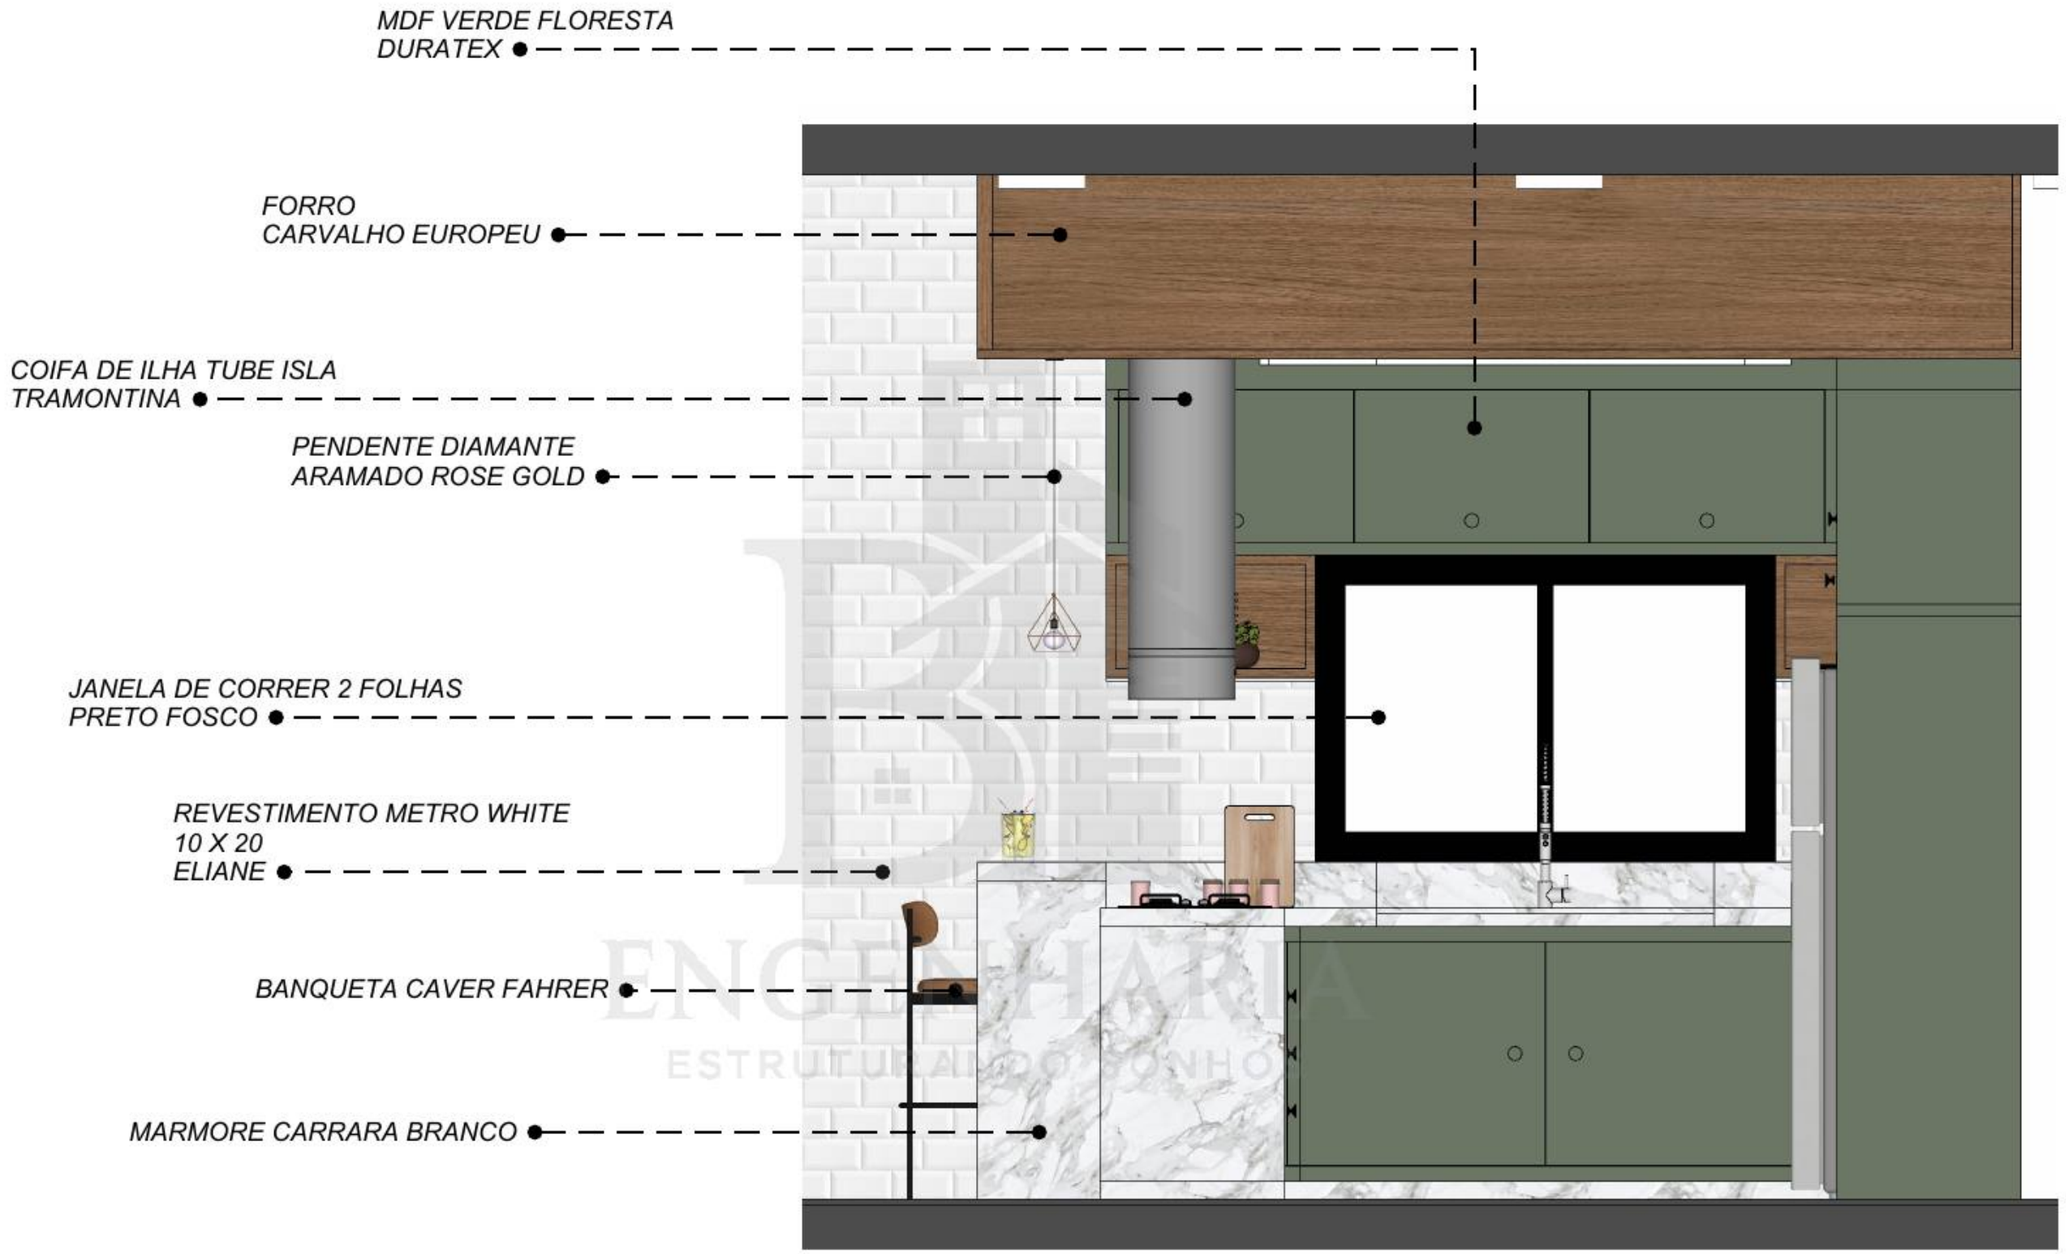

04 **VISTA C - COZINHA**
Esc: 1/20


ENGENHARIA
ESTRUTURANDO SONHOS

COZINHA - VISTA D

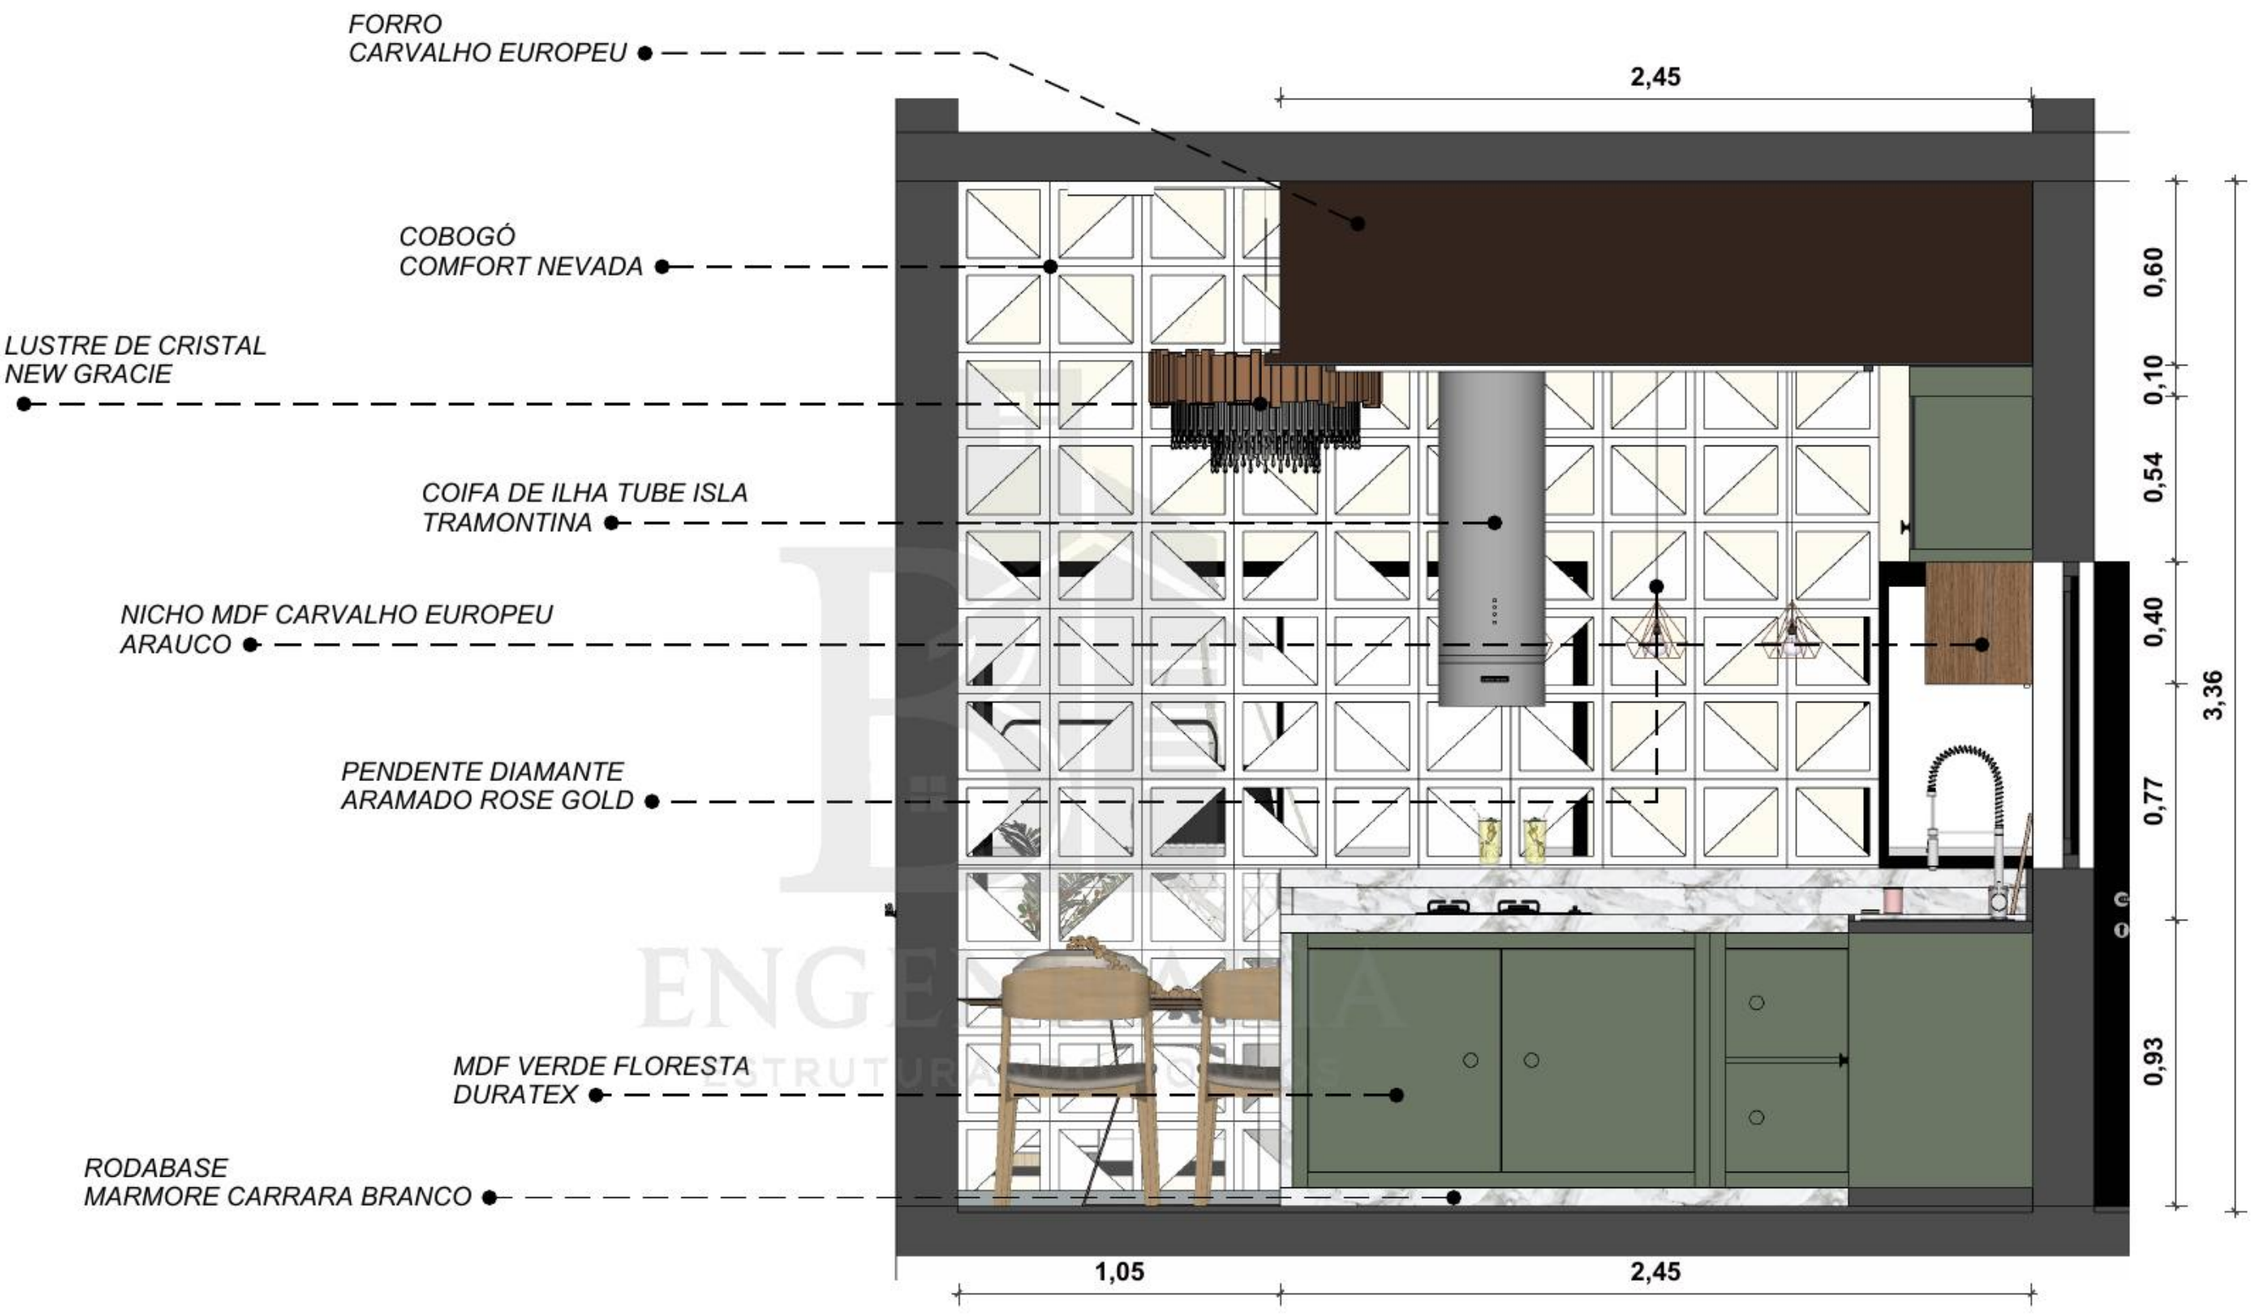


05 **VISTA D - COZINHA**
Esc: 1/20


COZINHA - DETALHAMENTO

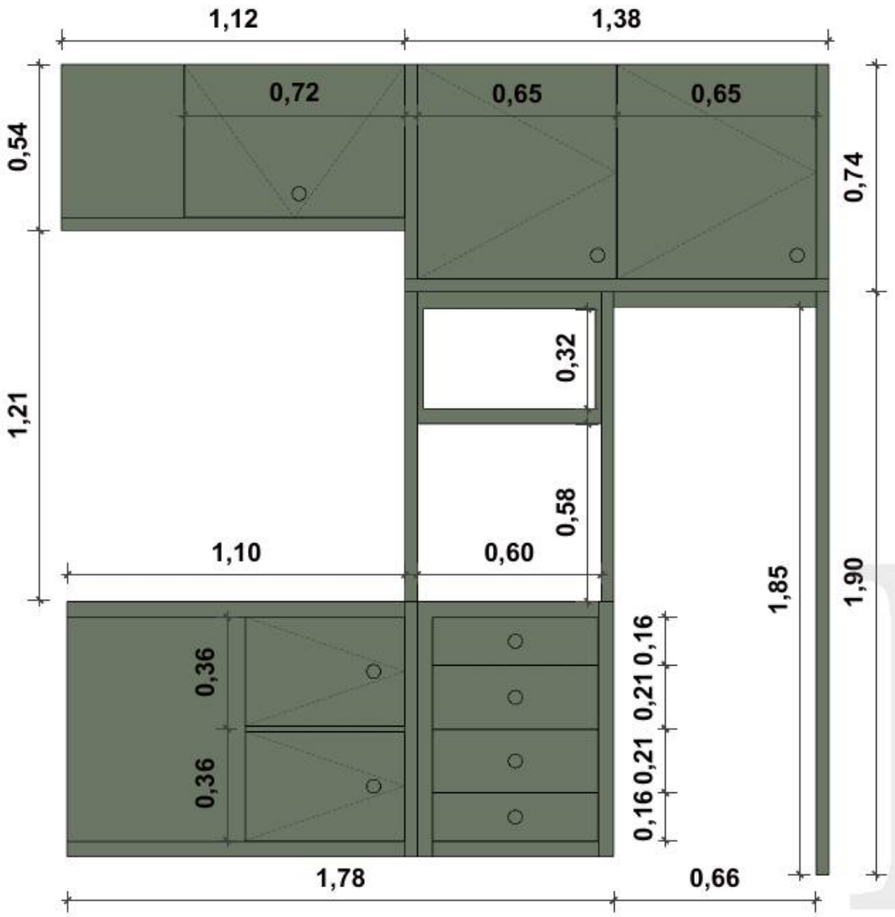


VISTA EM FRONTAL

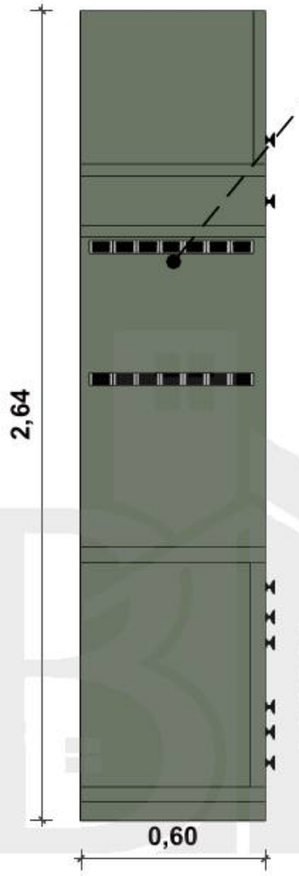


VISTA LATERAL

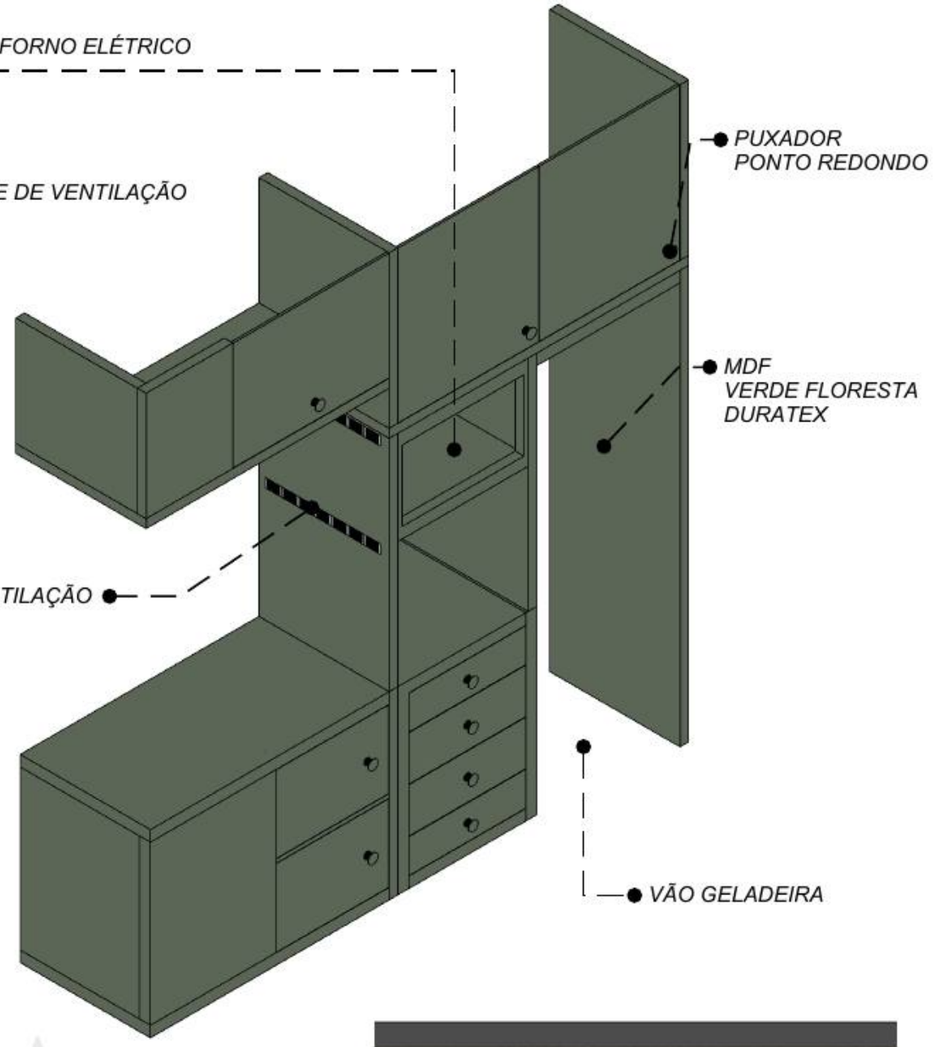

VISTA EM PERSPECTIVA

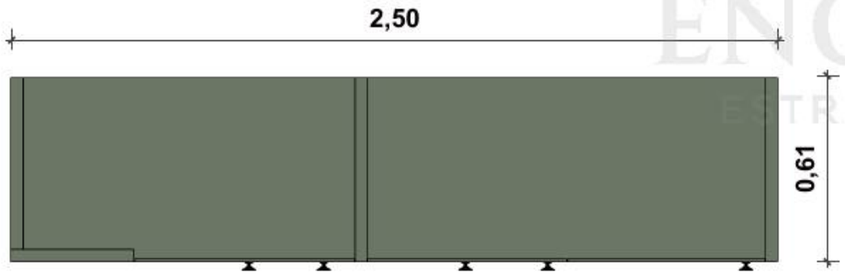


VISTA EM PLANTA

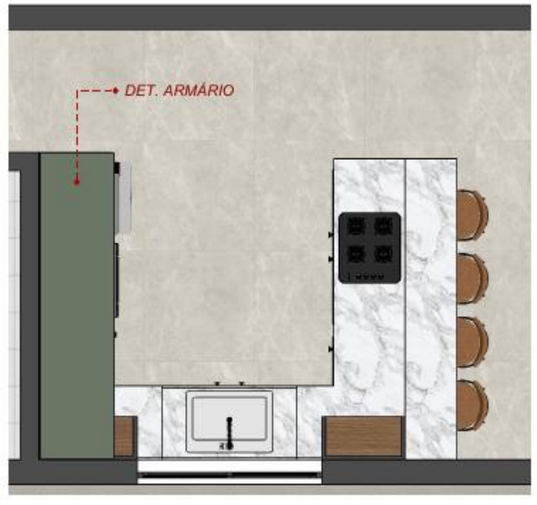


06 **DET. ARMÁRIO - COZINHA**
Esc: 1/20

ENGENHARIA
ESTRUTURANDO SONHOS


COZINHA - DETALHAMENTO

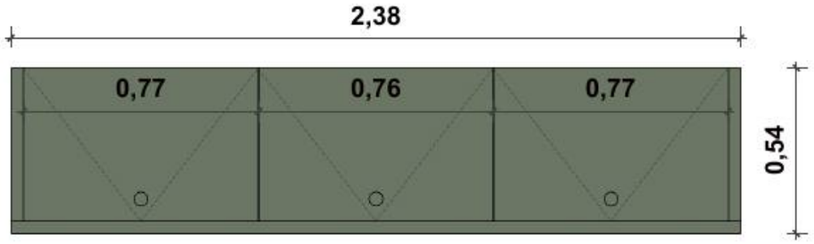


VISTA EM FRONTAL - ARMÁRIO AEREO

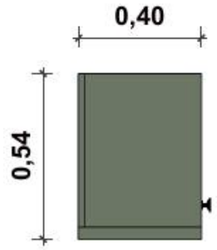


VISTA LATERAL - ARMÁRIO AÉREO

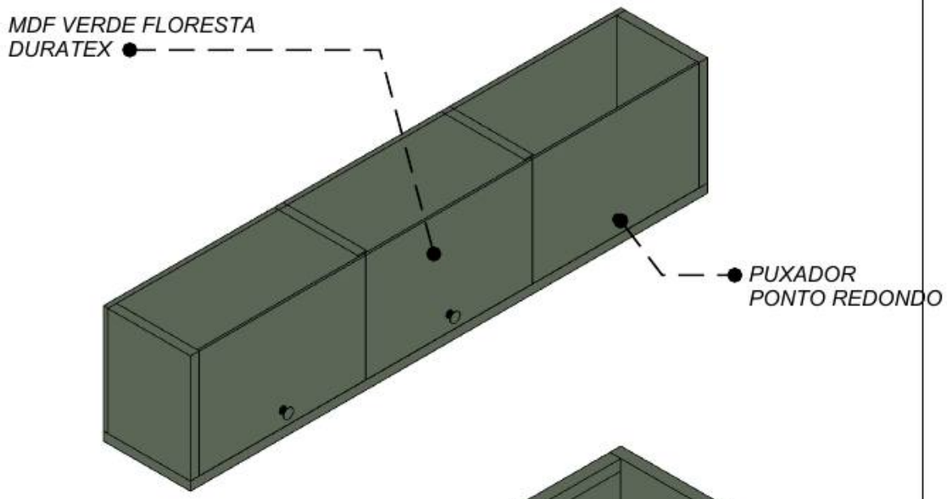


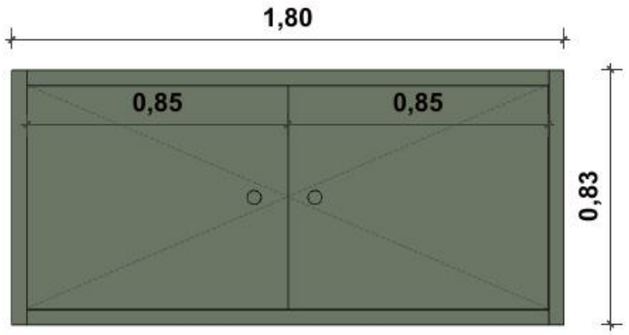


VISTA EM FRONTAL - ARMÁRIO

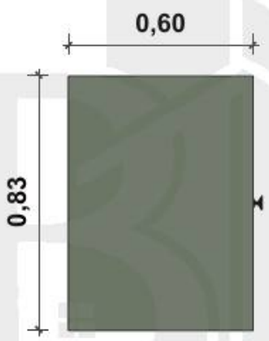


VISTA LATERAL - ARMÁRIO

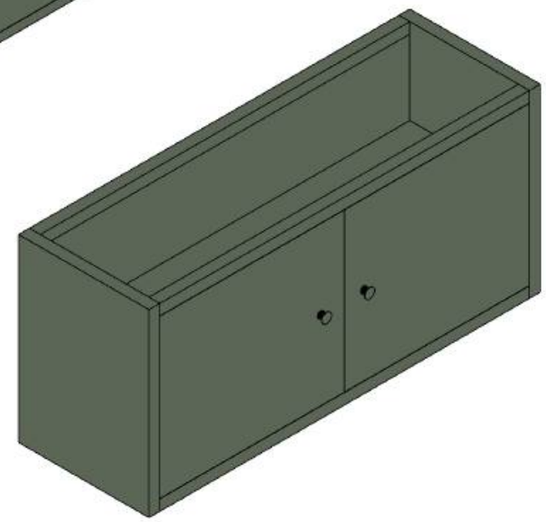


VISTA EM PERSPECTIVA

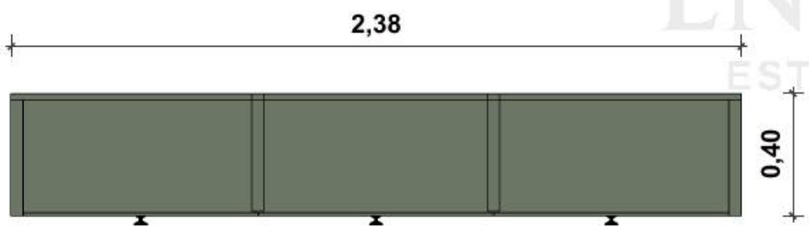

VISTA EM PLANTA - ARMÁRIO AÉREO

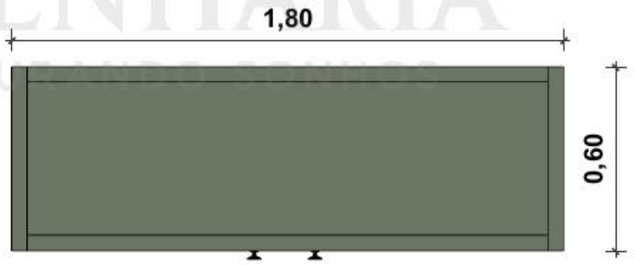


VISTA EM PLANTA - ARMÁRIO

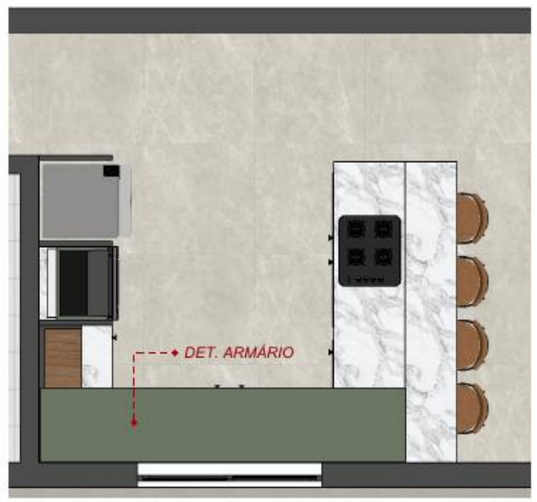


07 **DET. ARMÁRIO - COZINHA**
Esc: 1/20

ENGENHARIA
ESTRUTURANDO SONHOS


COZINHA - DETALHAMENTO

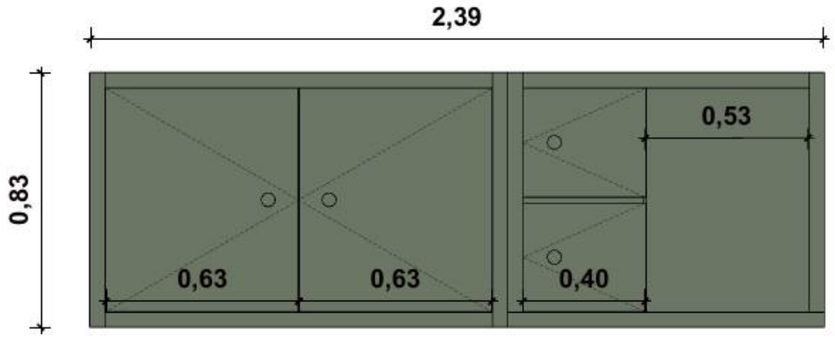


VISTA EM FRONTAL - ARMÁRIO

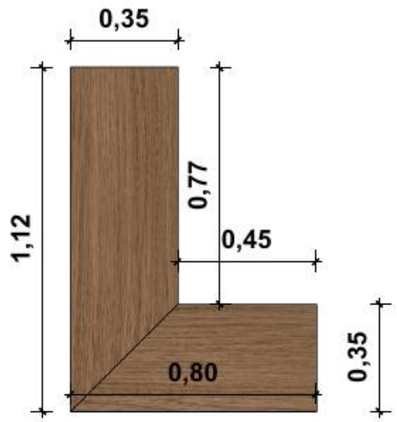


VISTA EM PLANTA - NICHO 1

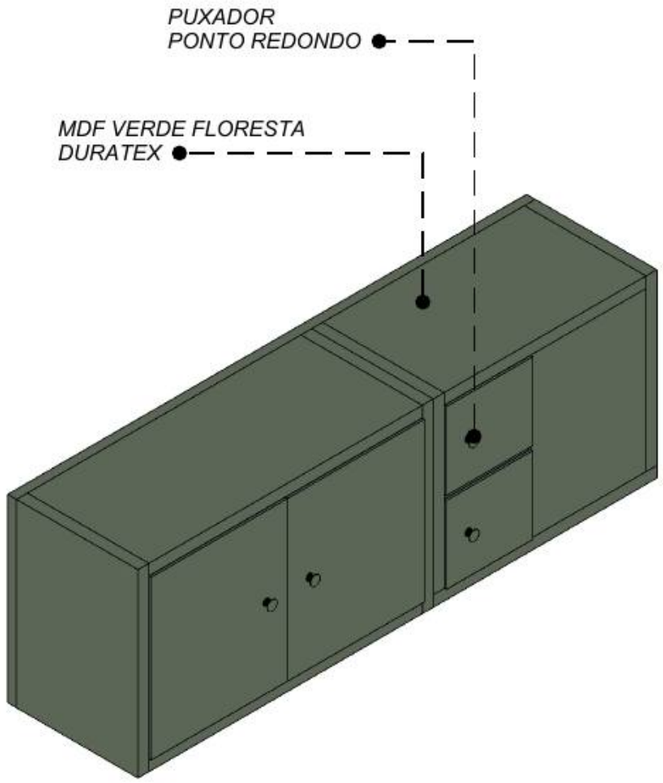


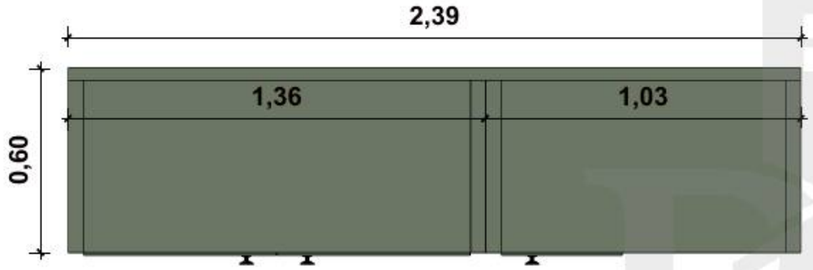


VISTA EM PLANTA - ARMÁRIO

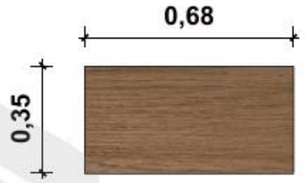

VISTA EM PLANTA - NICHO 2

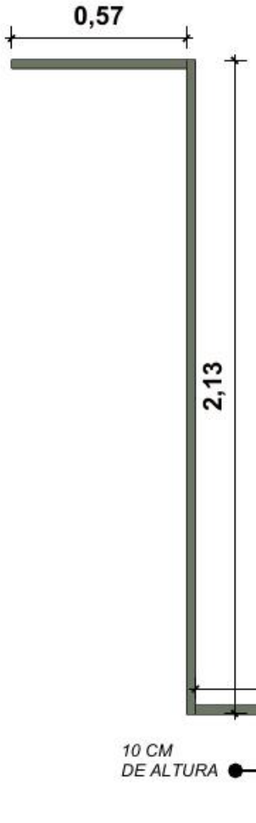


VISTA EM PLANTA - ARMÁRIO

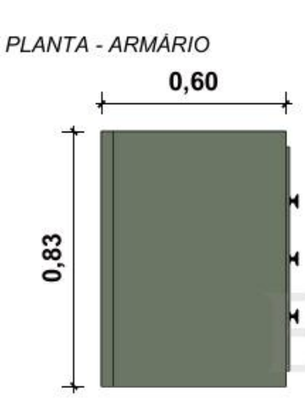


VISTA LATERAL - ARMÁRIO



VISTA EM PERSPECTINA - ARMÁRIO

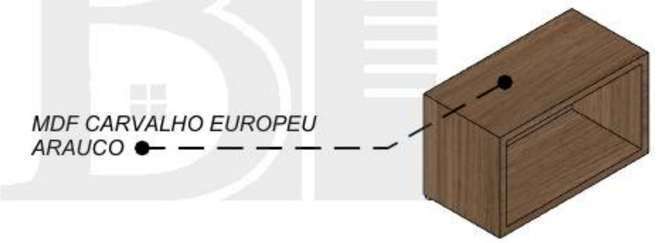


VISTA EM PERSP. - NICHO 1

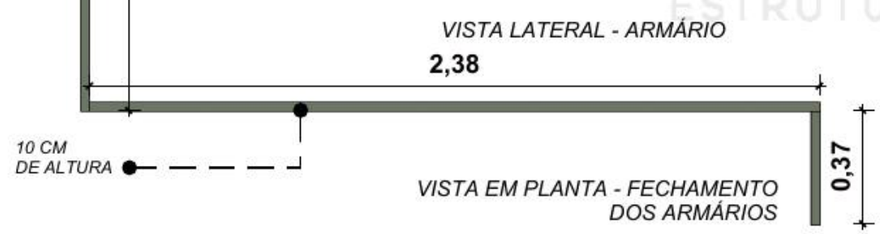

VISTA EM PLANTA - FECHAMENTO
DOS ARMÁRIOS



VISTA EM PERSP. - NICHO 2

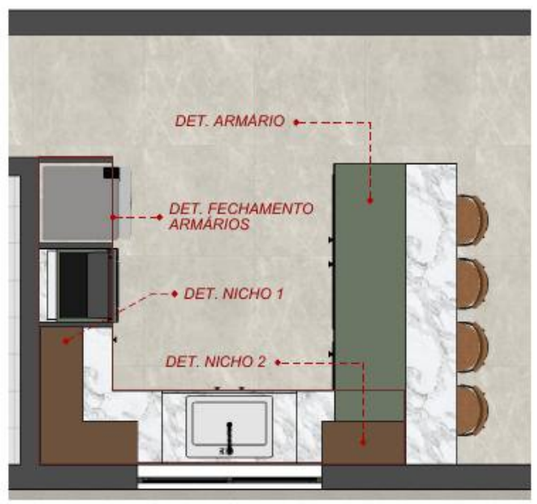

08 **DET. ARMÁRIO - COZINHA**
Esc: 1/20

ENGENHARIA
ESTRUTURANDO SONHOS

COZINHA - DETALHAMENTO




VISTA FRONTAL - FORRO




VISTA LATERAL - FORRO




VISTA EM PLANTA
FORRO

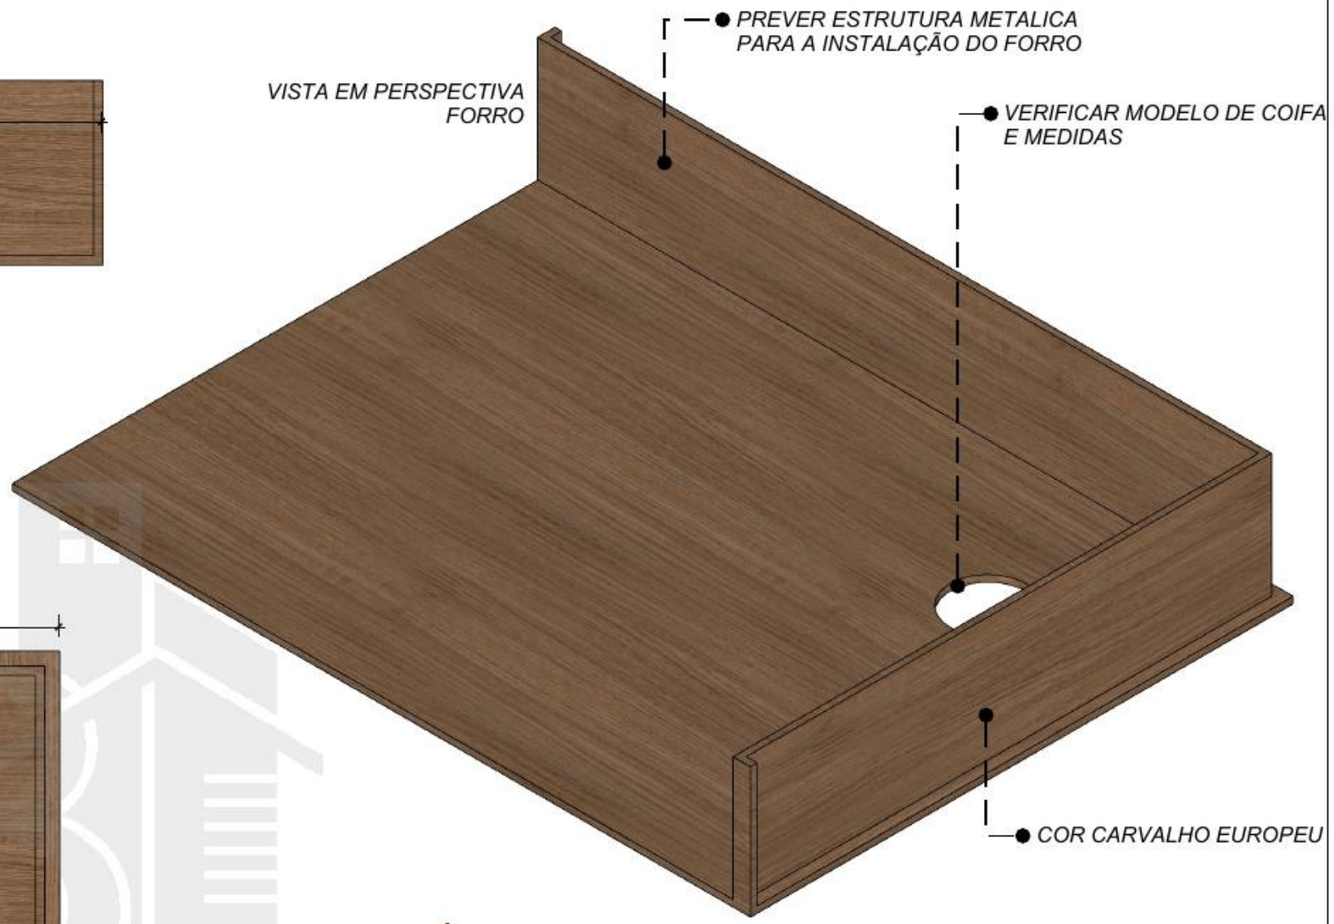

VISTA EM PERSPECTIVA
FORRO

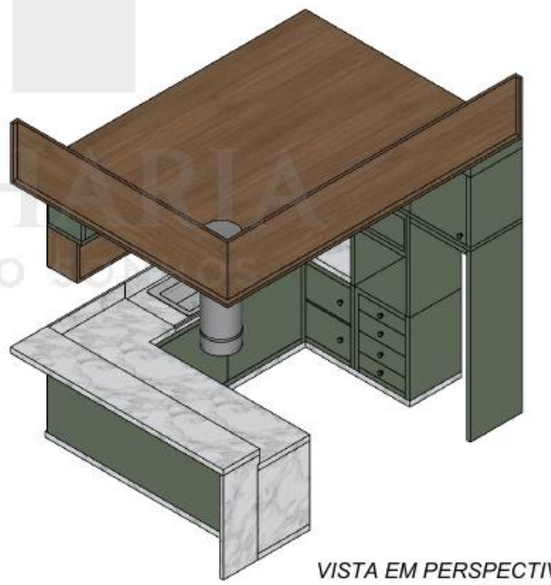

VISTA EM PERSPECTIVA
COZINHA

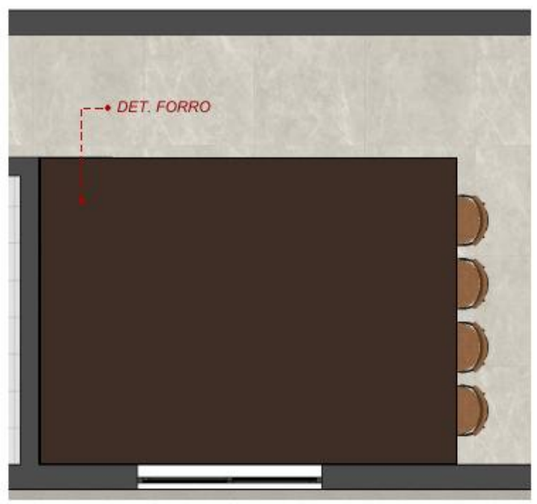


09 **DET. ARMÁRIO - COZINHA**
Esc: 1/20

ENGENHARIA
DESENVOLVENDO SOLUÇÕES

PRANCHA
09/60


SALA DE JANTAR - PLANTA BAIXA

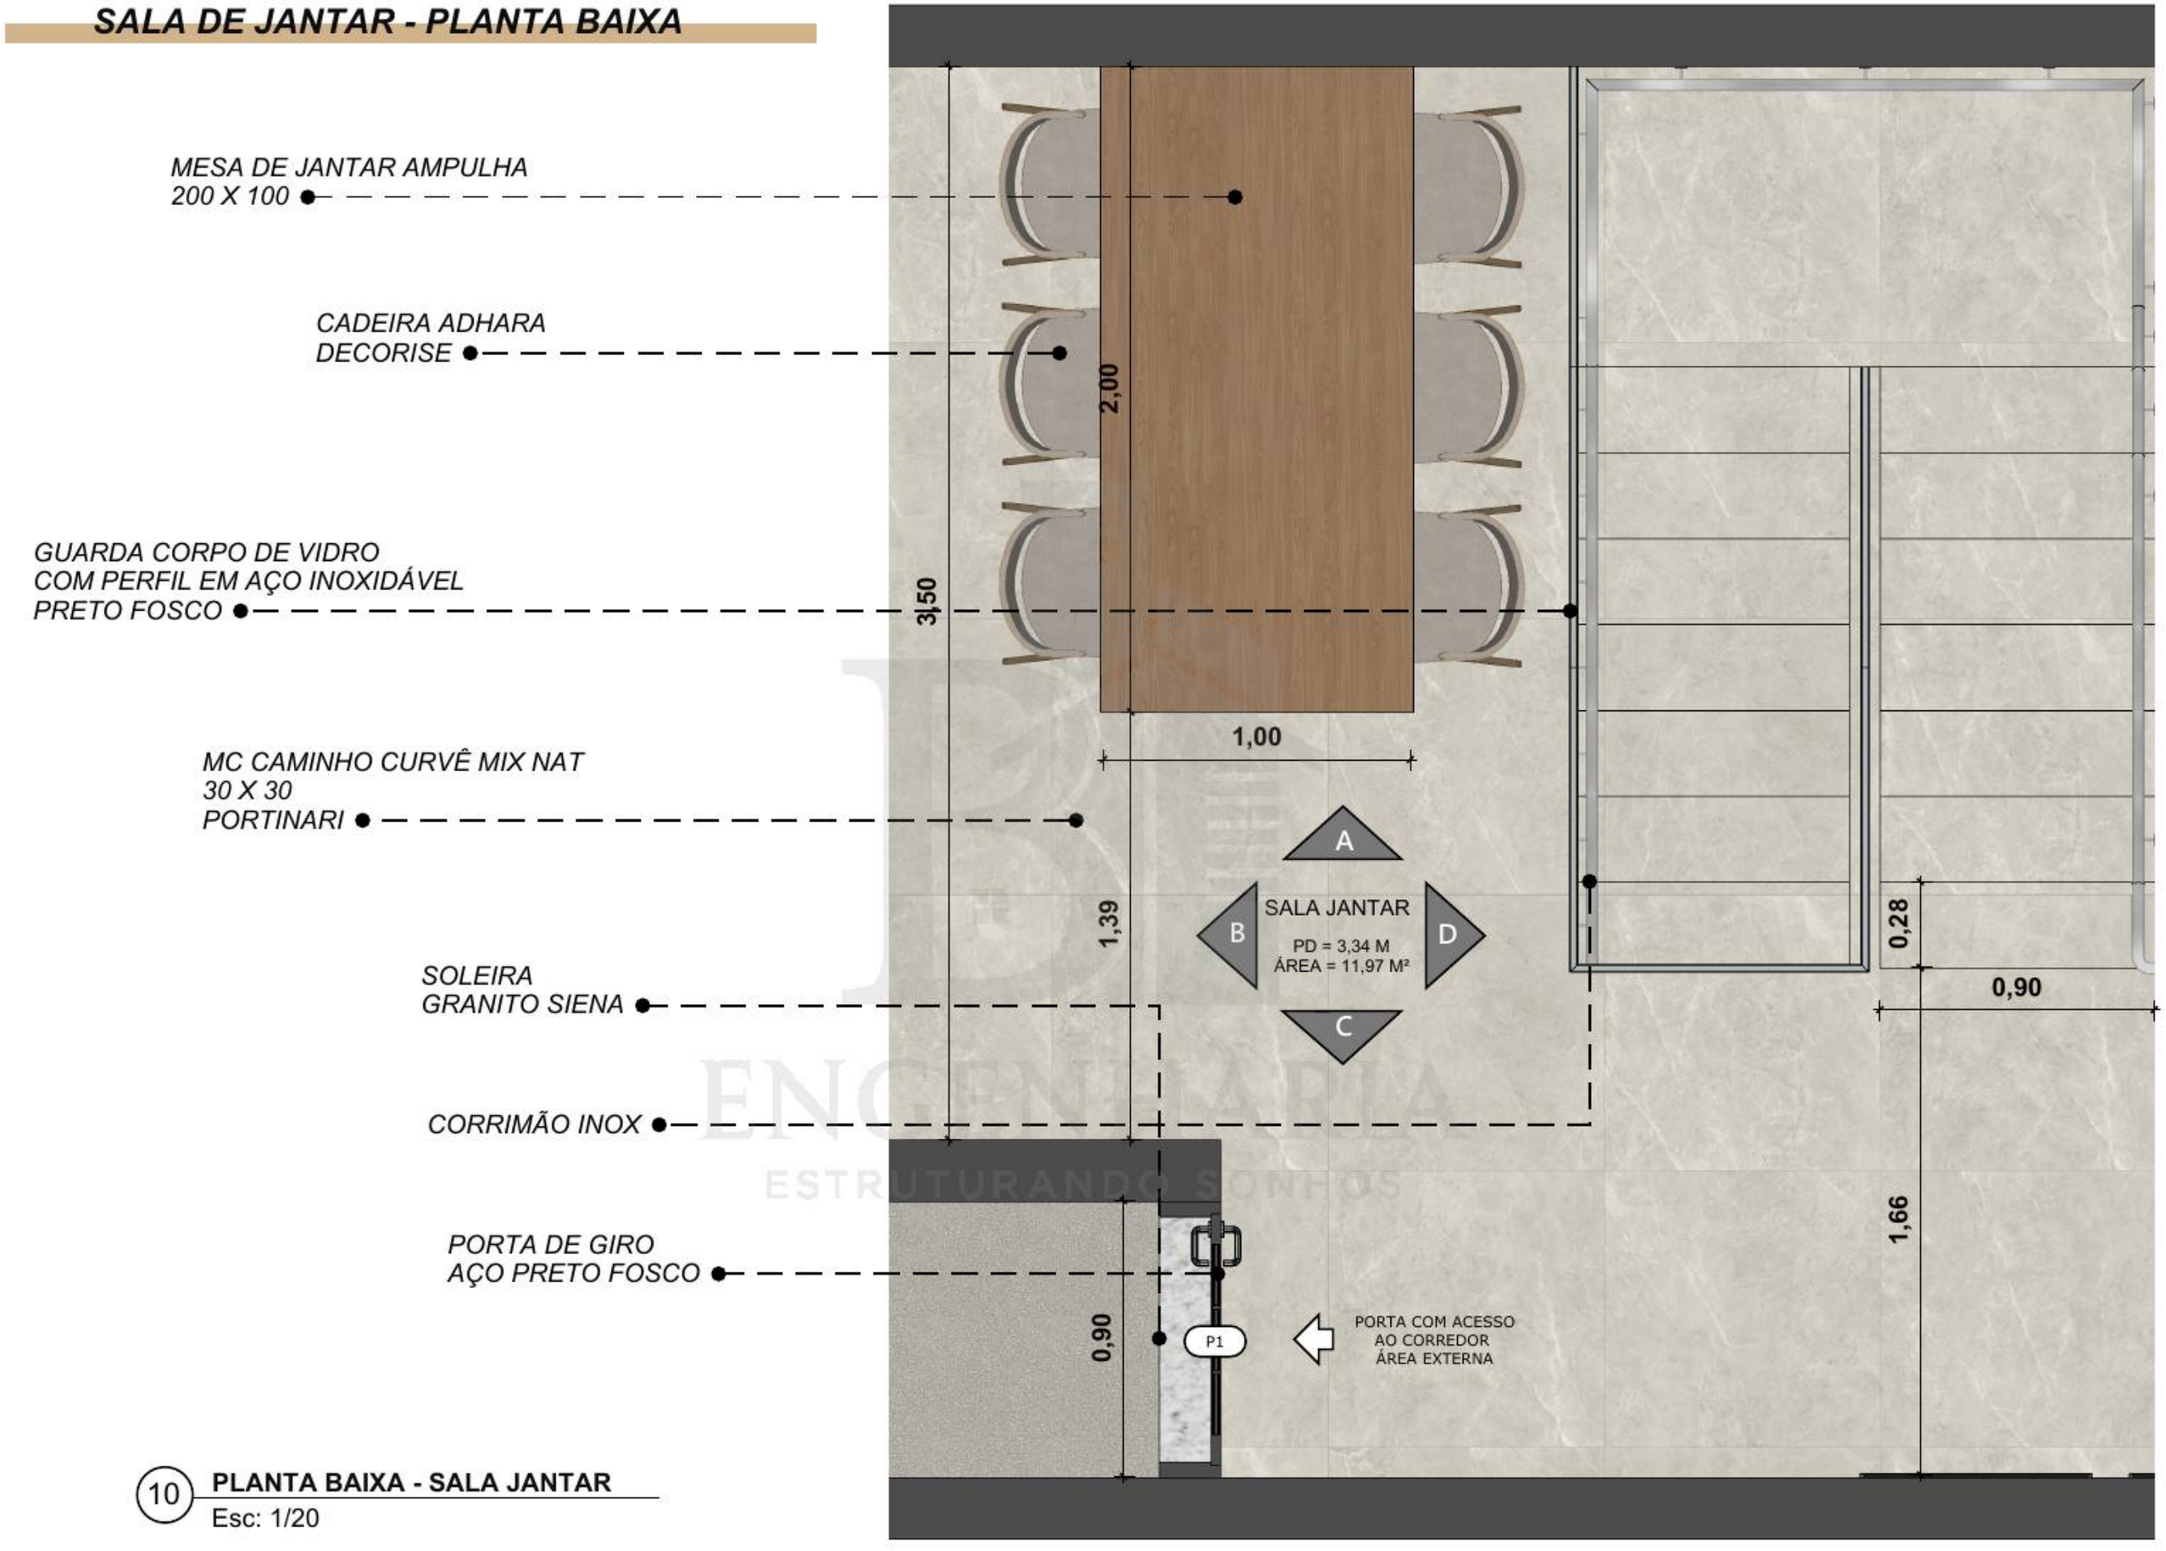

10 **PLANTA BAIXA - SALA JANTAR**
Esc: 1/20

ENGENHARIA
ESTRUTURANDO SONHOS


SALA DE JANTAR - VISTA A

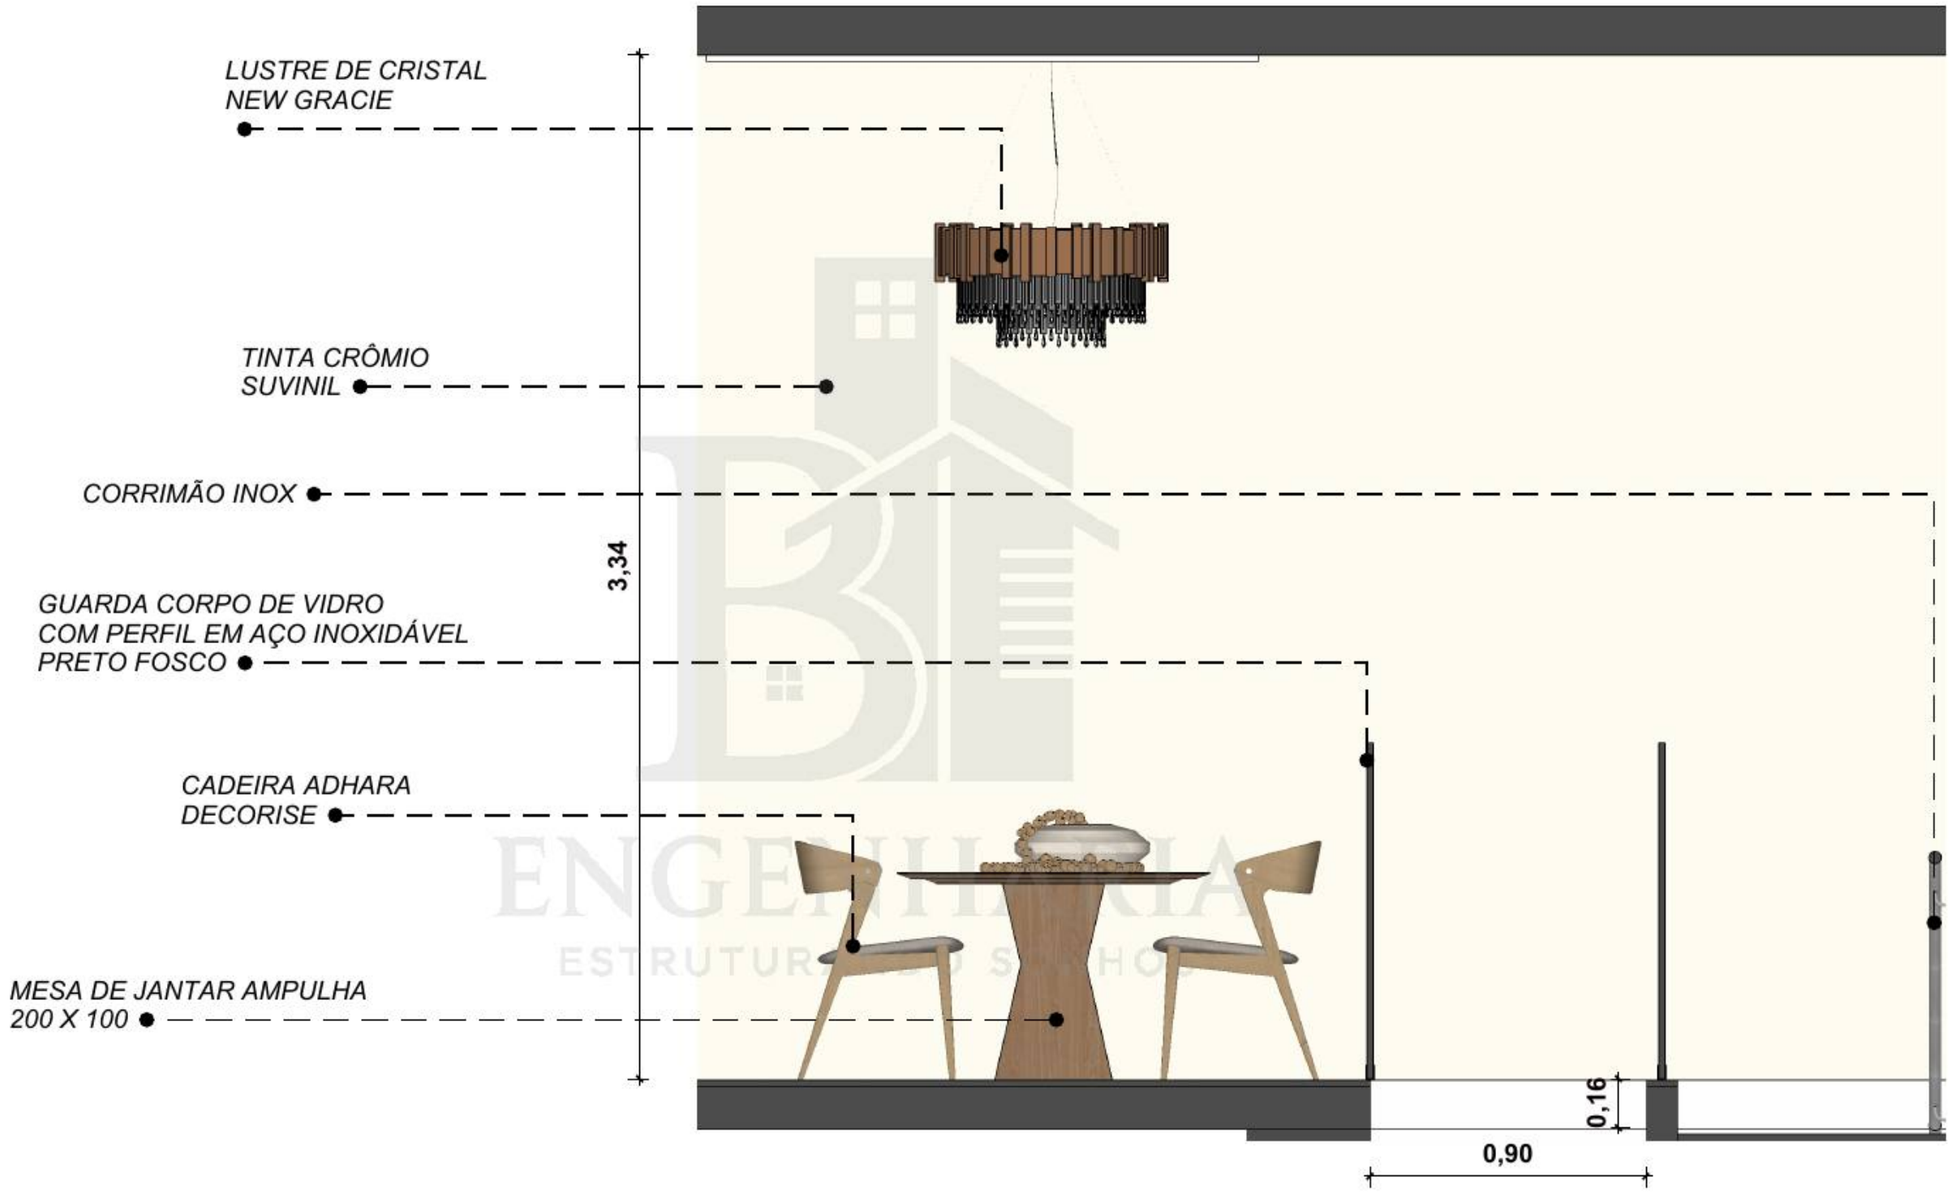

11 **VISTA A - SALA JANTAR**
Esc: 1/20

ENGENHARIA
ESTRUTURAL

SALA DE JANTAR - VISTA B

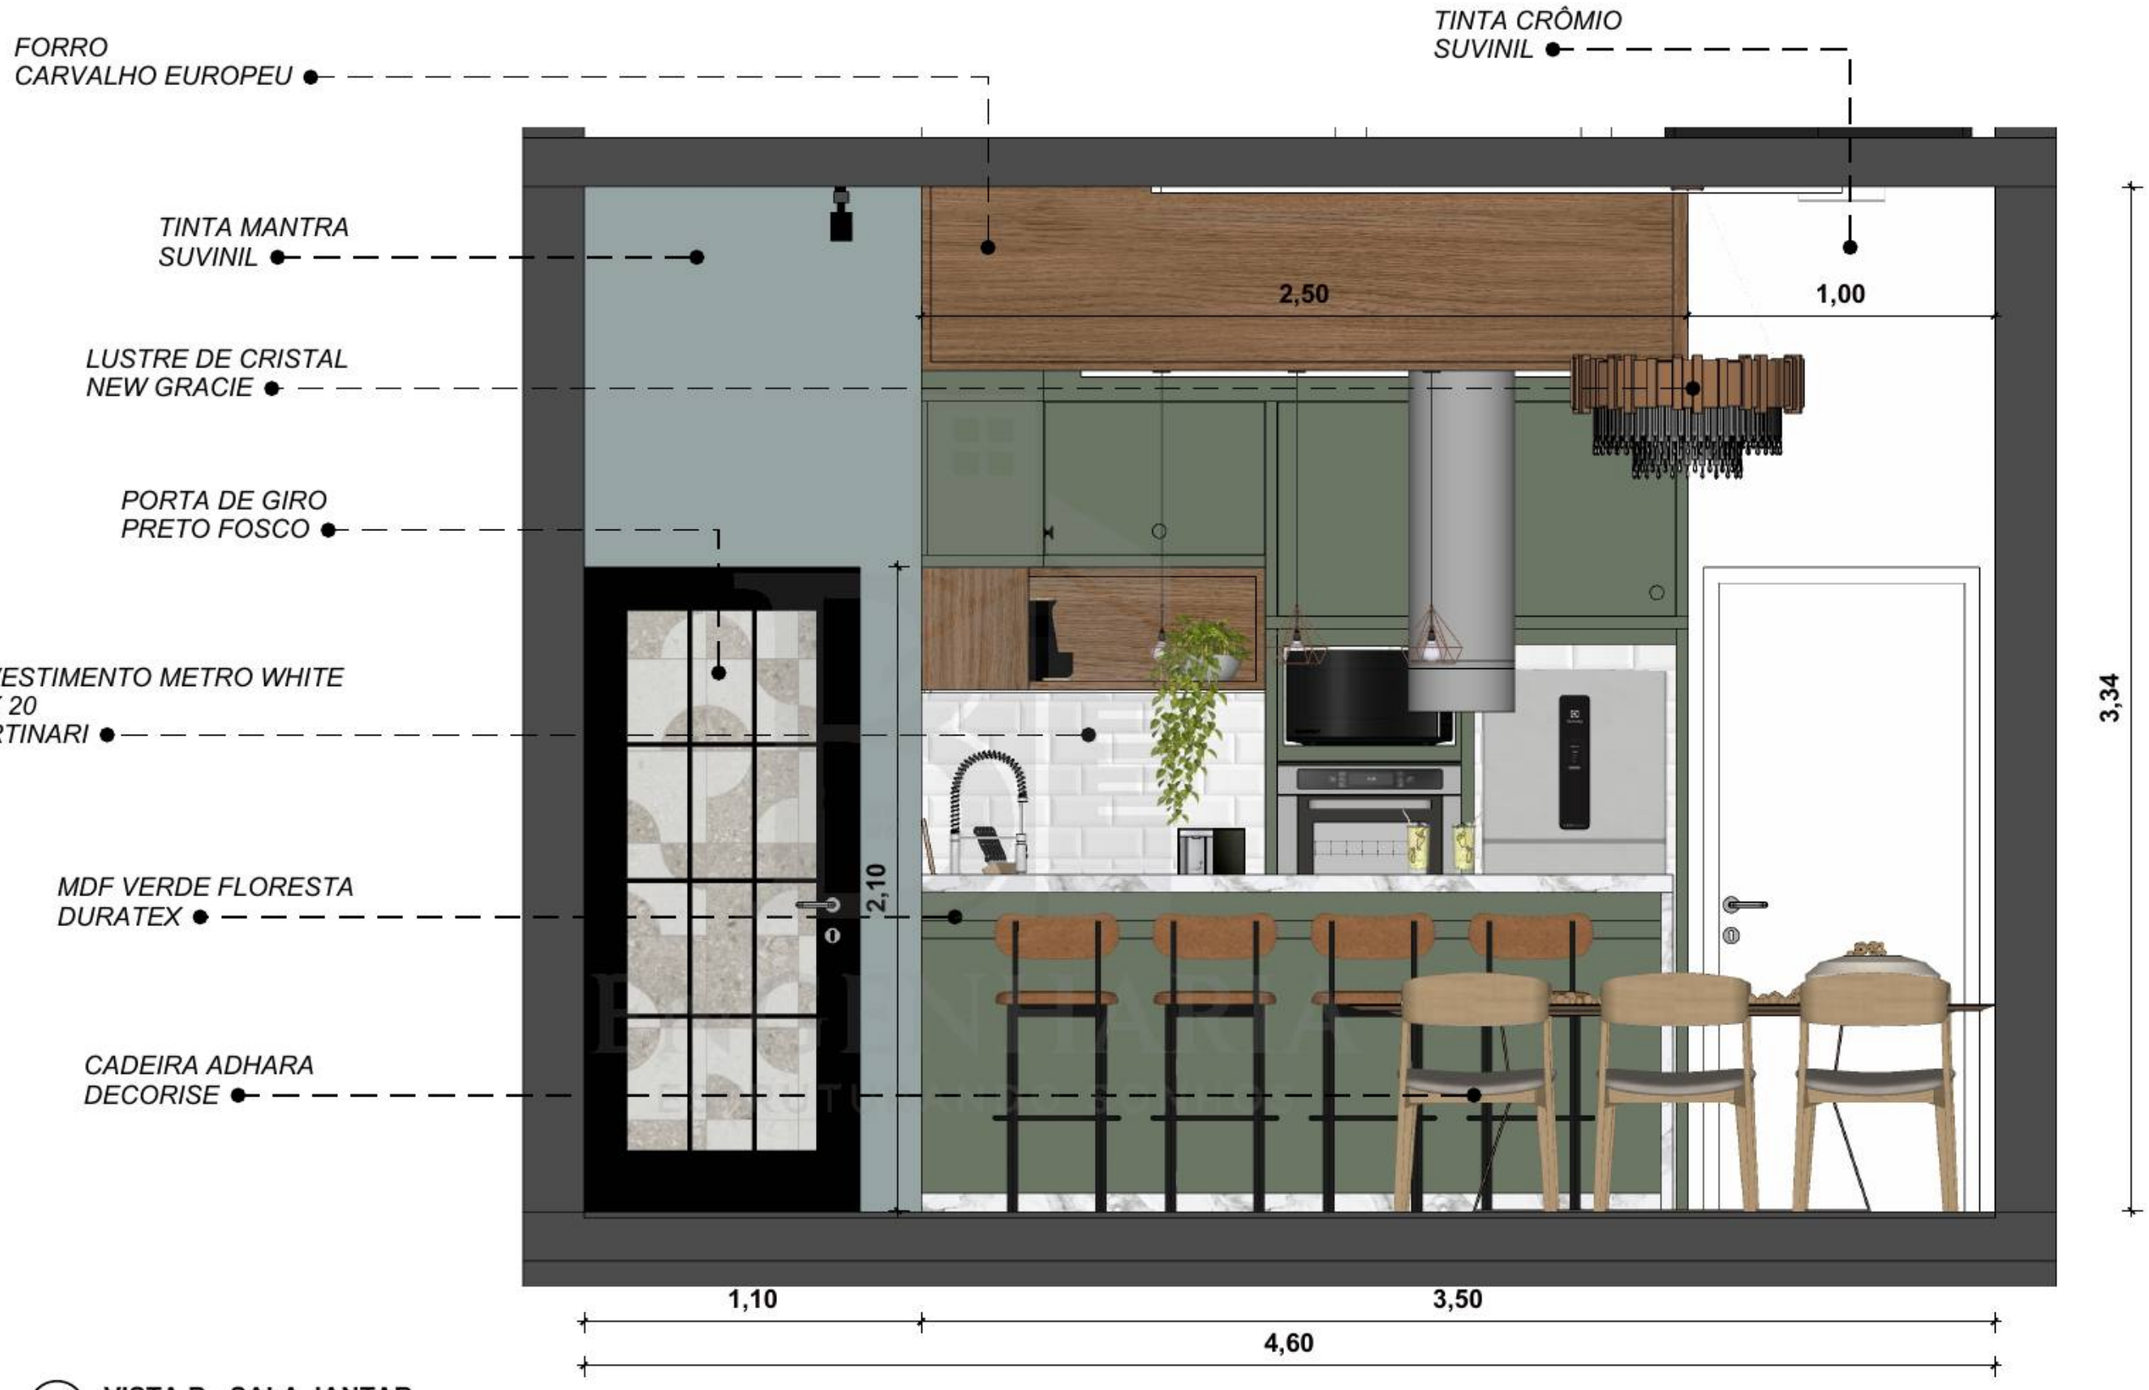

12 **VISTA B - SALA JANTAR**
Esc: 1/20

SALA DE JANTAR - VISTA C

REVESTIMENTO METRO WHITE
10 X 20
PORTINARI

COBOGÓ
COMFORT NEVADA

LUSTRE DE CRISTAL
NEW GRACIE

TINTAL MANTRA
SUVINIL


QUADRO DECORATIVO
O2 ARTS
KIT TRIPLO

MESA DE JANTAR AMPULHA
200 X 100

CADEIRA ADHARA
DECORISE

CORRIMÃO INOX


GUARDA CORPO DE VIDRO
COM PERFIL EM AÇO INOXIDÁVEL
PRETO FOSCO

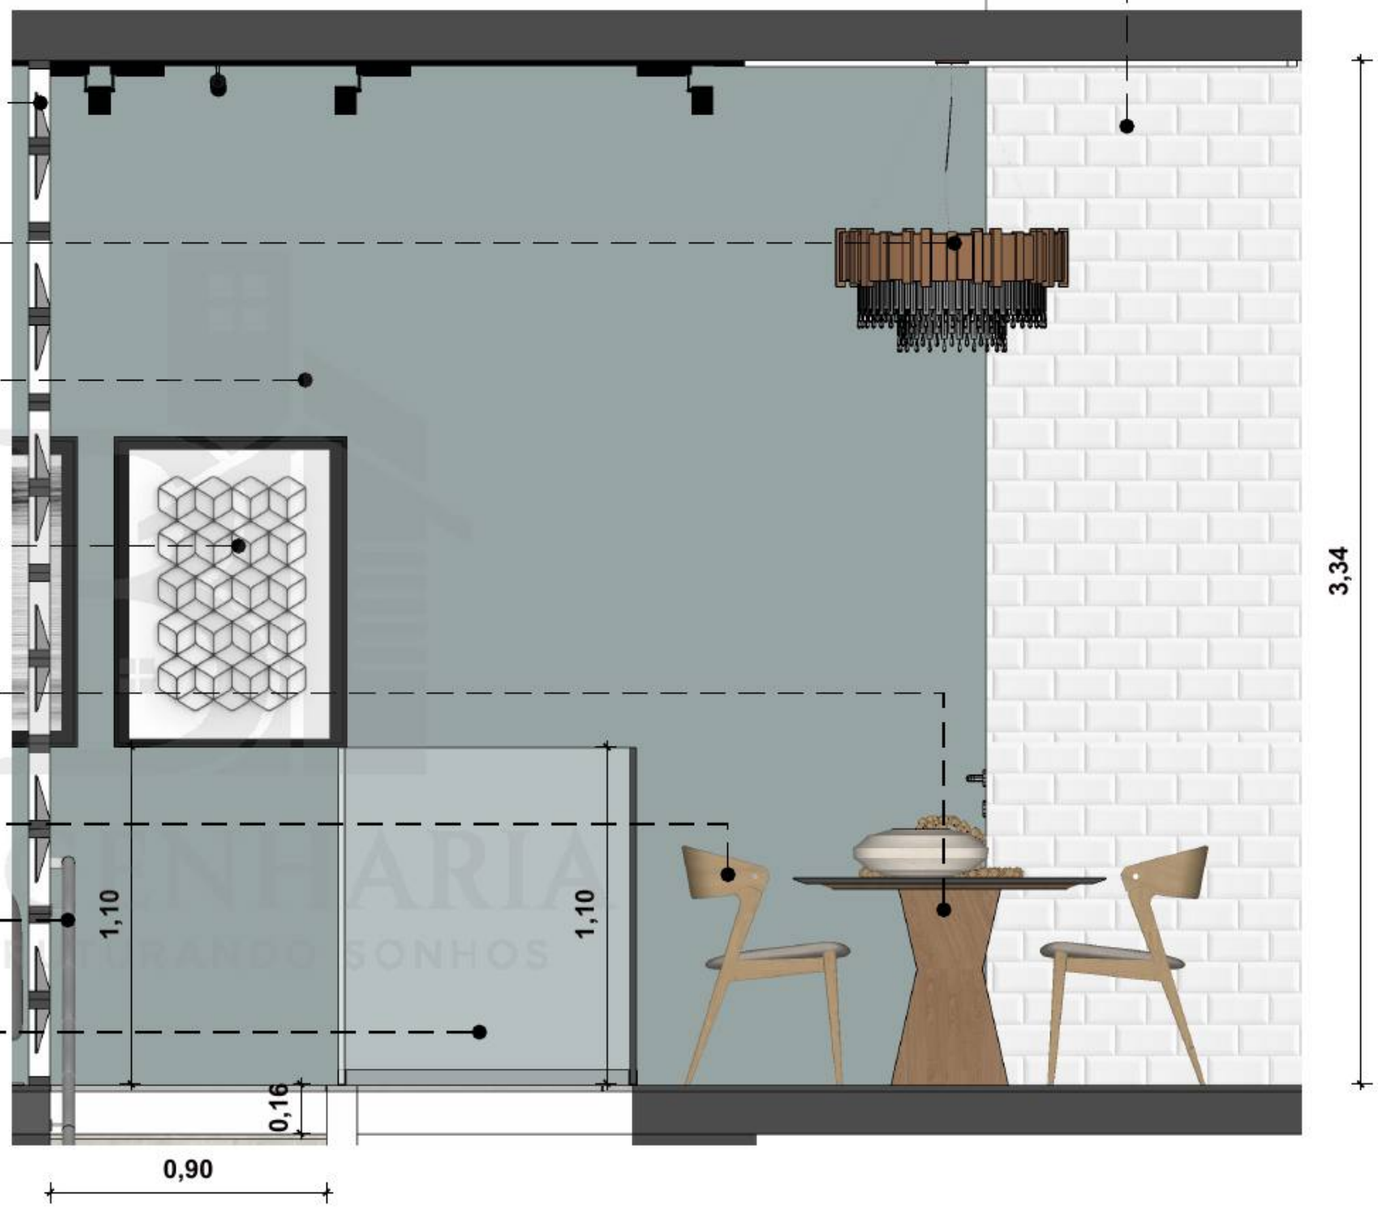

13 **VISTA C - SALA JANTAR**
Esc: 1/20


ENGENHARIA
ESTRUTURANDO SONHOS

SALA DE JANTAR - VISTA D

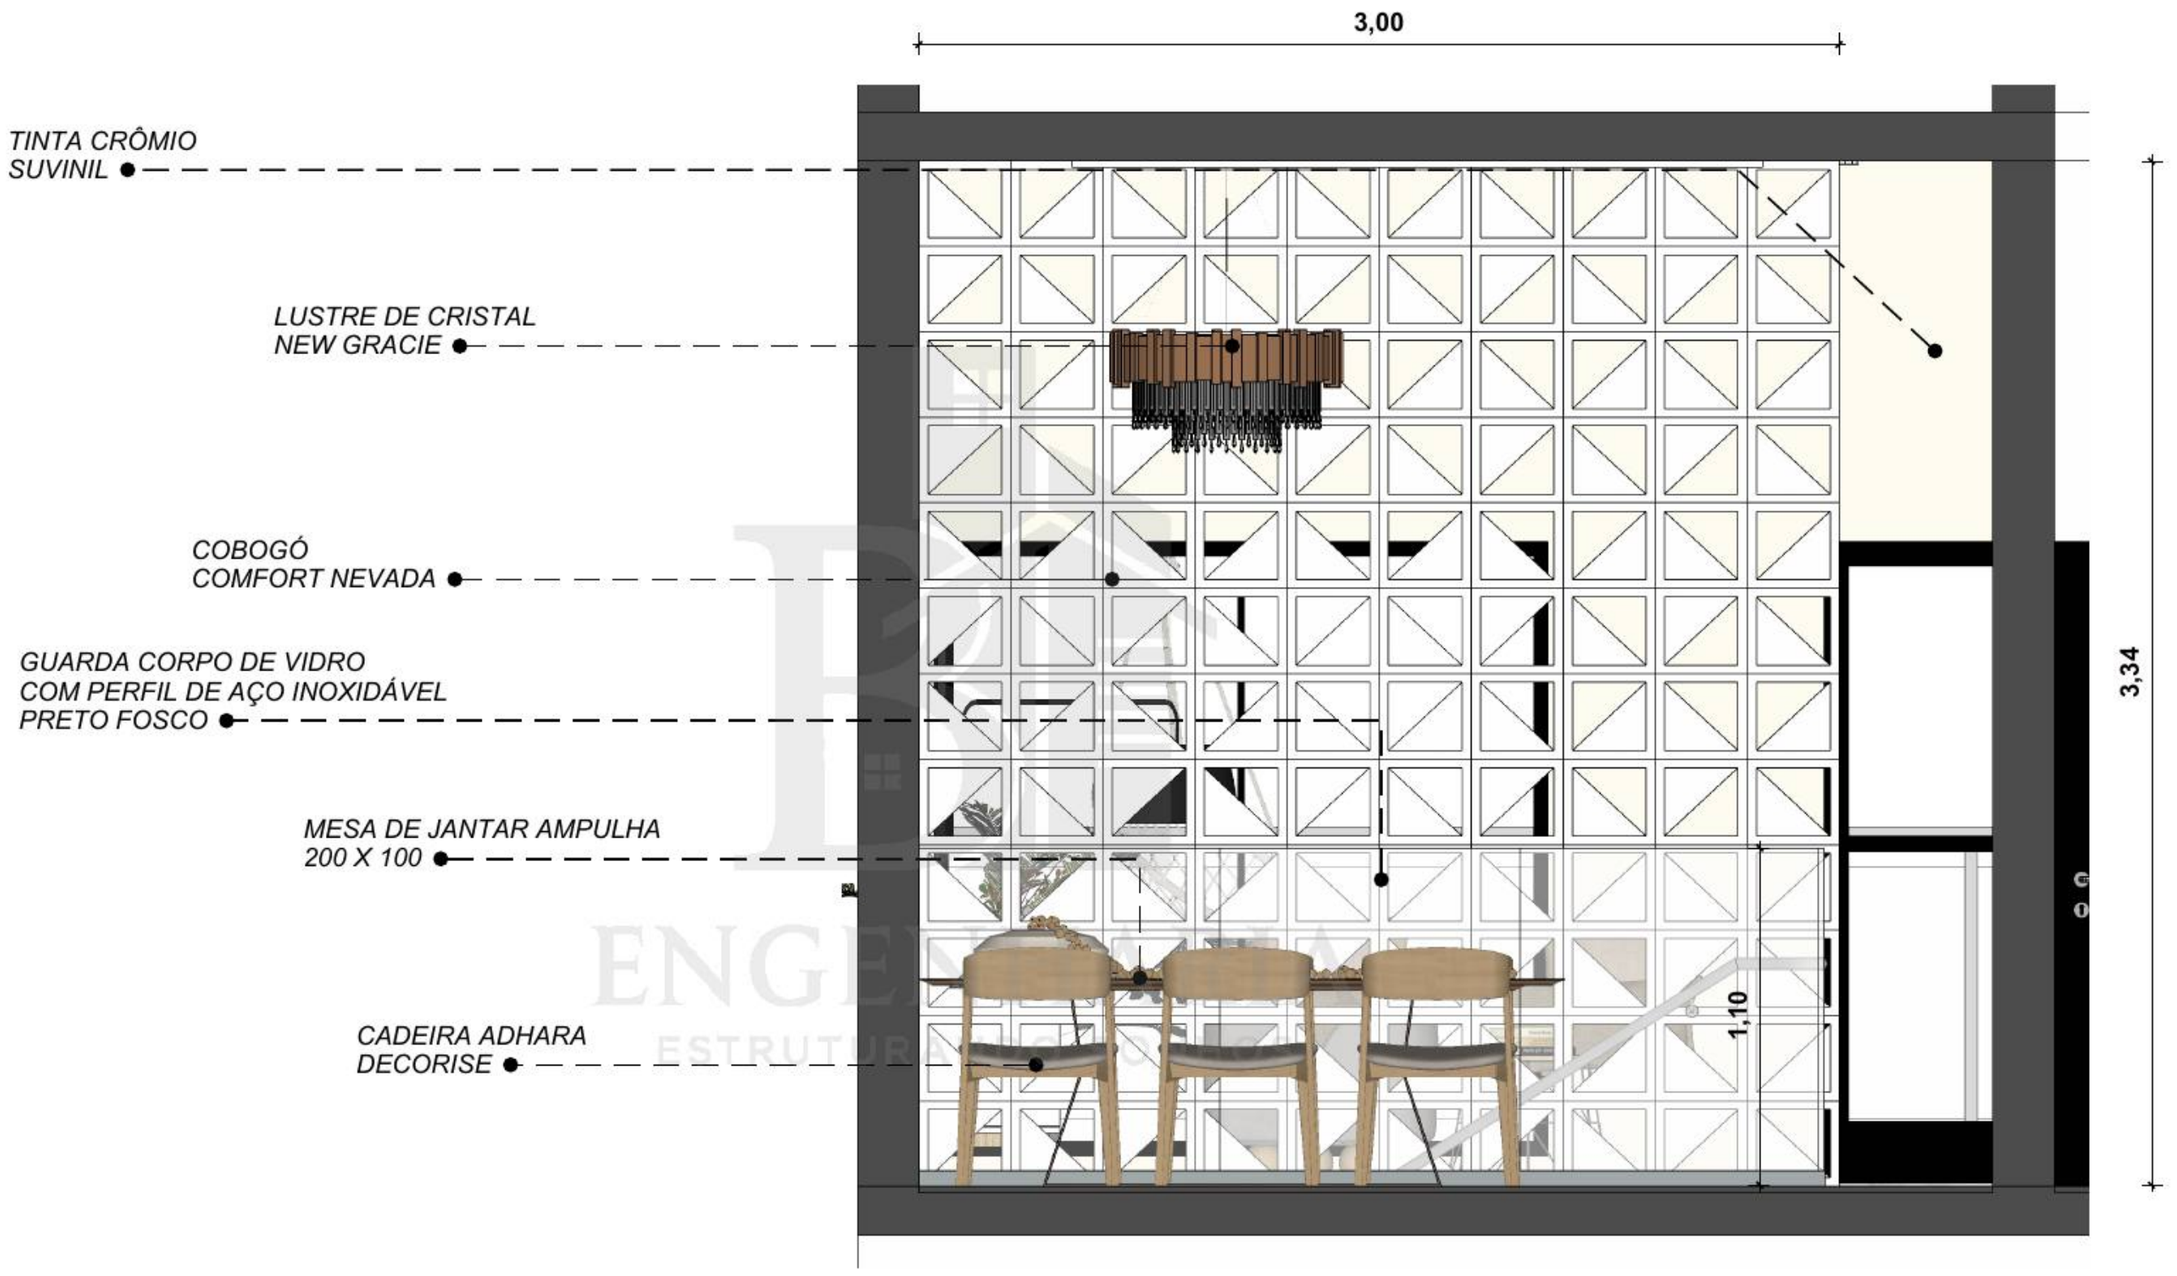

14 **VISTA D - SALA JANTAR**
Esc: 1/20


SALA DE ESTAR - PLANTA BAIXA

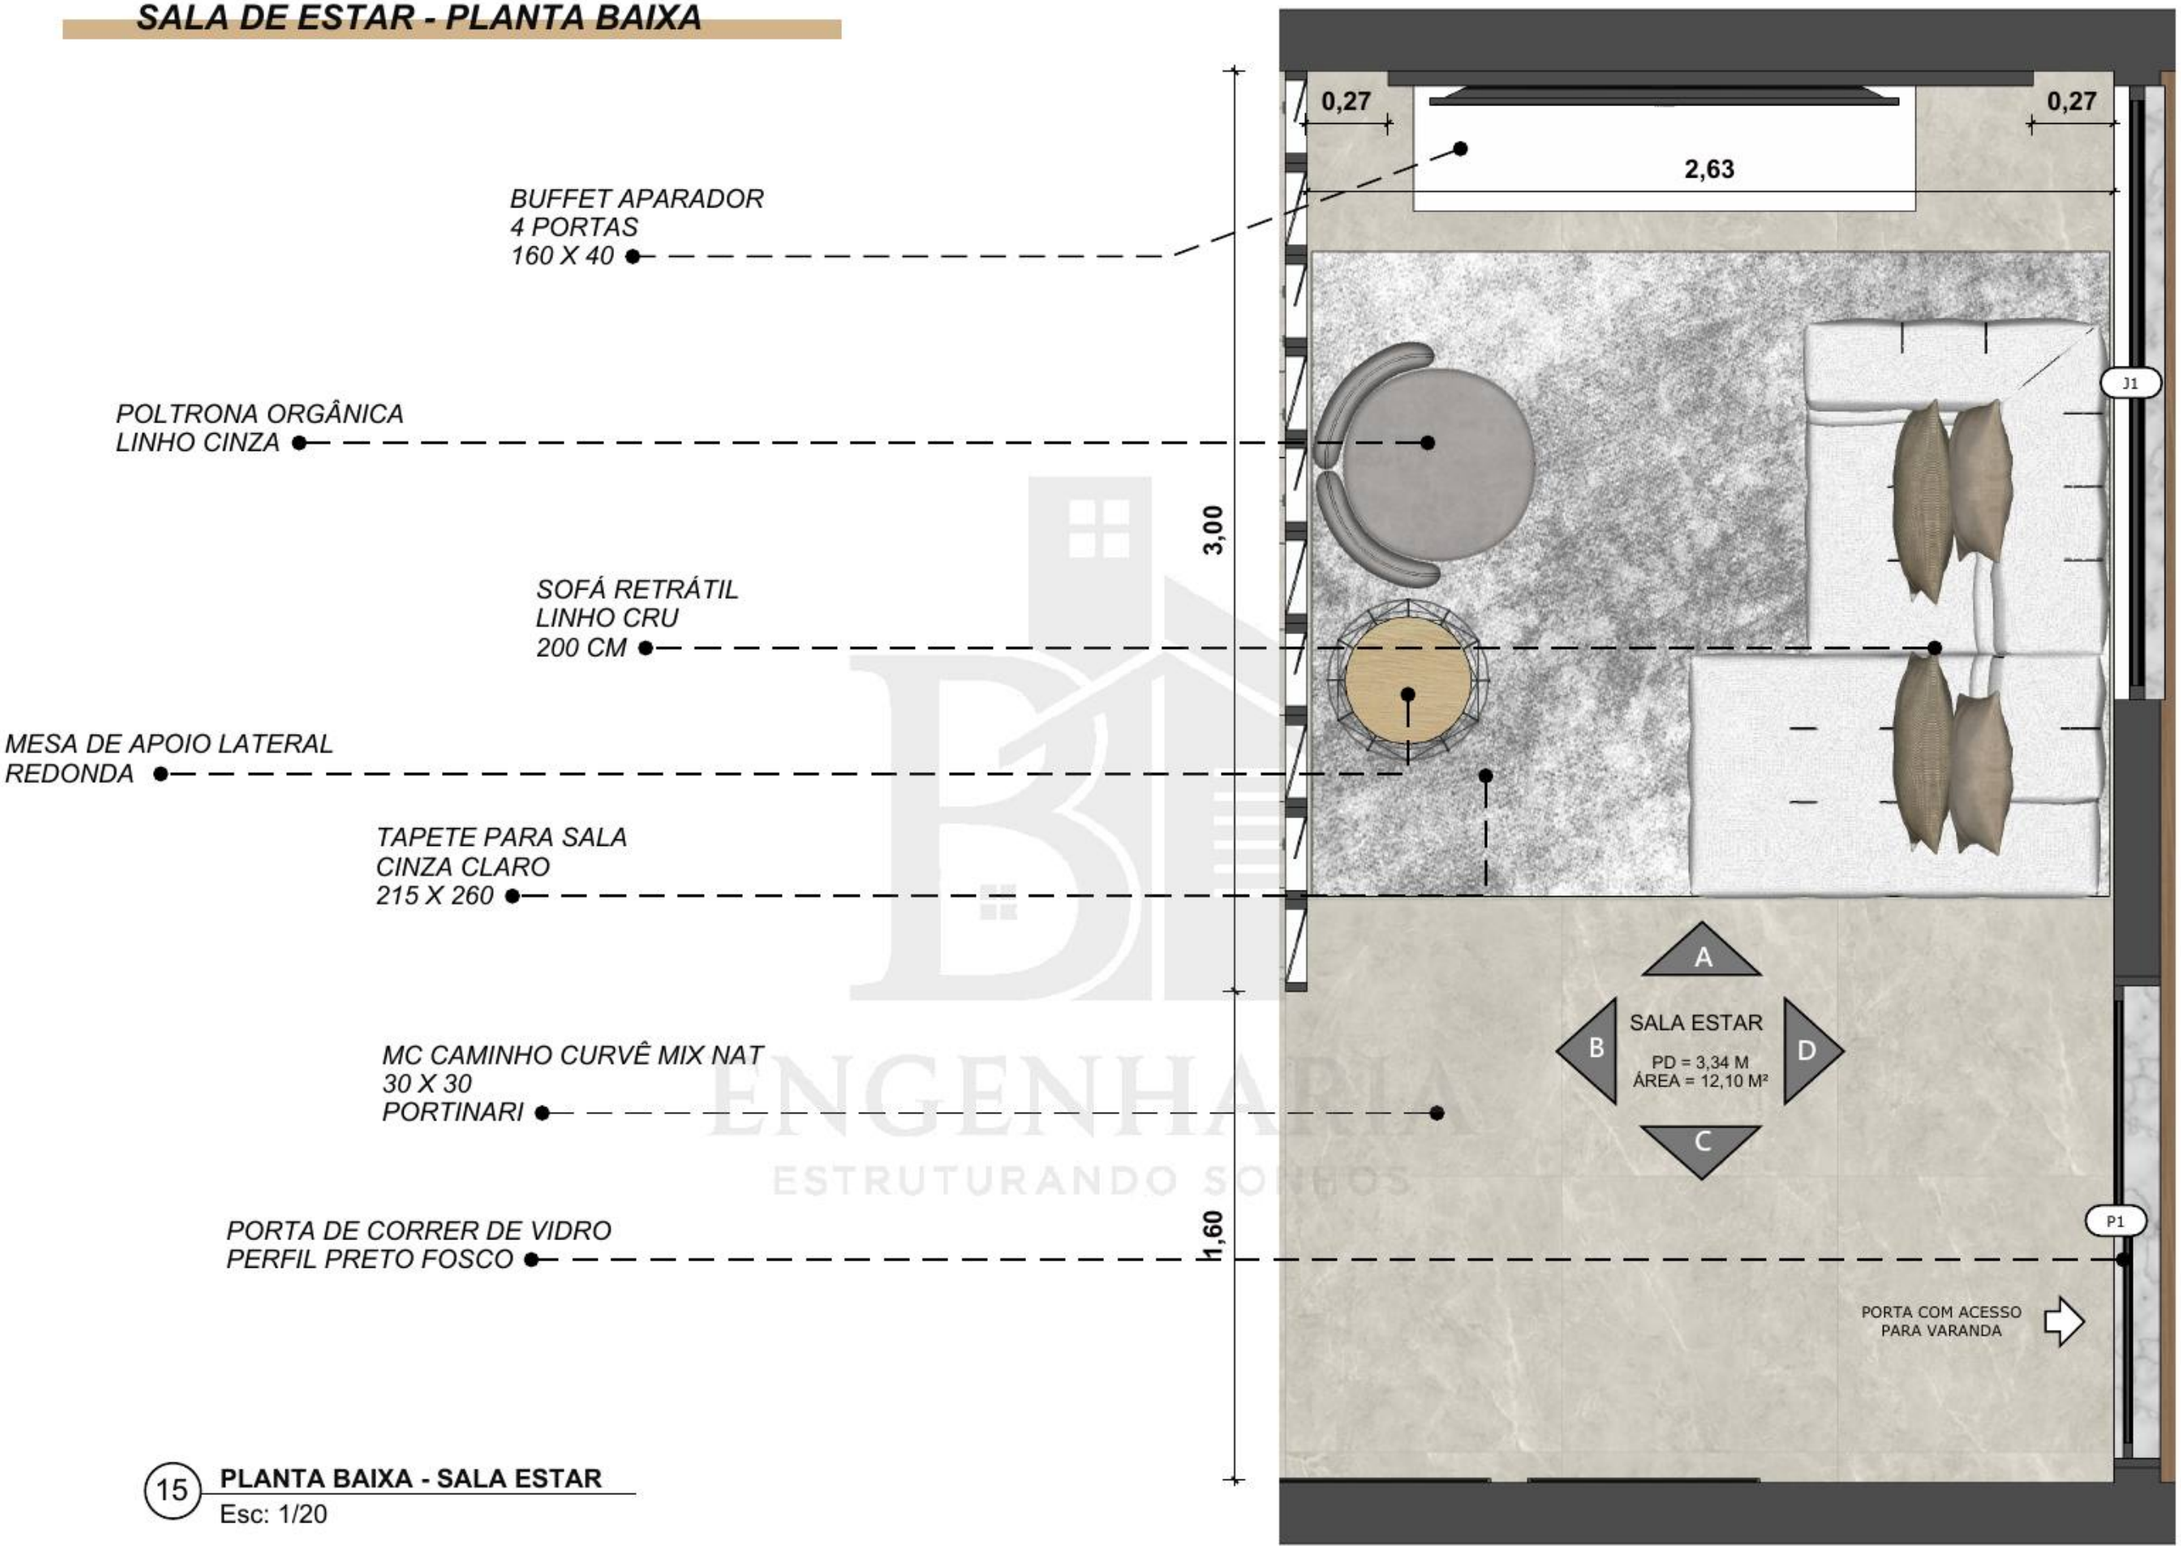

15 **PLANTA BAIXA - SALA ESTAR**
Esc: 1/20

DF ENGENHARIA
ESTRUTURANDO SONHOS


SALA DE ESTAR - VISTA A

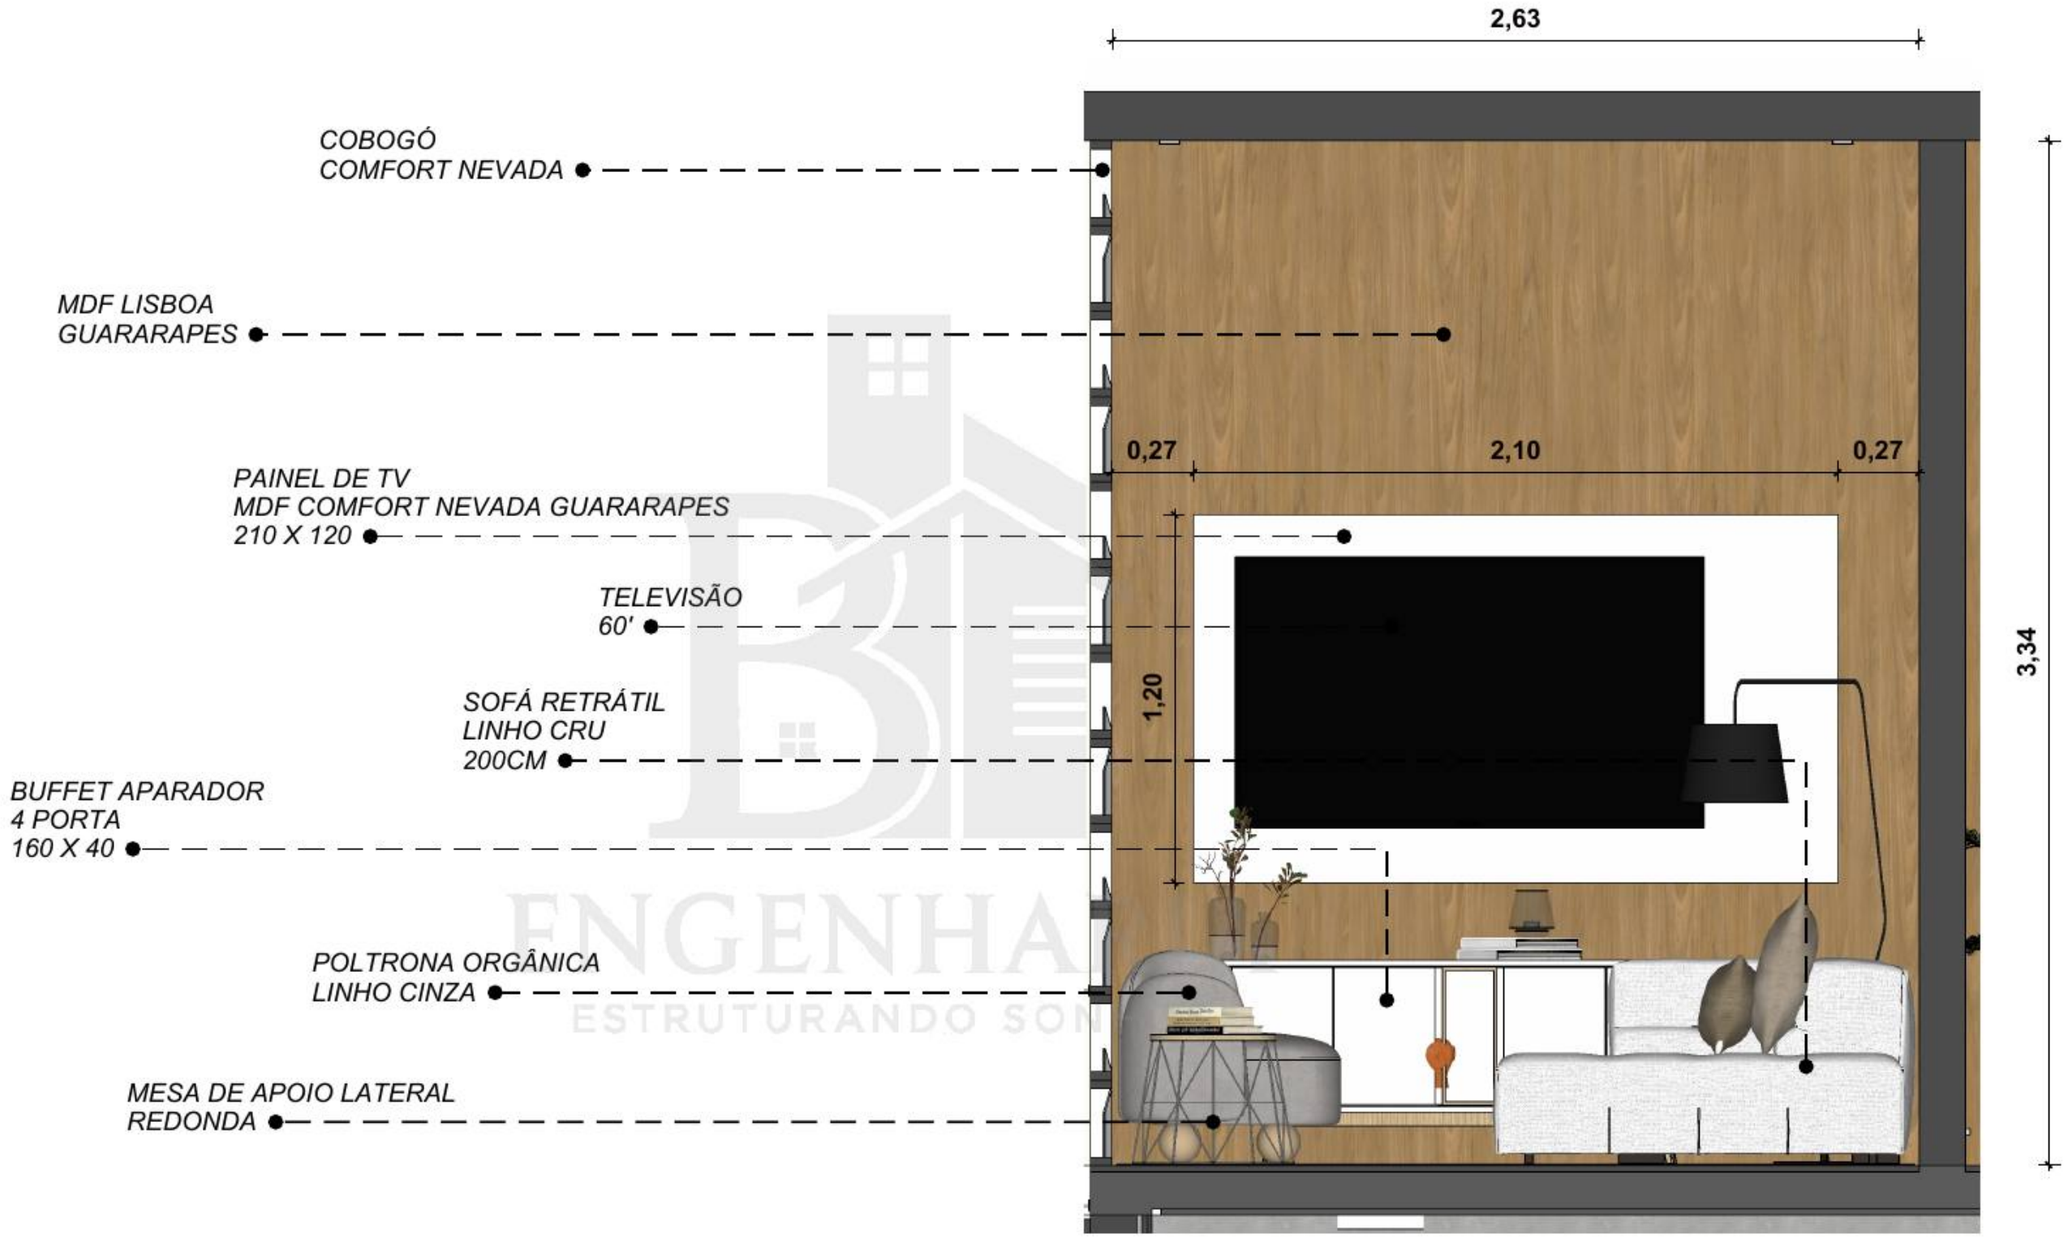

16 **VISTA A - SALA ESTAR**
Esc: 1/20

ENGENHARIA
ESTRUTURANDO SONHOS


SALA DE ESTAR - VISTA B

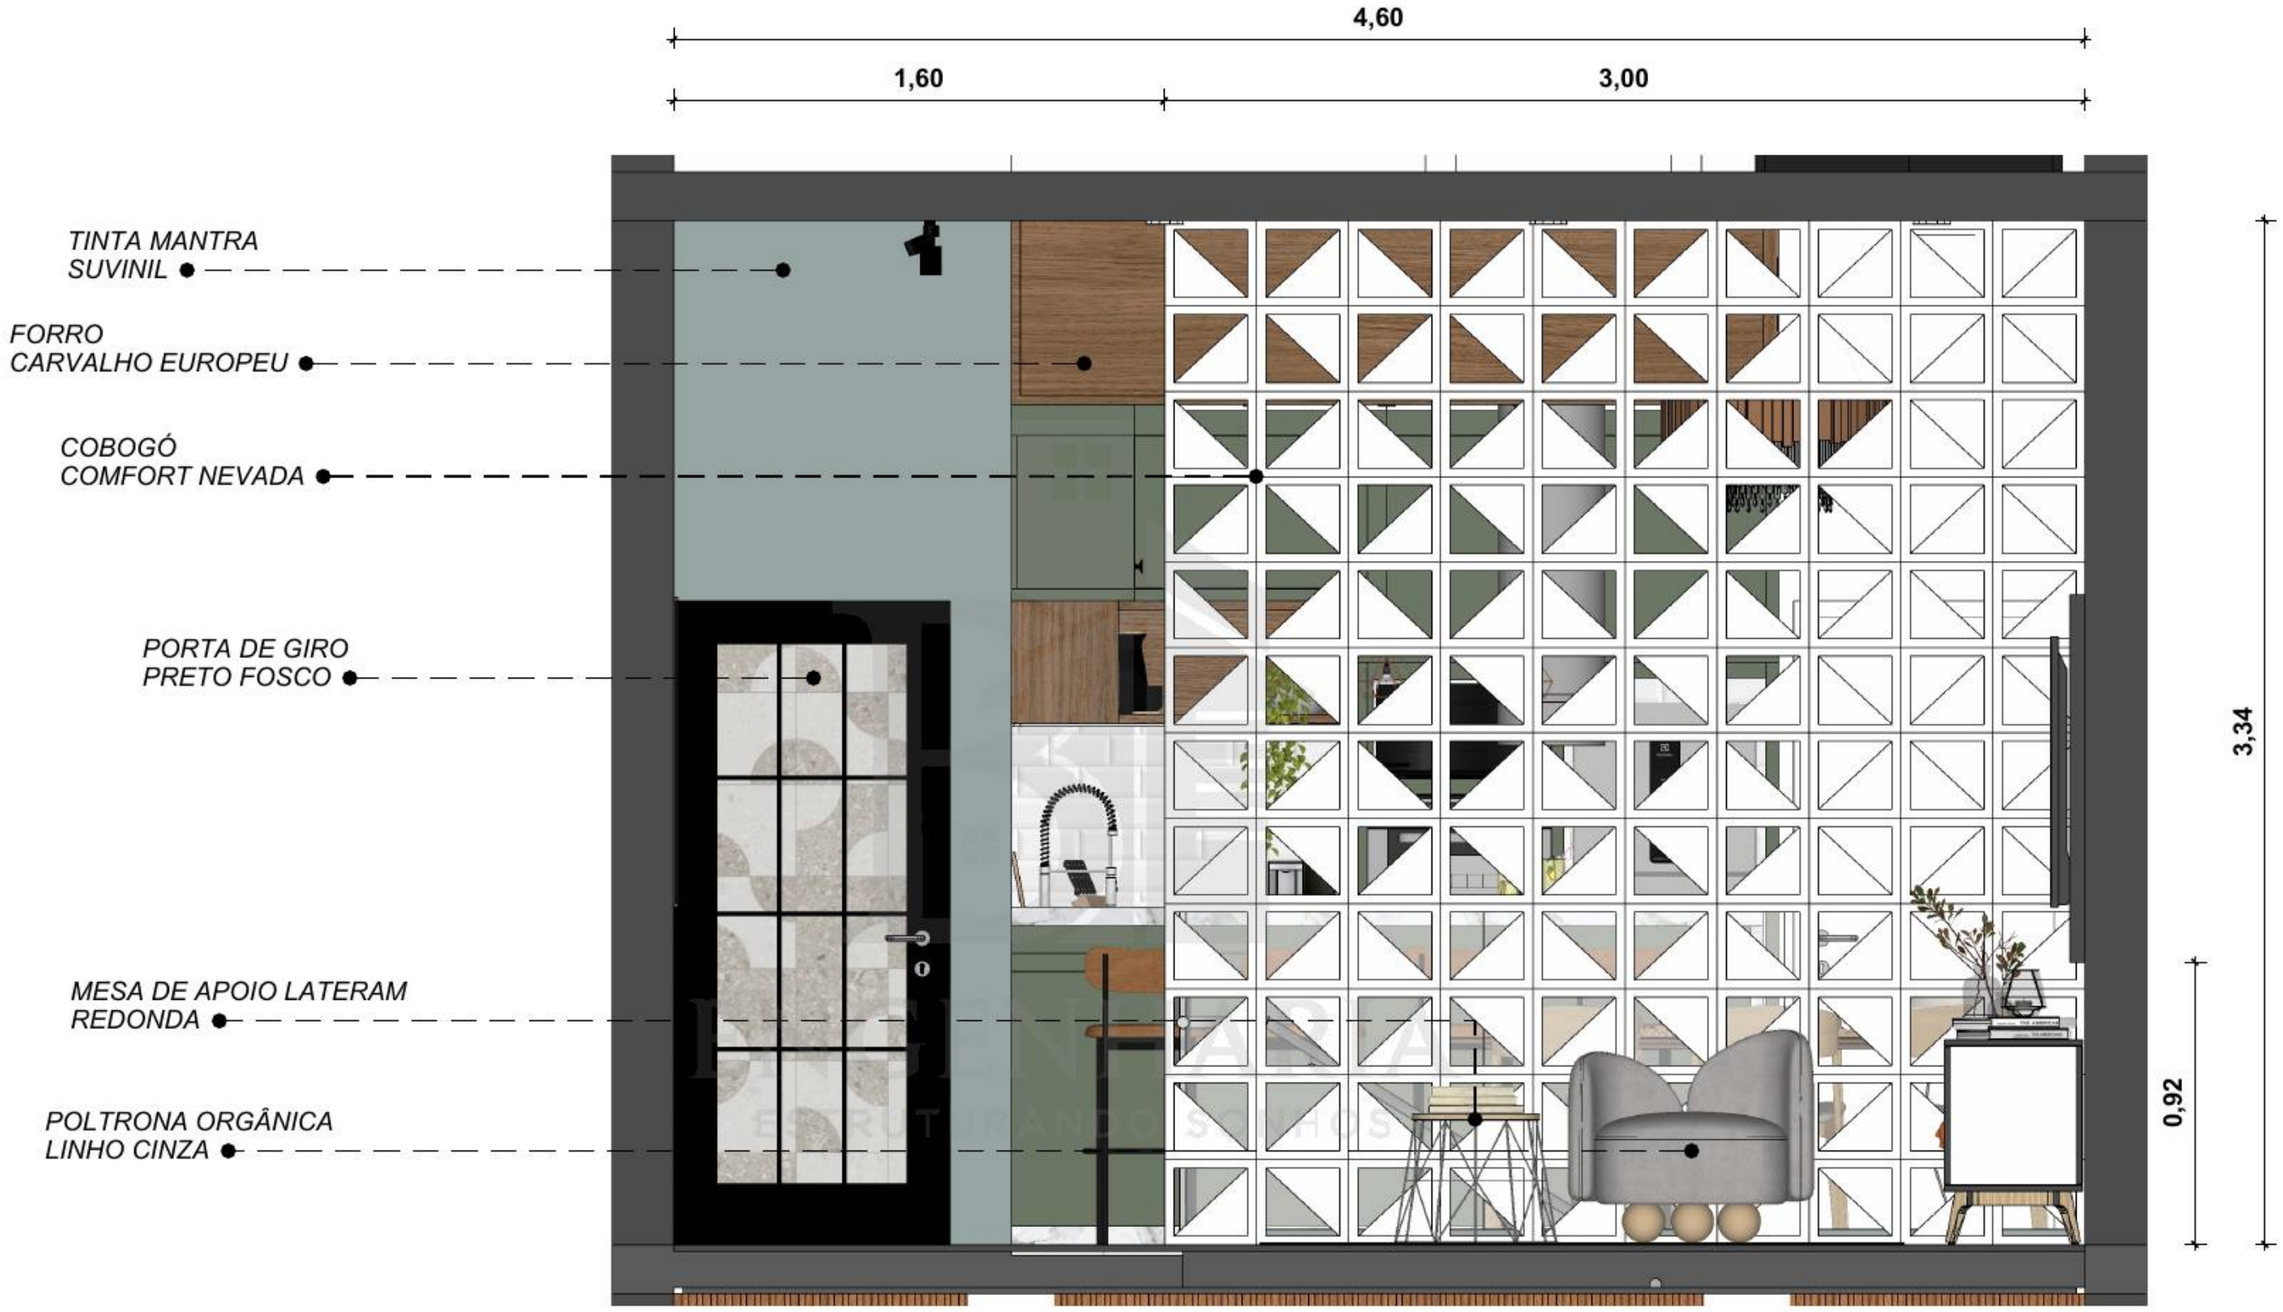

17 **VISTA B - SALA ESTAR**
Esc: 1/20

PRANCHA
17/60

SALA DE ESTAR - VISTA C

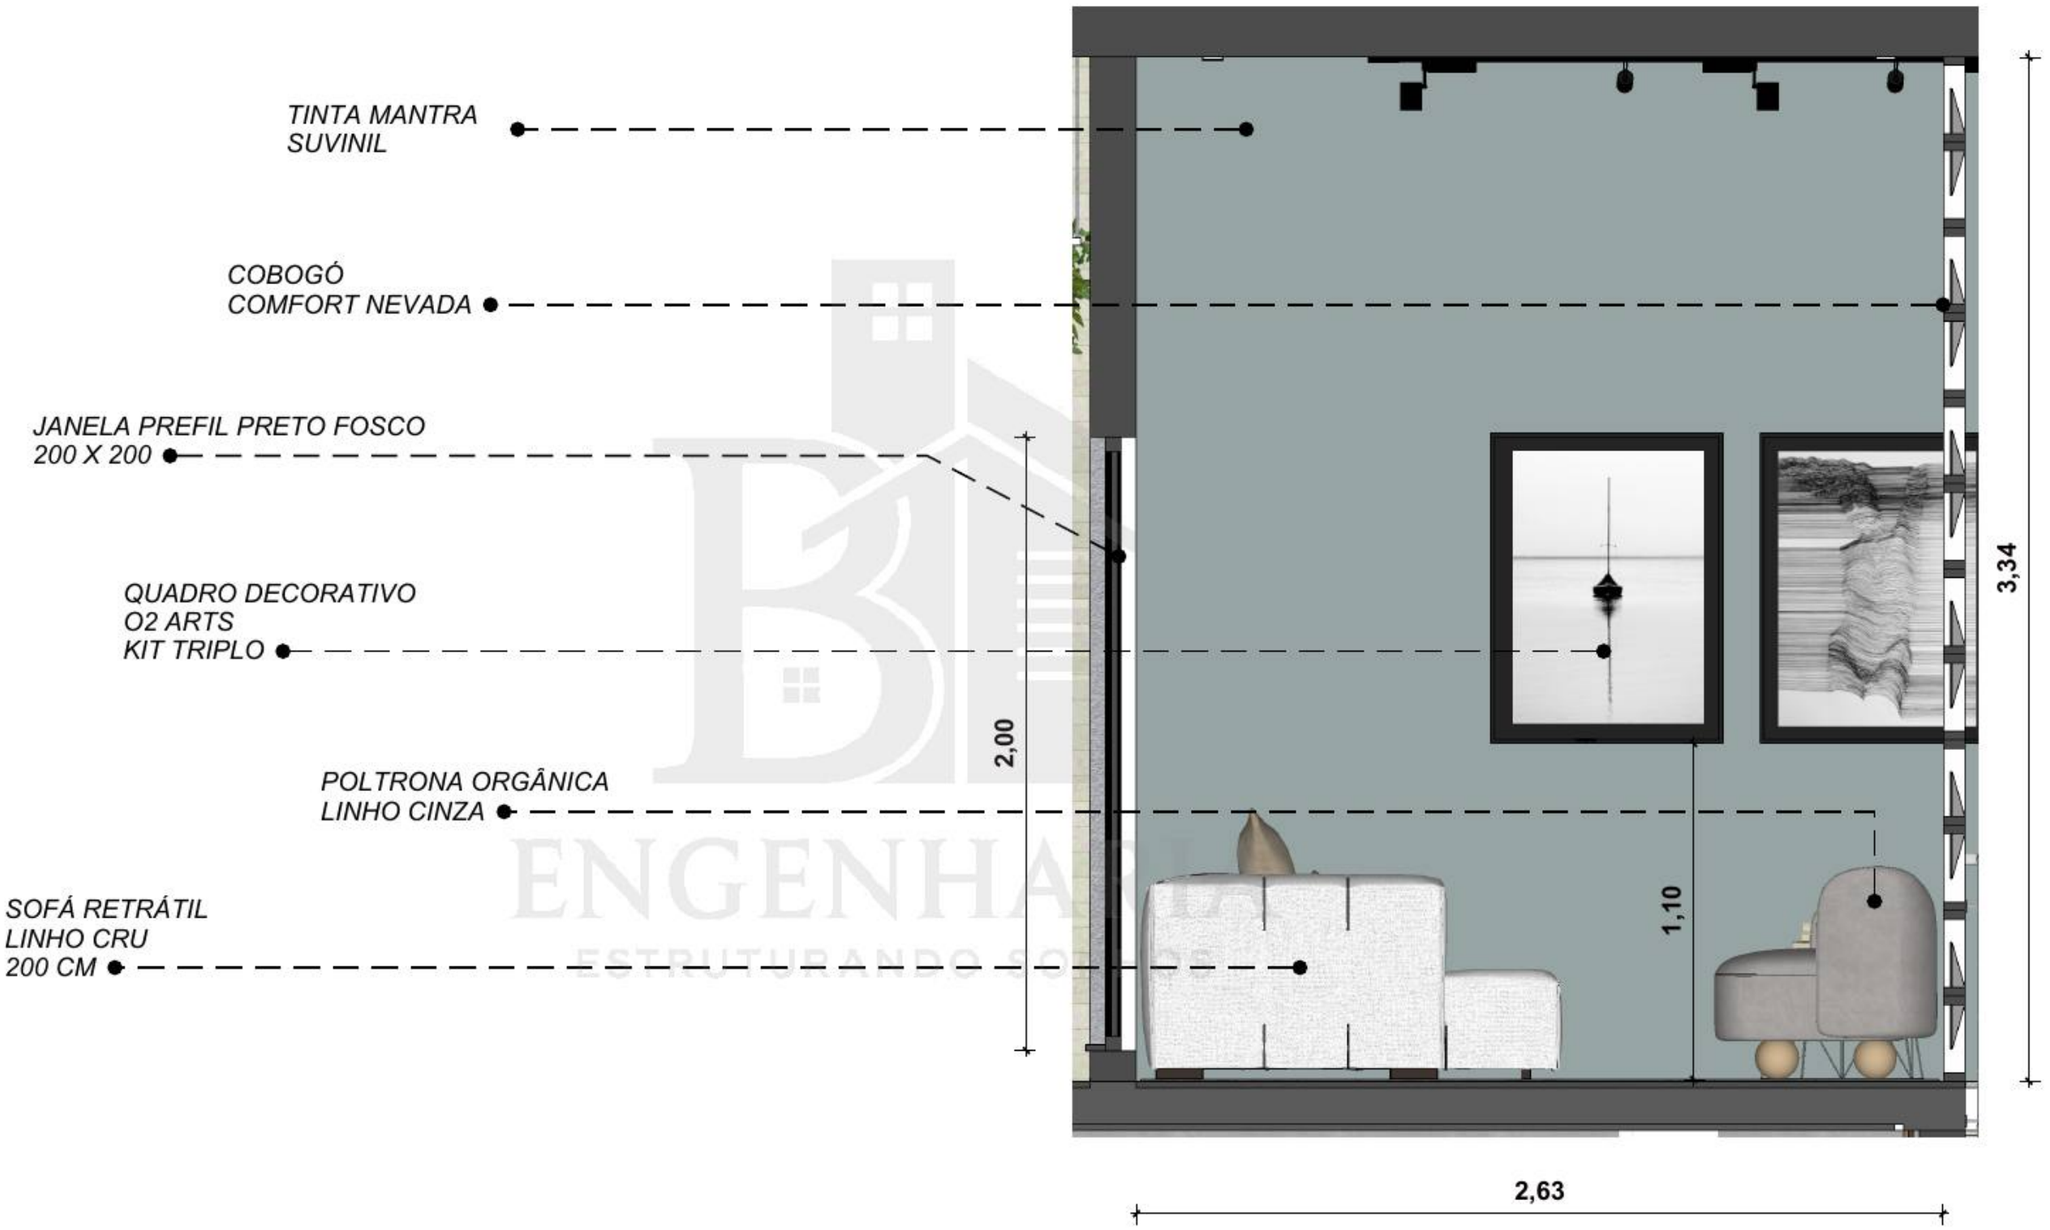

18 **VISTA C - SALA ESTAR**
Esc: 1/20


ENGENHARIA
ESTRUTURANDO SONHOS

SALA DE ESTAR - VISTA D




19 **VISTA D - SALA ESTAR**
Esc: 1/20


SALA DE ESTAR - DETALHAMENTO

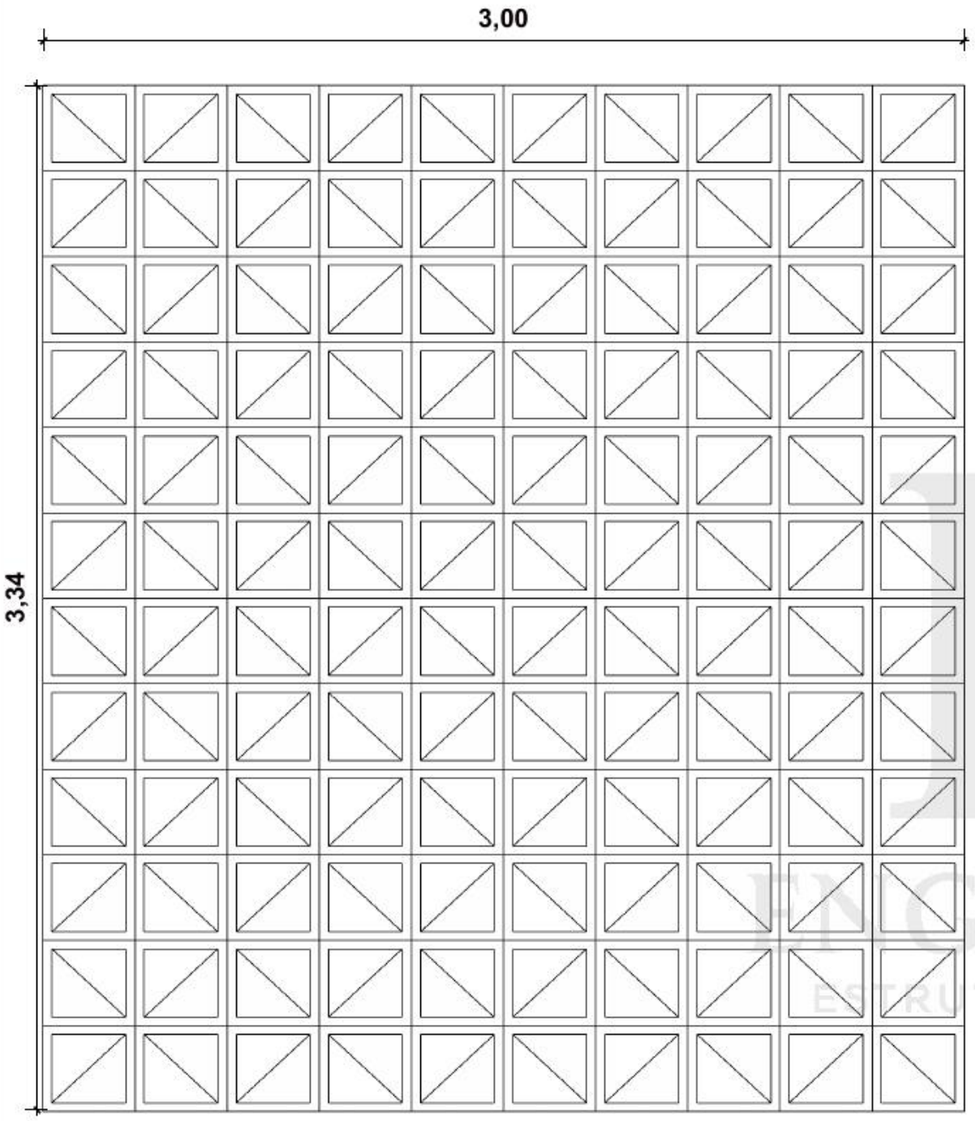


VISTA EM PLANTA - COBOGÓ

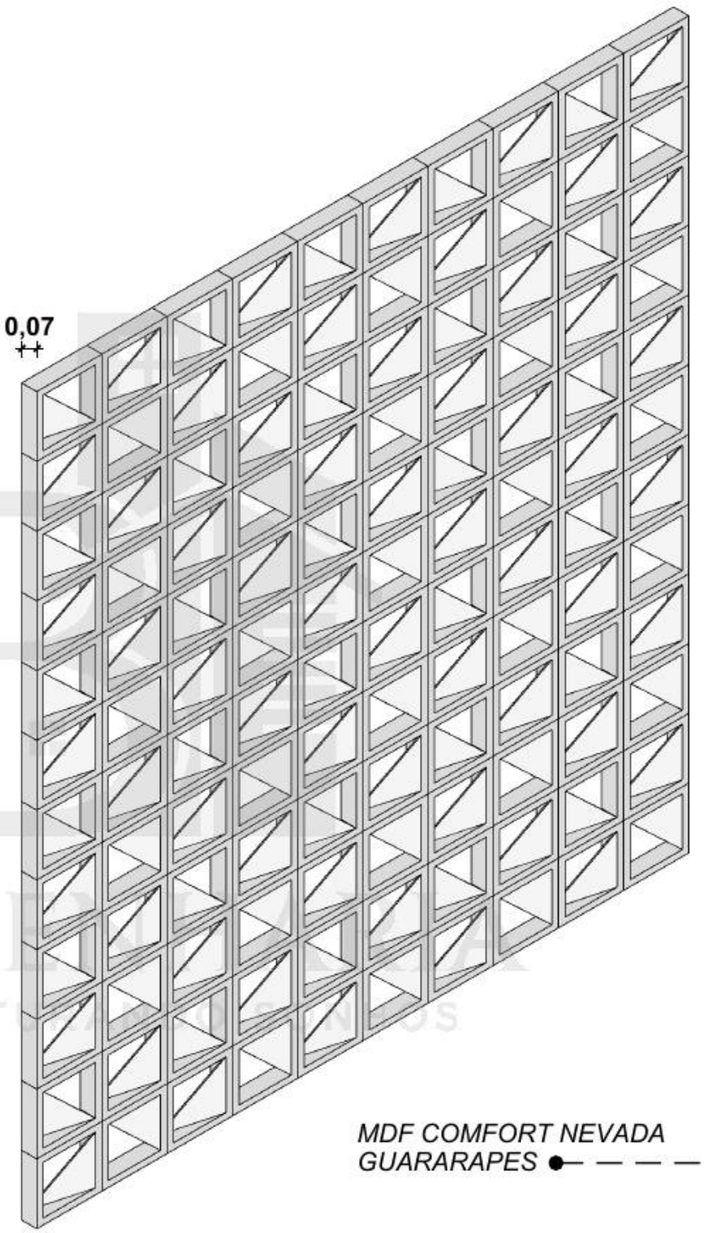


VISTA EM PERSPECTIVA
COBOGÓ

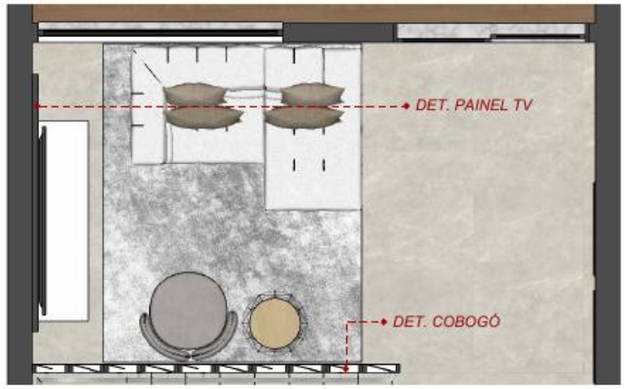

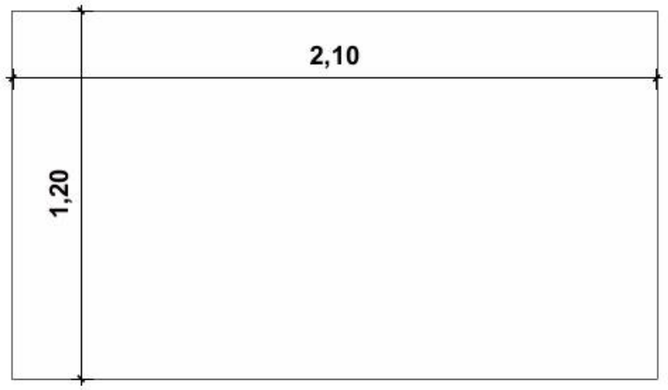

VISTA EM PLANTA
PAINEL TV

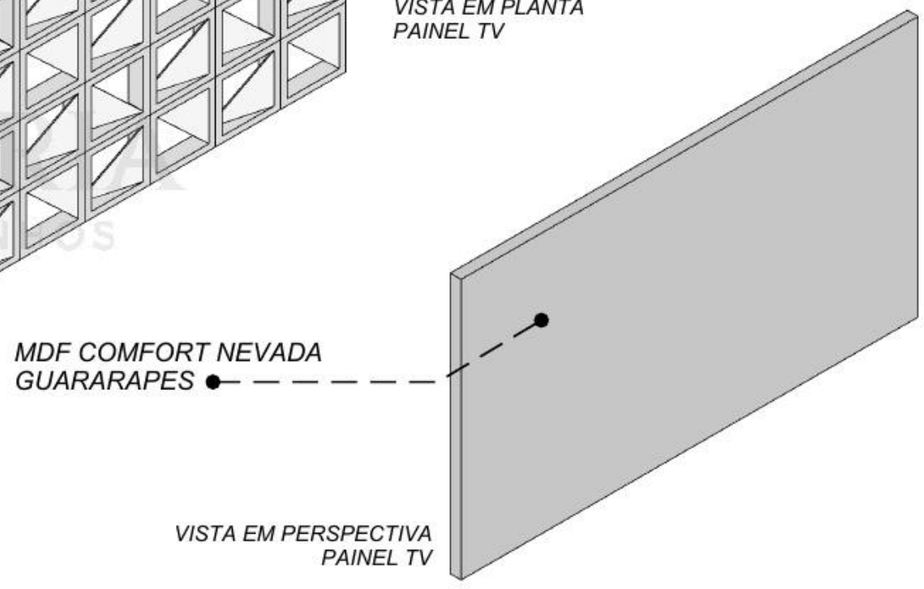

VISTA EM PERSPECTIVA
PAINEL TV

20 **DET. MARCENARIA - SALA ESTAR**
Esc: 1/20

PRANCHA
20/60

VARANDA - PLANTA BAIXA


SOLEIRA
GRANITO SIENA

GUARDA CORPO DE VIDRO
PERFIL EM AÇO INOXIDÁVEL
PRETO FOSCO

JANELA
2 FOLHAS
PERFIL PRETO FOSCO

PISO VINÍLICO AMADEIRADO
JACARANDÁ


PORTA DE GIRO
AÇO PRETO FOSCO

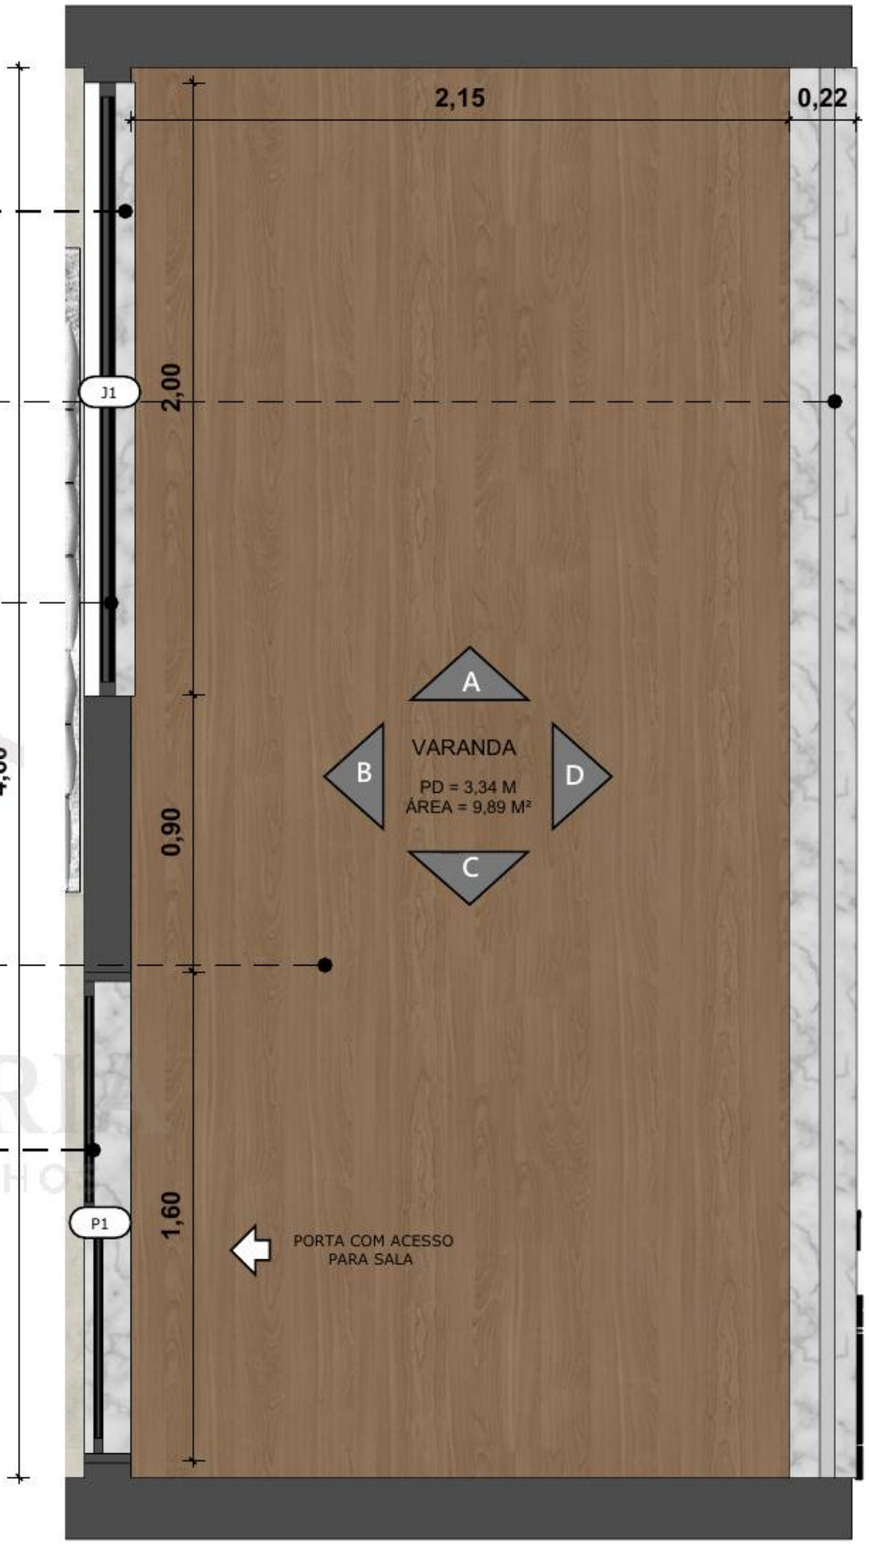

21 **PLANTA BAIXA - VARANDA**
Esc: 1/20

ENGENHARIA
ESTRUTURANDO SONHOS

VARANDA - VISTA A

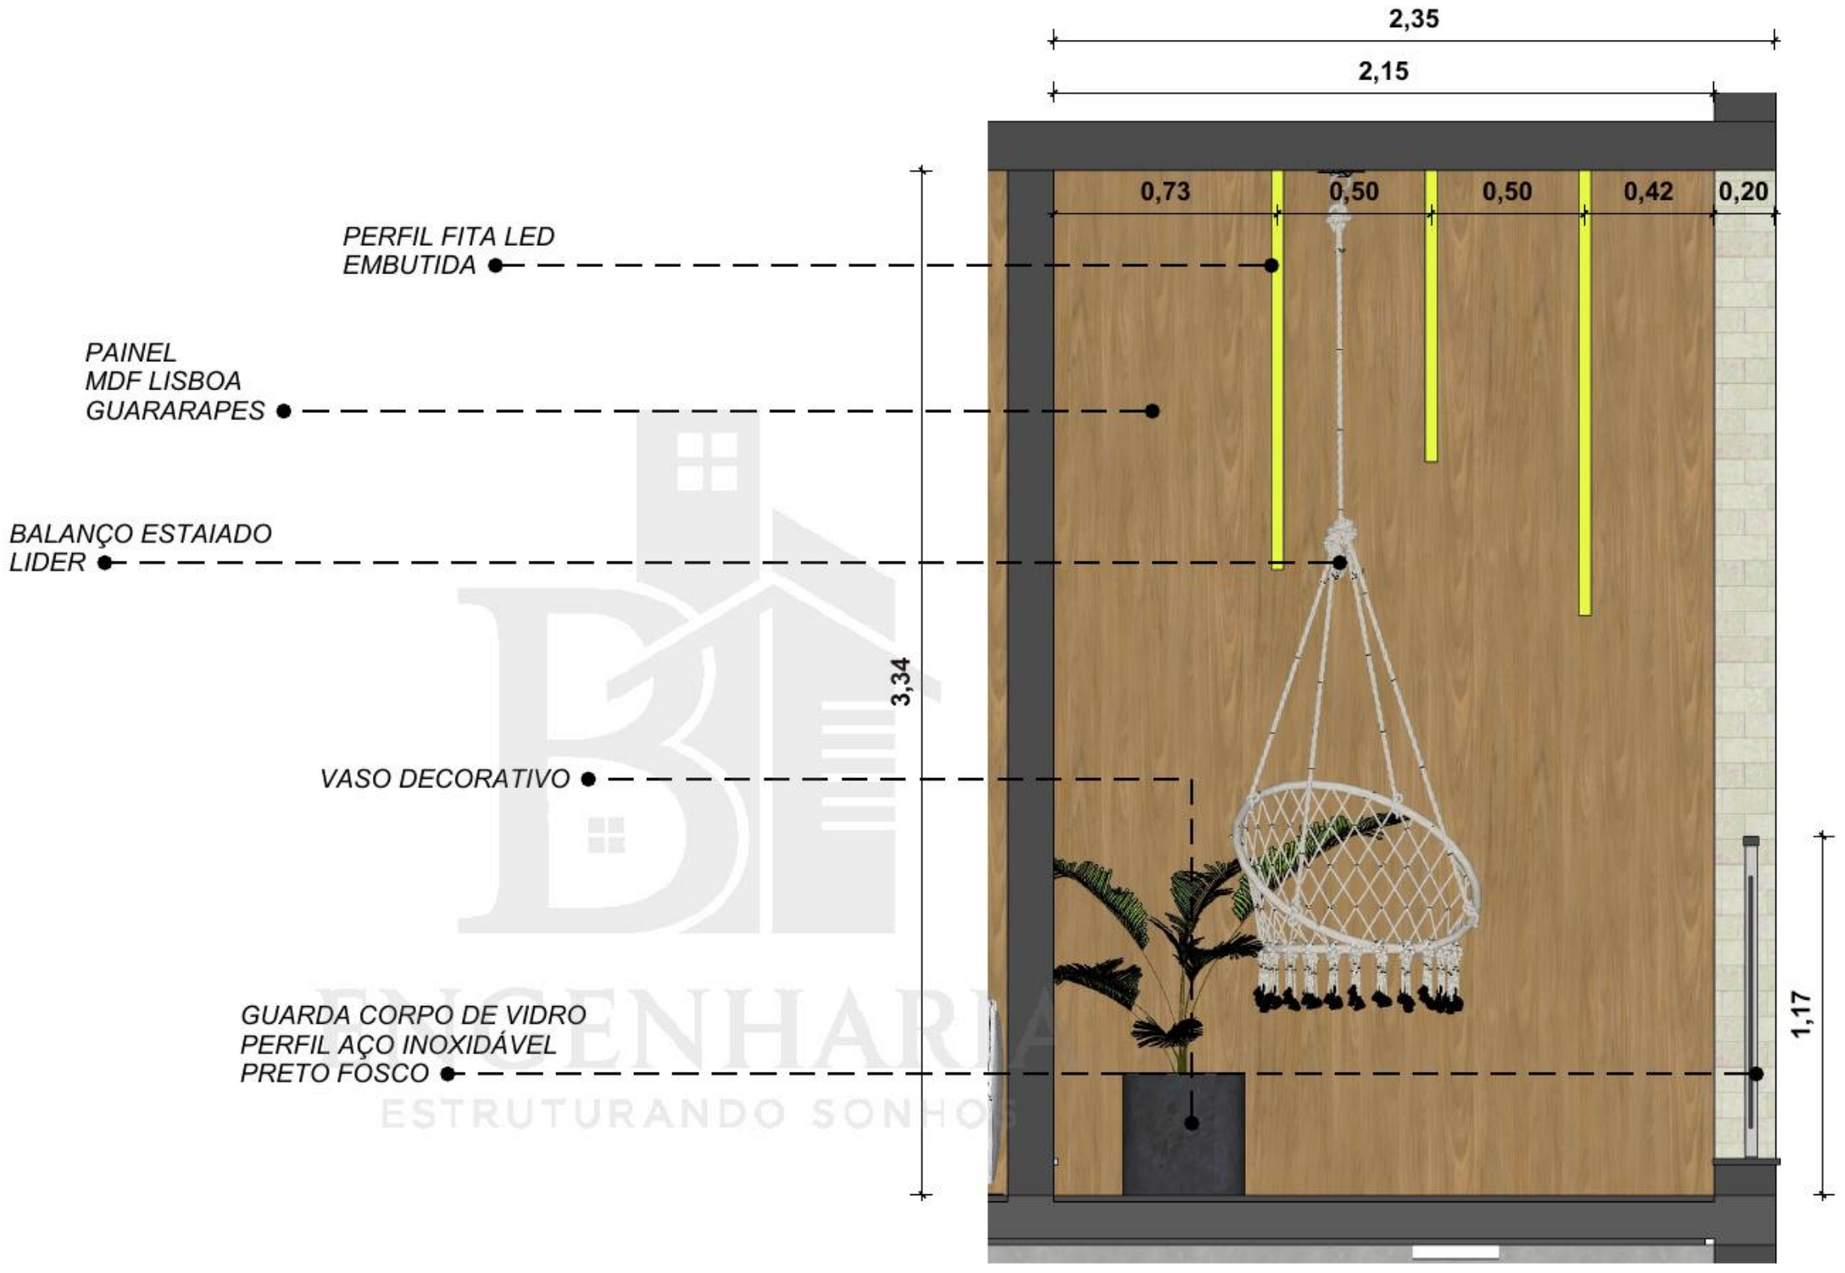

22 **VISTA A - VARANDA**
Esc: 1/20


DF ENGENHARIA
ESTRUTURANDO SONHOS

VARANDA - VISTA B



23 **VISTA B - VARANDA**
Esc: 1/20


VARANDA - VISTA C

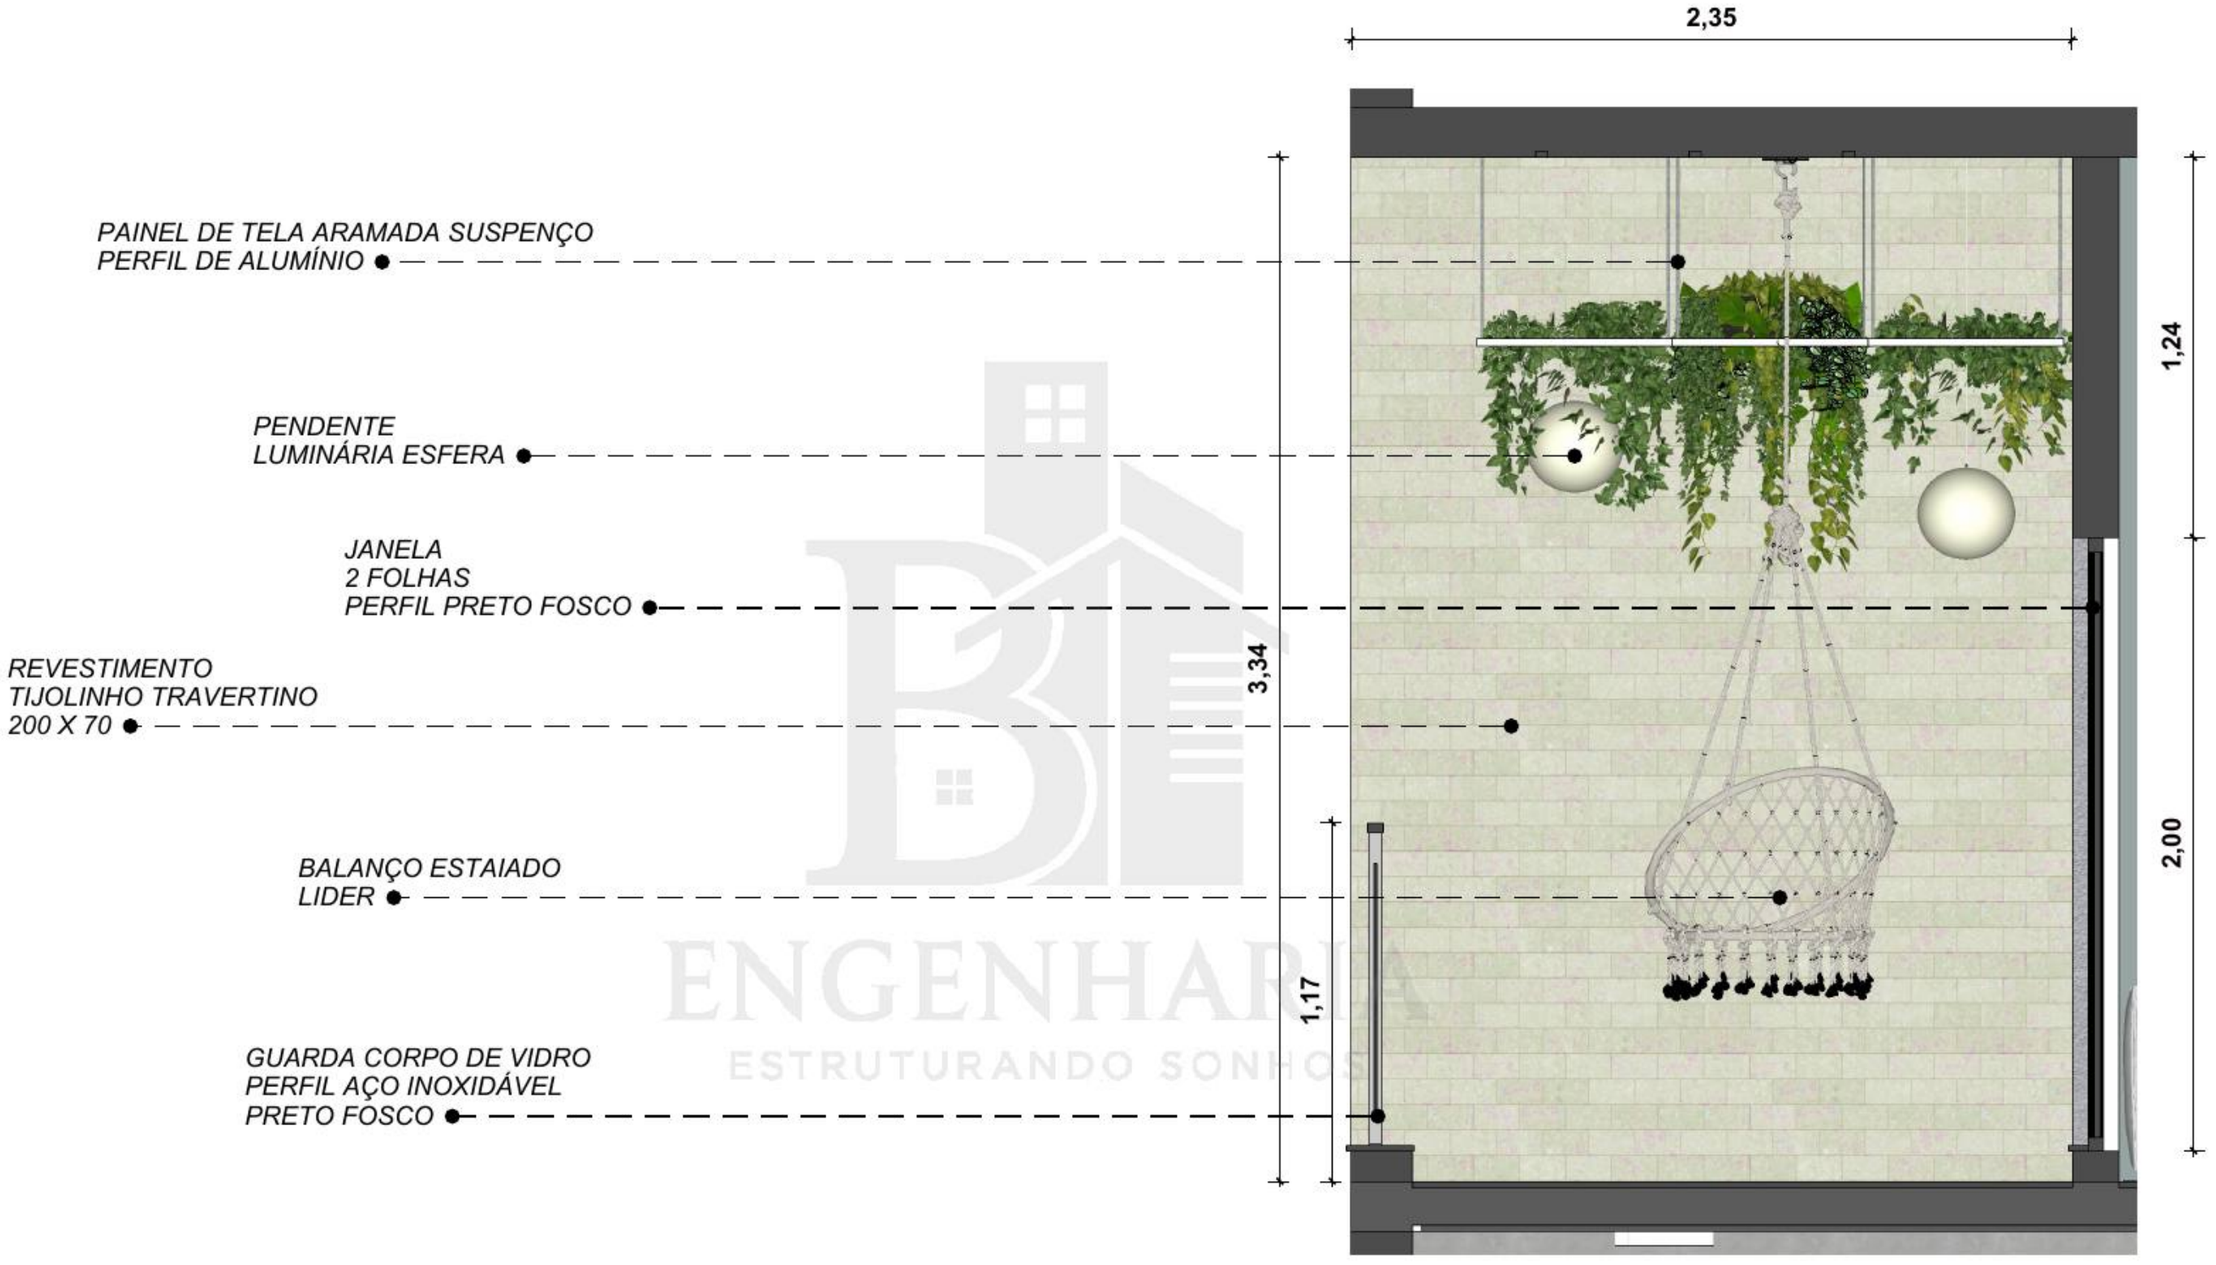

24 **VISTA C - VARANDA**
Esc: 1/20

DE ENGENHARIA
ESTRUTURANDO SONHOS

VARANDA - VISTA D

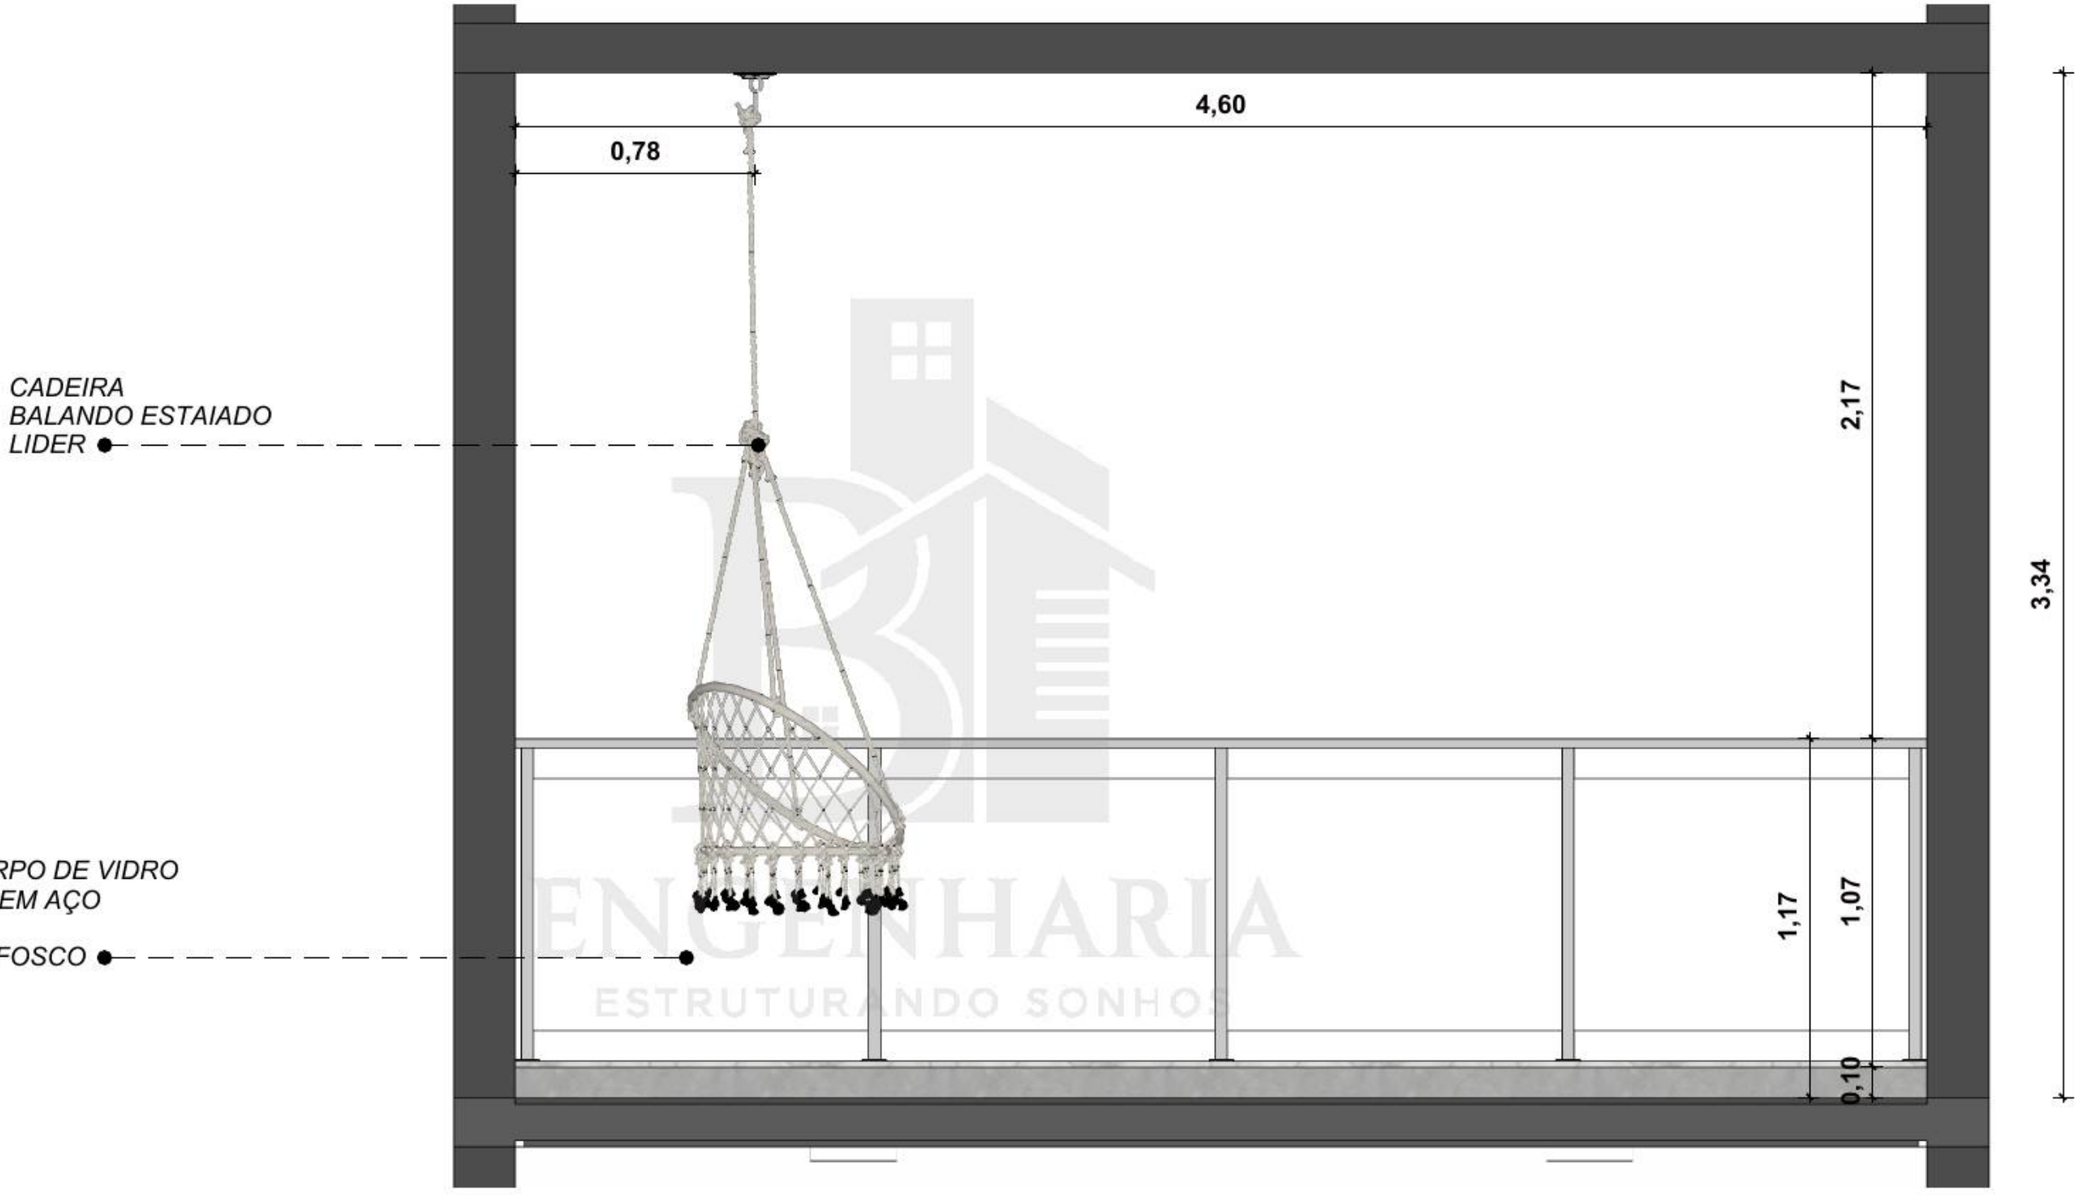

25 **VISTA D - VARANDA**
Esc: 1/20


ENGENHARIA
ESTRUTURANDO SONHOS

GARAGEM - PLANTA BAIXA

PORCELANATO CEMENTO GRIGIO
CINZA ACETINADO
60 X 120
BIANCOGRES

PORTÃO DE GARAGEM
SISTEMA BASCULANTE
COM UMA PORTA MANUAL


PORTA DE CORRER EMBUTIDA
COM RIPAS
MDF LISBOA
GUARARAPES

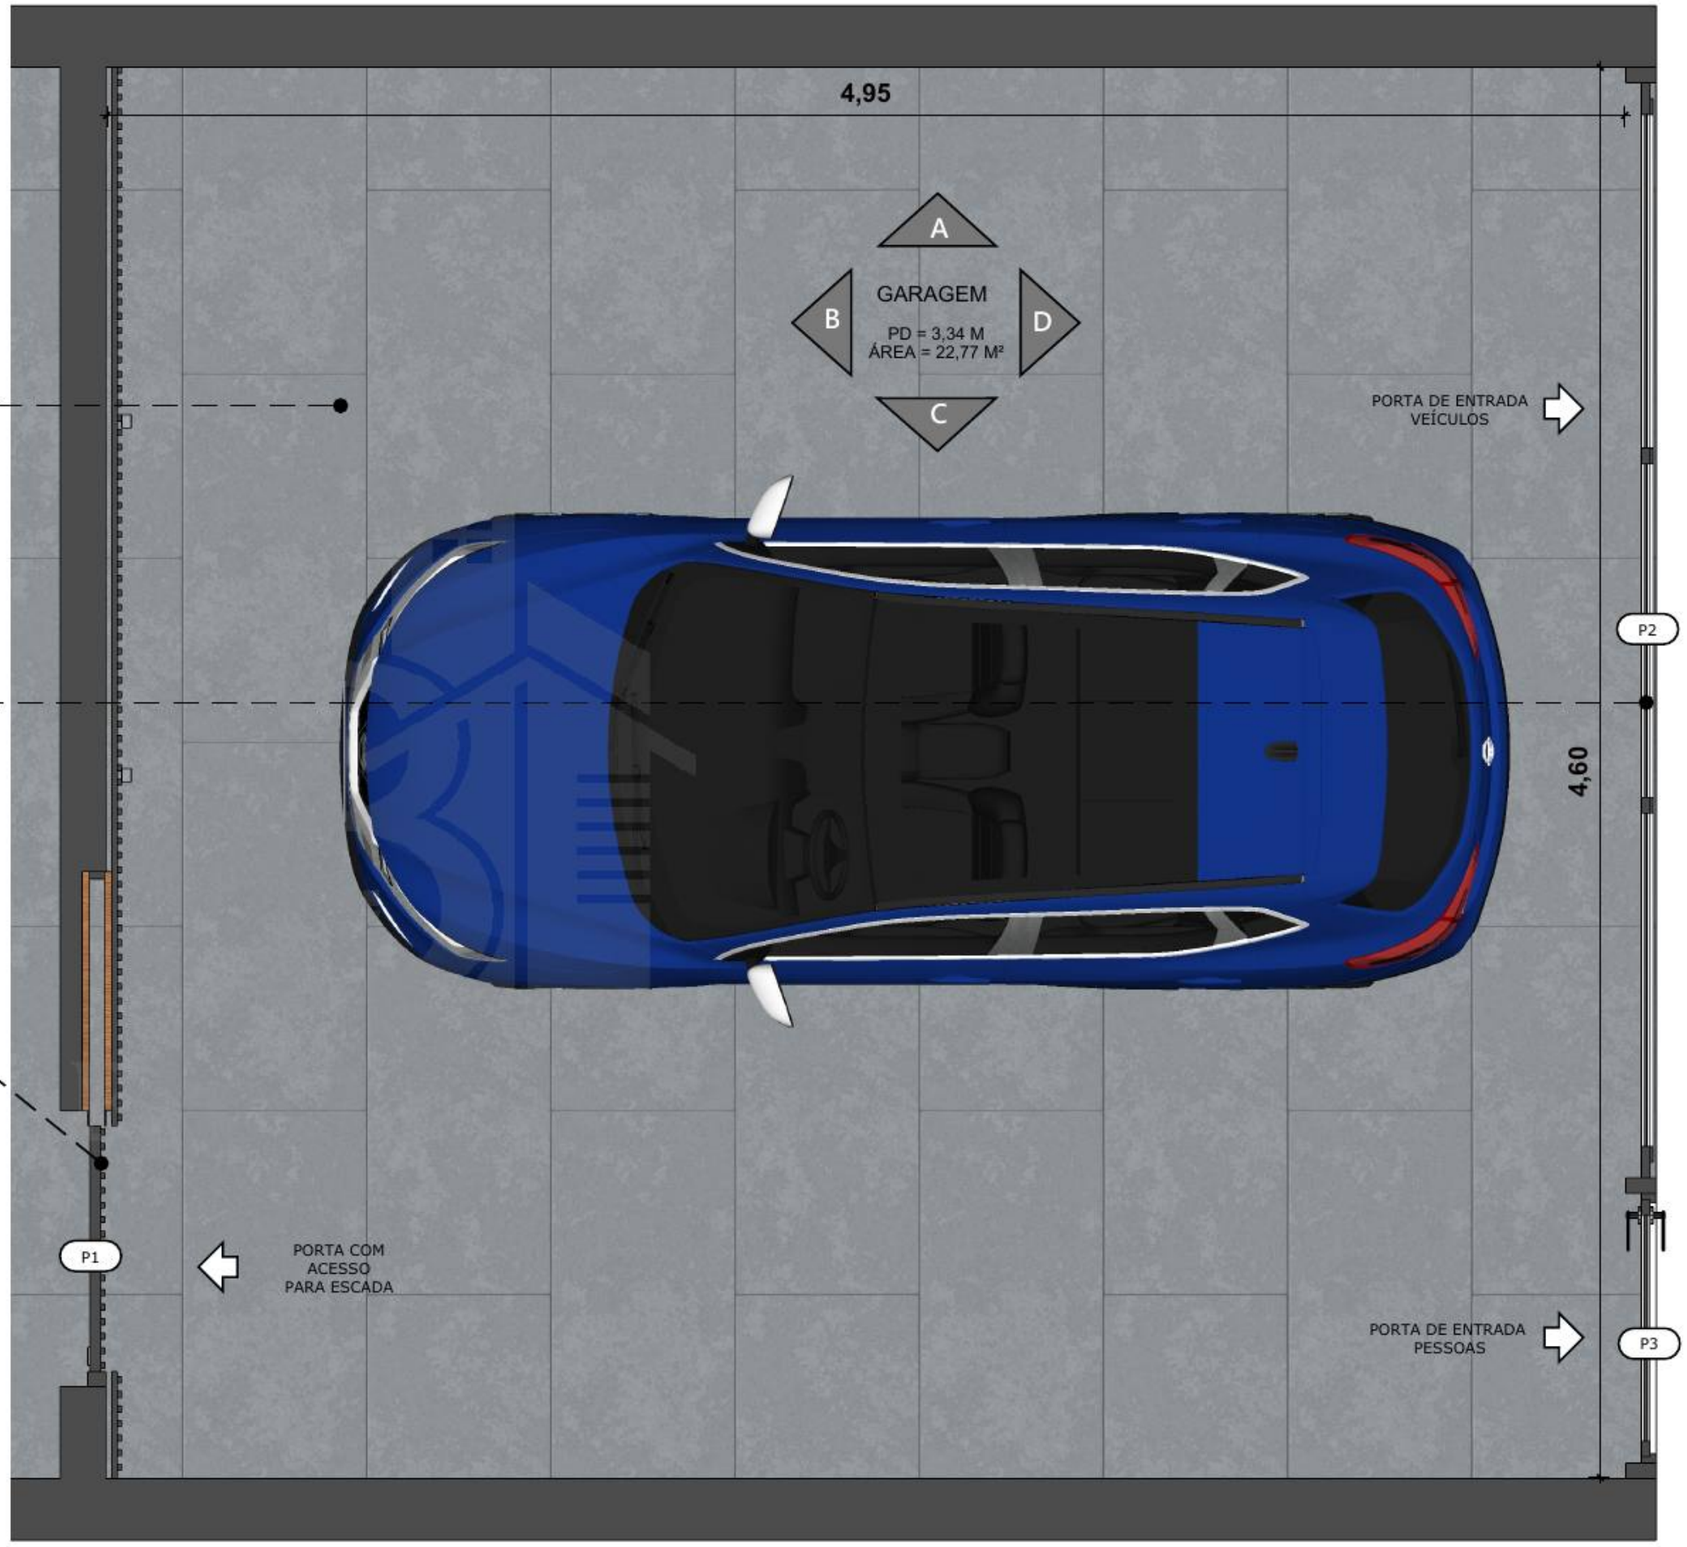

26 **PLANTA BAIXA - GARAGEM**
Esc: 1/20


PRANCHA
26/60

GARAGEM - VISTA A

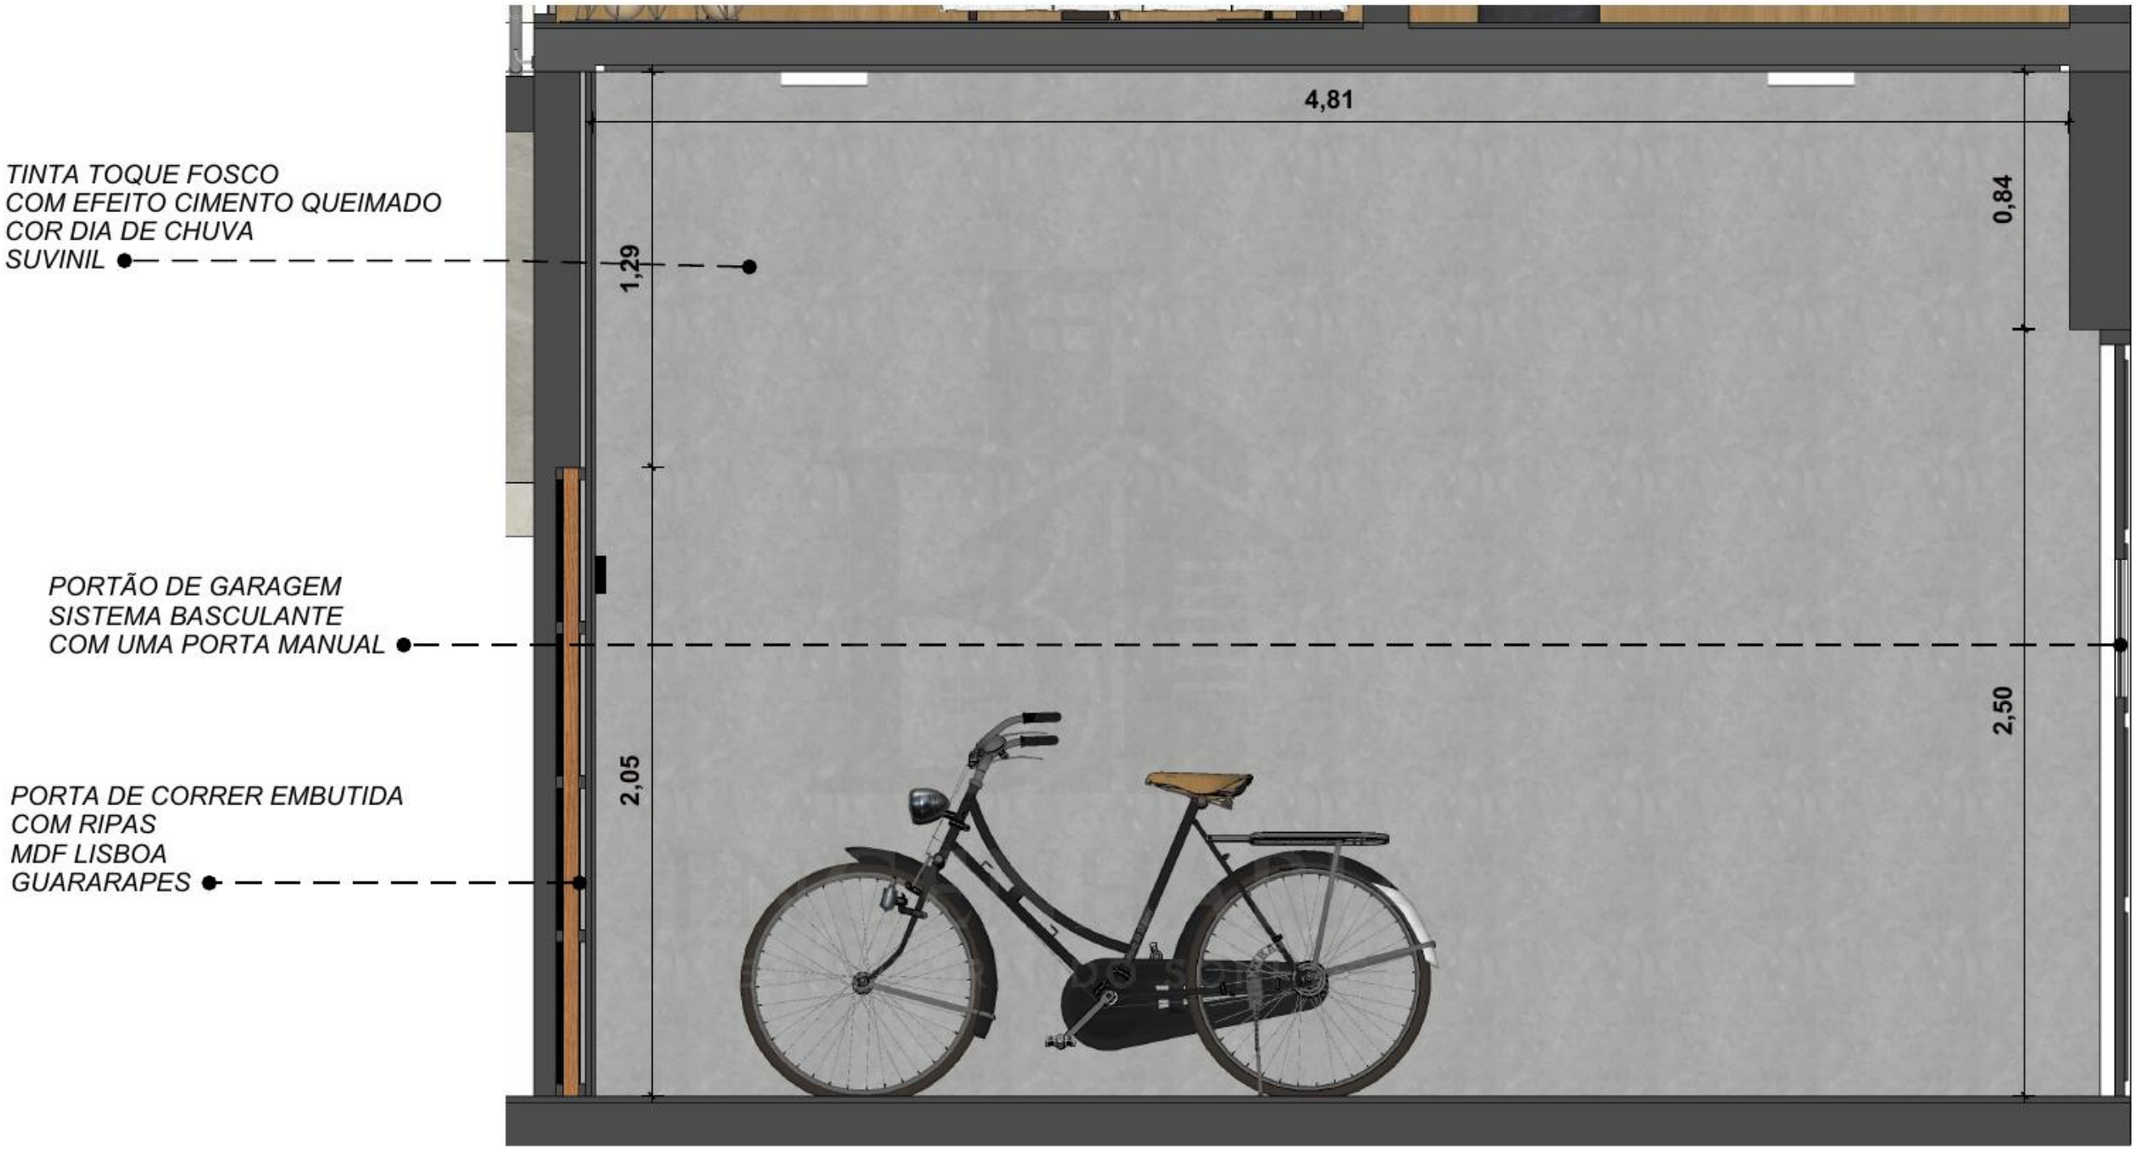

27 **VISTA A - GARAGEM**
Esc: 1/20

GARAGEM - VISTA B

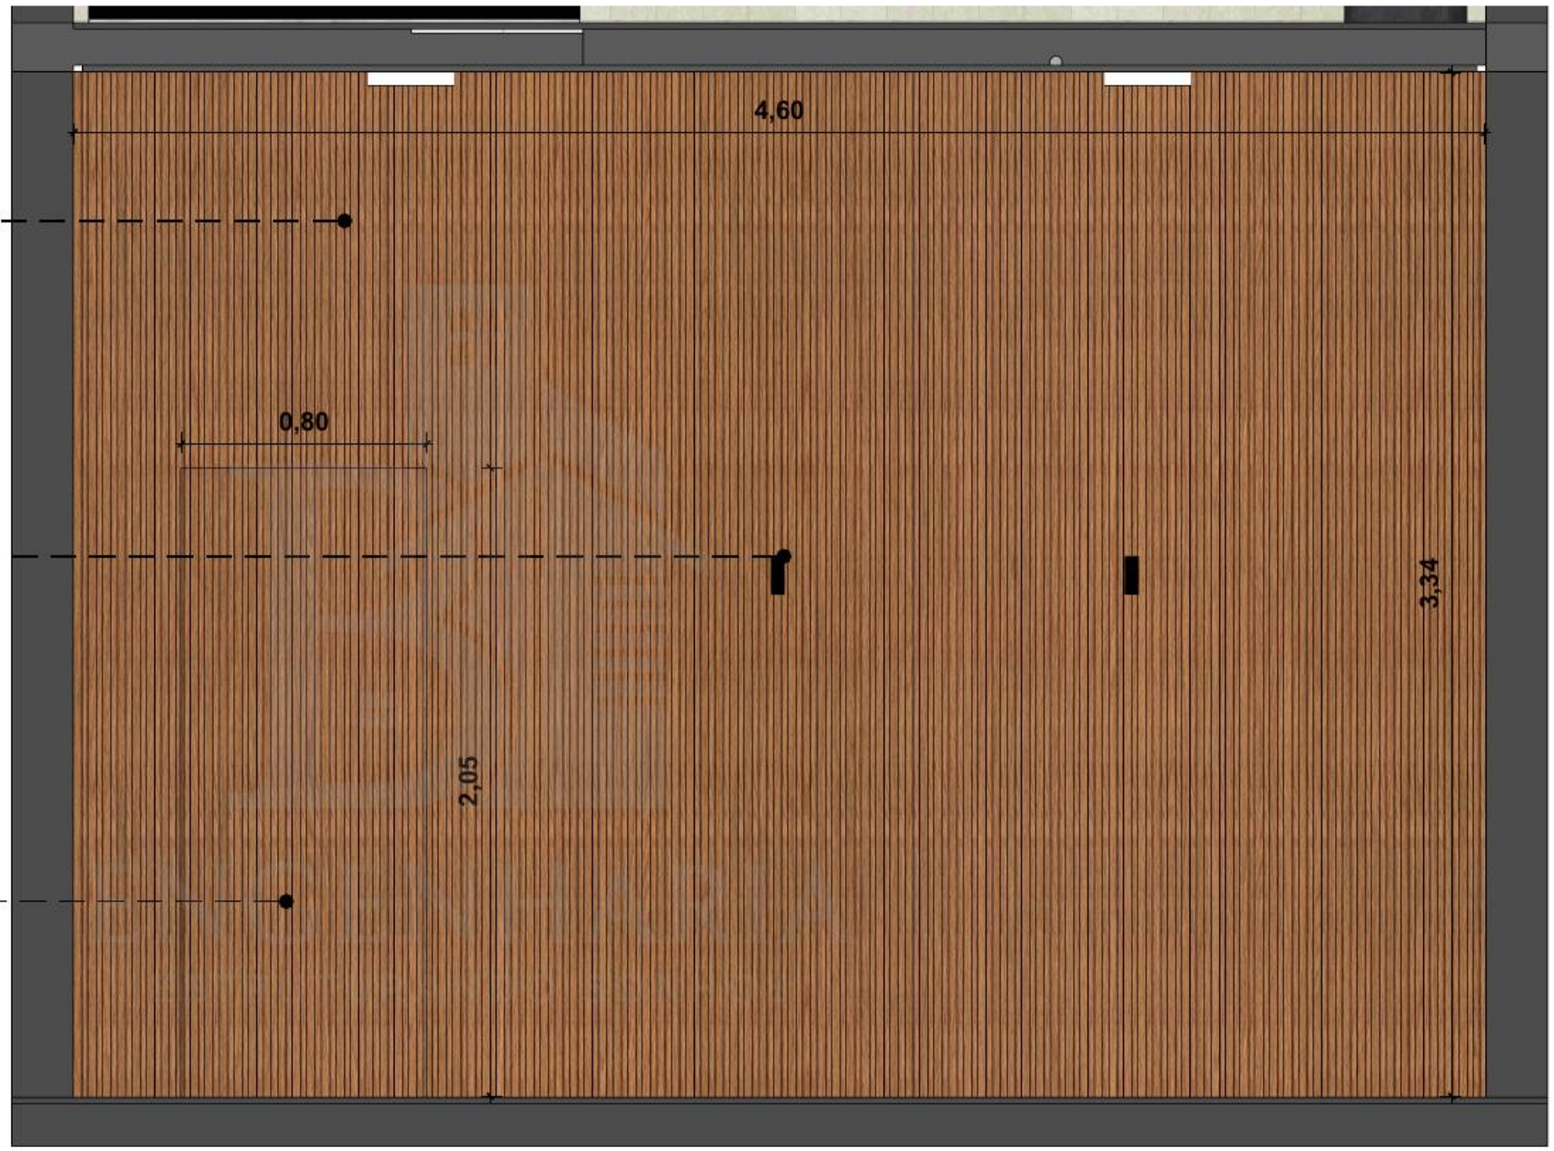


PAINEL RIPADO
MDF LISBOA
GUARARAPES

ARANDELA FOCUS SLIM
COR PRETA
GAYA

PORTA DE CORRER EMBUTIDA
COM RIPAS
MDF LISBOA
GUARARAPES

28 **VISTA B - GARAGEM**
Esc: 1/20

GARAGEM - VISTA C

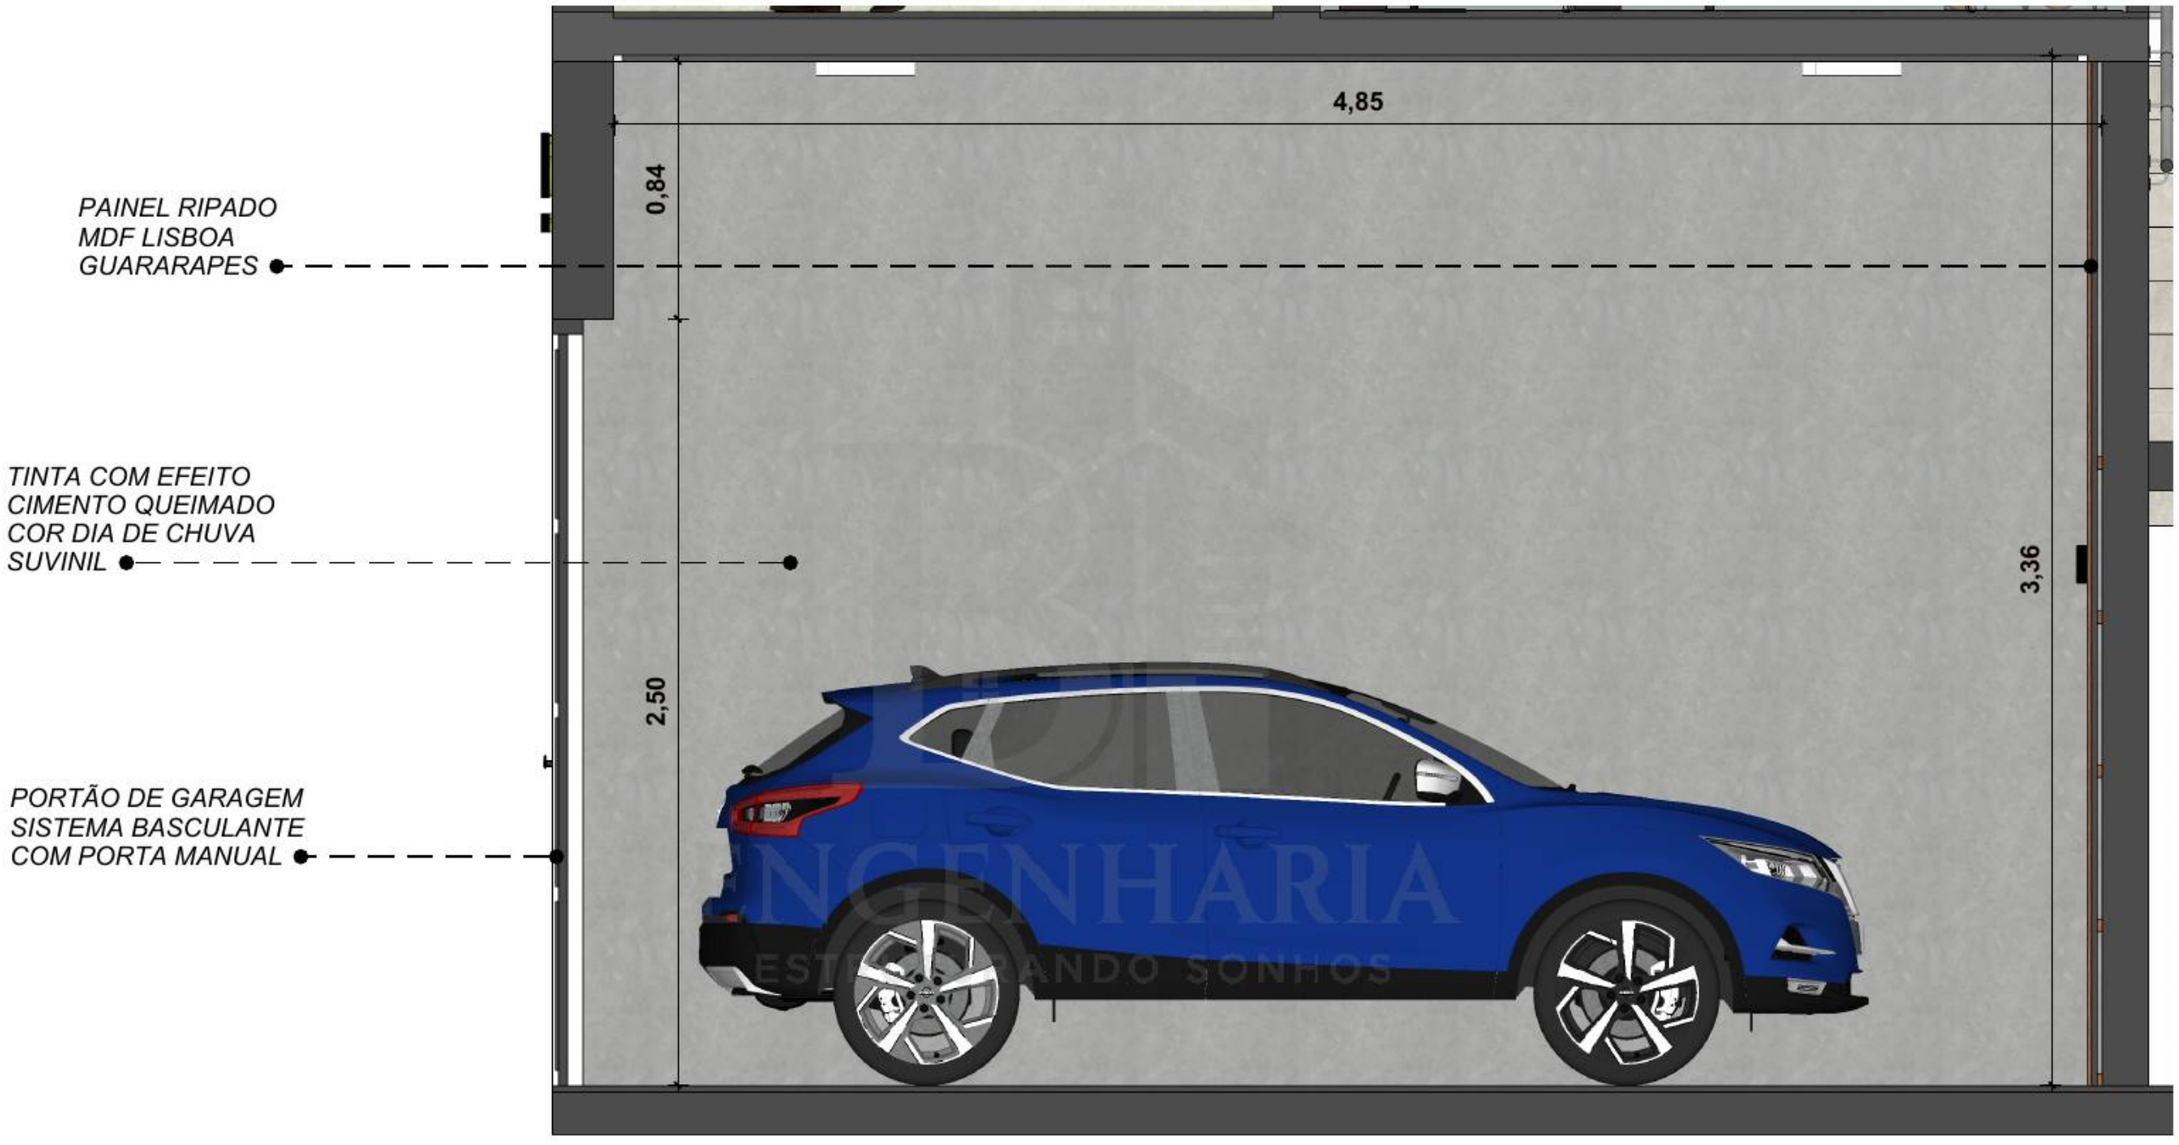


29 **VISTA C - GARAGEM**
Esc: 1/20

ENGENHARIA
ESTRUTURANDO SONHOS

GARAGEM - VISTA D

TINTA ACRÍLICA FOSCA
BRANCO NEVE
SUVINIL


PORTÃO DE GARAGEM
SISTEMA BASCULANTE
COM PORTA MANUAL

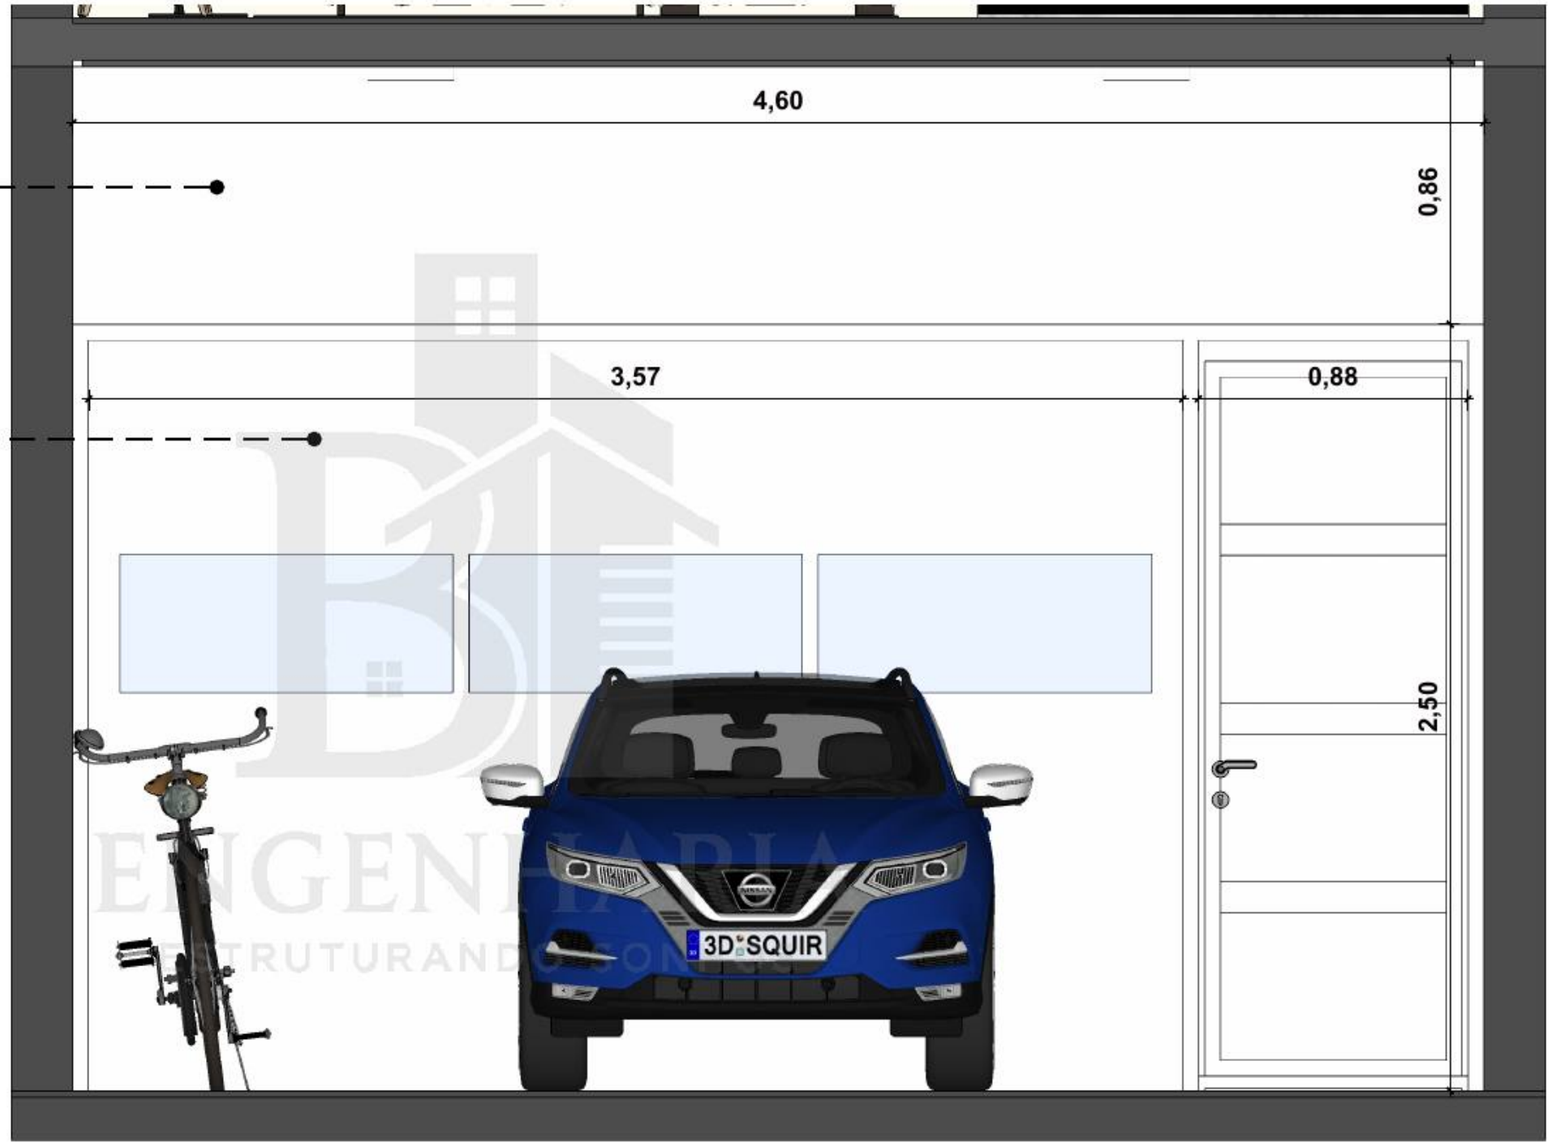

30 **VISTA D - GARAGEM**
Esc: 1/20

ENGENHARIA
ESTRUTURANDO SONHOS

GARAGEM - PLANTA BAIXA

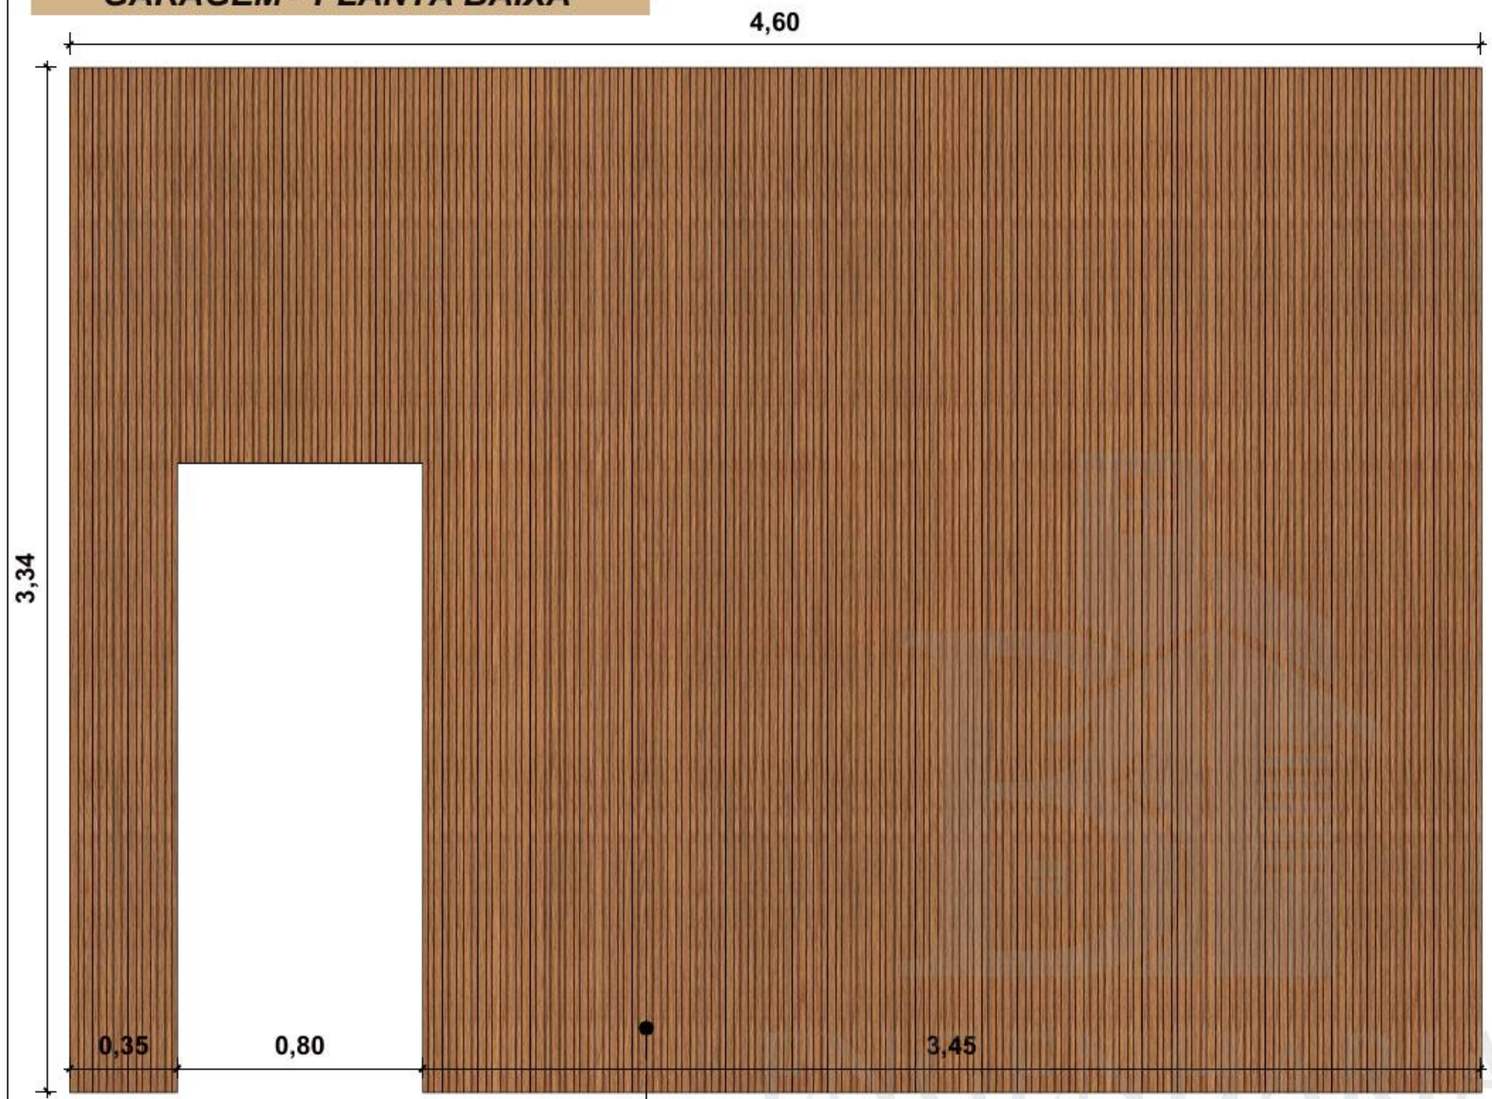


VISTA FRONTAL PAINEL


PAINEL RIPADO
MDF LISBOA
GUARARAPES




VISTA FRONTAL PORTA

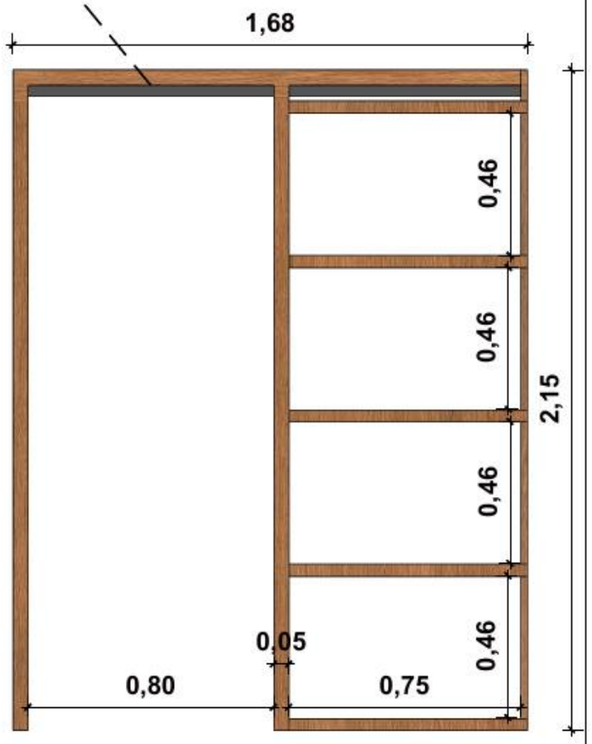

VISTA FRONTAL ESTRUTURA DA PORTA

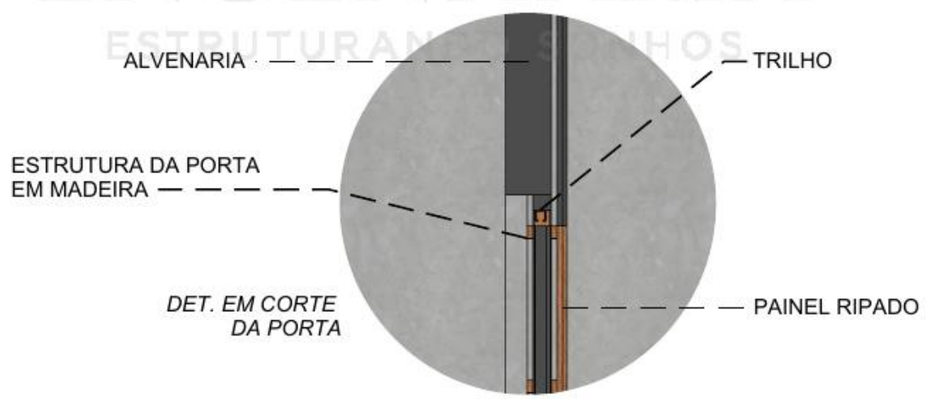

DET. EM CORTE
DA PORTA

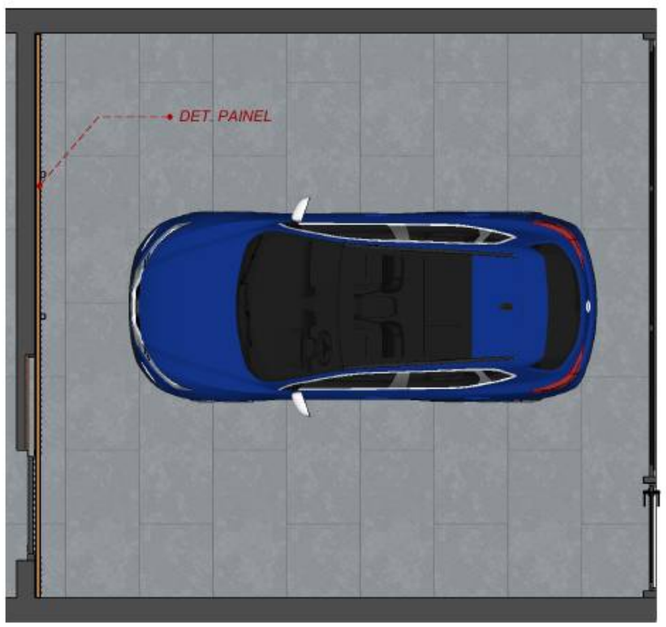

31 DET. PAINEL - GARAGEM
Esc: 1/20

ENGENHARIA
ESTRUTURAS E PROJETOS

LAVANDERIA / ÁREA GOUMET - PLANTA BAIXA

VARAL SANFONADO
ALUMÍNIO RETRÁTIL

VASO DECORATIVO

CHURRASQUEIRA
80 X 60

ACROSS DRAIN SAND
80 X 80
PORTOBELLO


CUBA LAVÍNIA 40 BL
40 X 34
TRAMONTINA

TIJOLO VAZADO
COBOGÓ

GRANITO SÃO GABRIEL

TANQUE DE ENCAIXE
RETANGULAR EM AÇO INOX
50 X 40
TRAMONTINA

PORTA DE GIRO
70 X 210
PINTURA BRANCO POLIDO

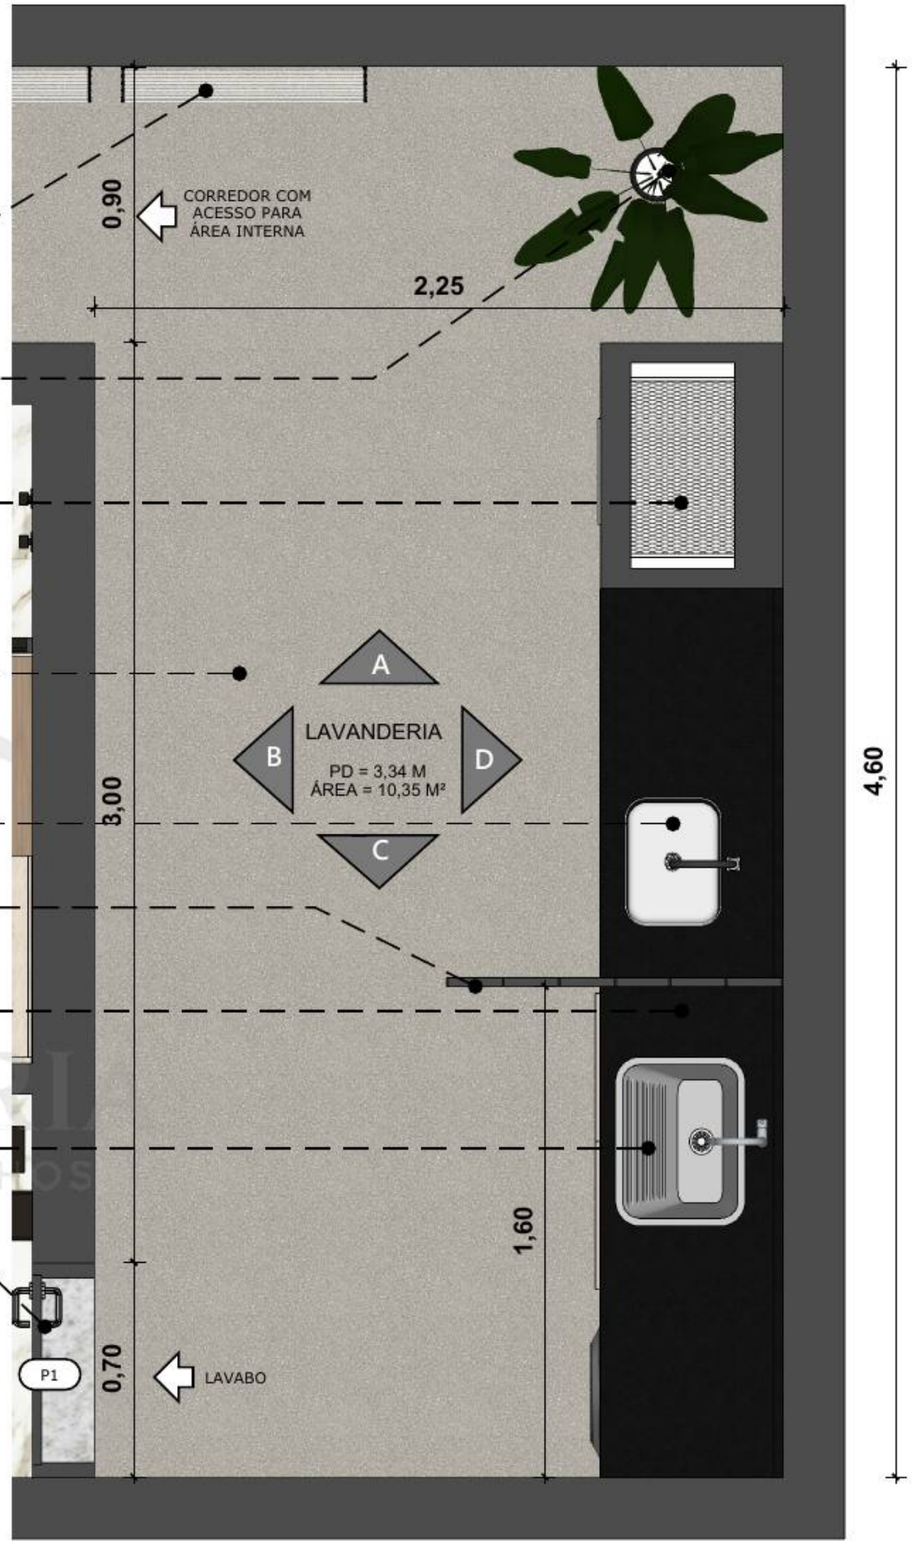

32 **PLANTA BAIXA - LAVANDERIA / ÁREA GOURMET**
Esc: 1/20

DF ENGENHARIA
ESTRUTURANDO SONHOS

PRANCHA
32/60

LAVANDERIA E ÁREA GOUMET - VISTA A

CLARABÓIA DE VIDRO
PERFIL DE ALUMÍNIO
T INVERTIDO

ALÇAPÃO
80 X 80

CHURRASQUEIRA
80 X 60

TINTA TOQUE FOSCO
COM EFEITO CIMENTO QUEIMADO
COR DIA DE CHUVA
SUVINIL

TIJOLO VAZADO
COBOGÓ

VARAL SANFONADO
ALUMÍNIO RETRÁTIL

PORTA DE GIRO
PINTURA BRANCO POLIDO


MDF LISBOA
GUARARAPES



33 **VISTA A - LAVANDERIA / ÁREA GOURMET**
Esc: 1/20

ENGENHARIA
ESTRUTURANDO SONHOS

LAVANDERIA E ÁREA GOUMET - VISTA B

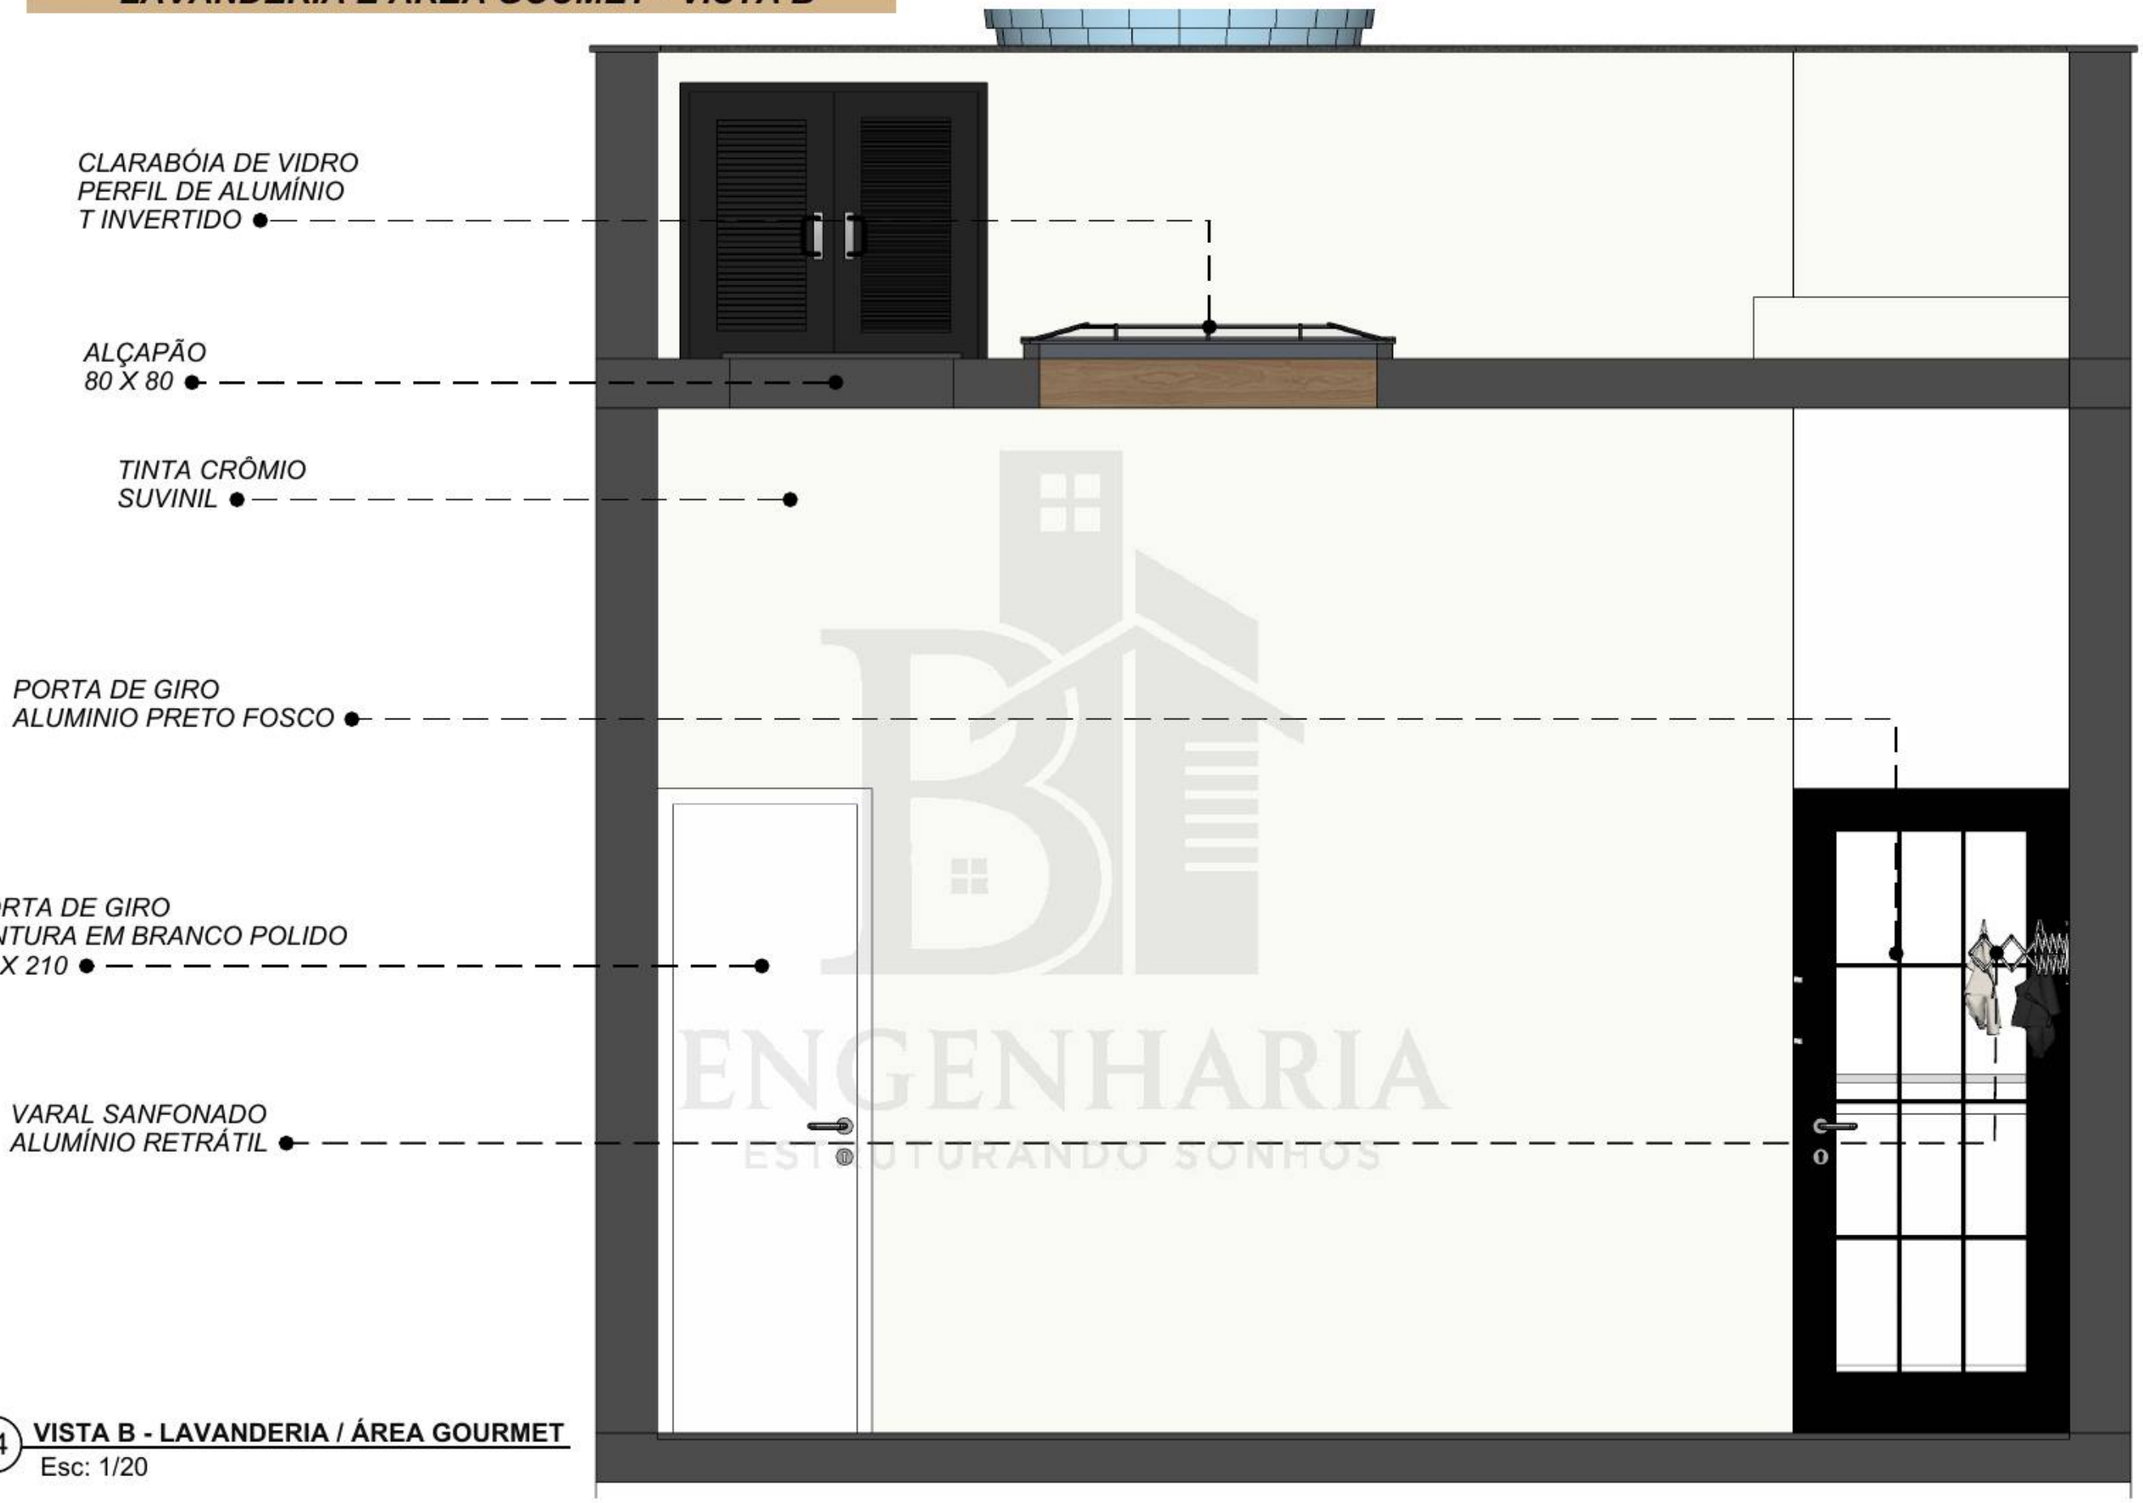

34 **VISTA B - LAVANDERIA / ÁREA GOURMET**
Esc: 1/20

ENGENHARIA
ESTRUTURANDO SONHOS

LAVANDERIA E ÁREA GOUMET - VISTA C

TINTA CRÔMIO
SUVINIL


ALÇAPÃO
80 X 80

MC CAMINHO CURVÊ MIX NAT
30 X 30
PORTINARI

MDF LISBOA
GUARARAPES

PORTA DE GIRO
TINTURA EM BRANCO POLIDO
70 X 210

LAVA E SECA
10 KG

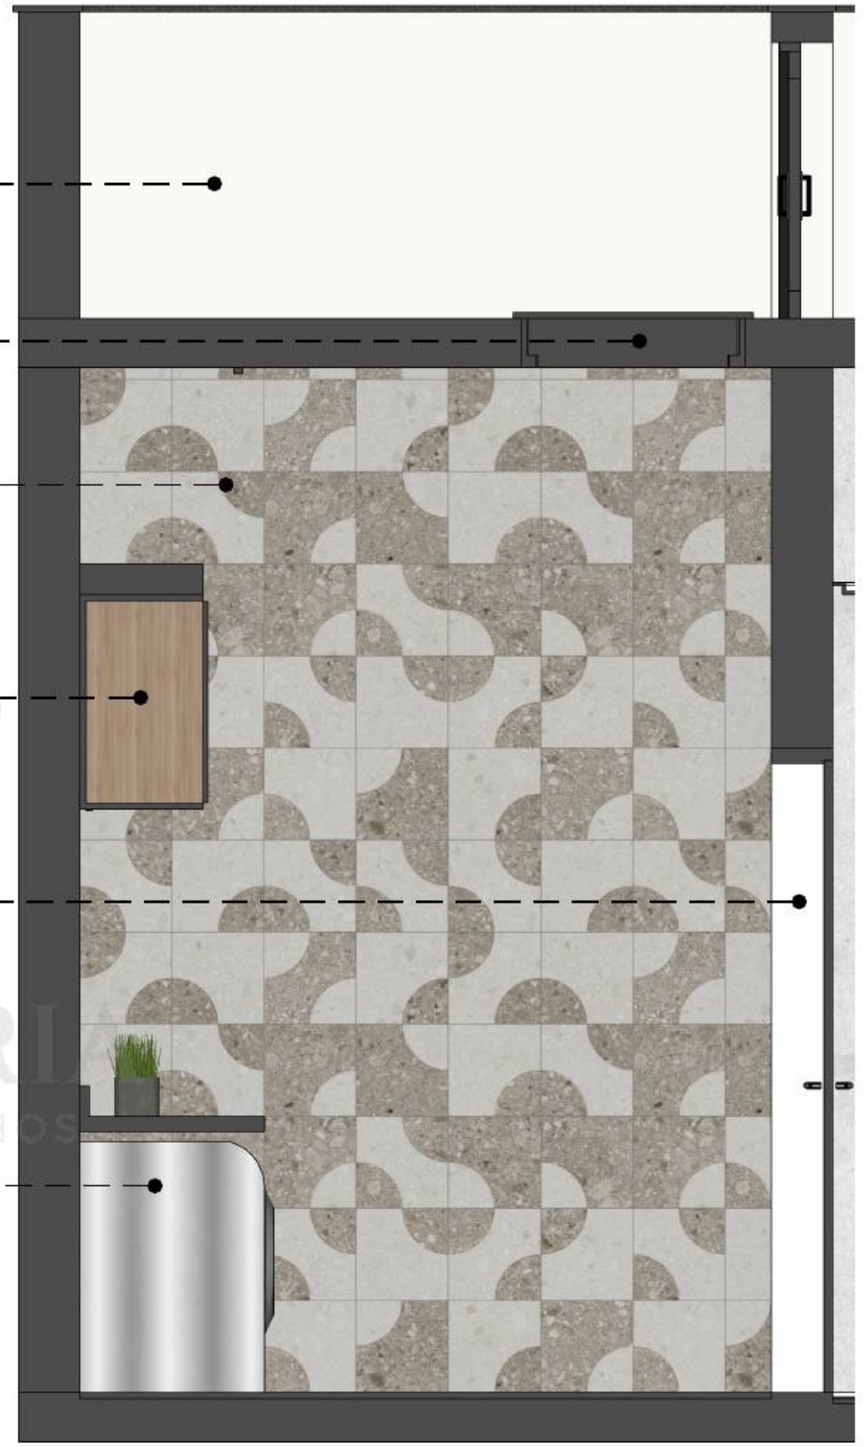

35 **VISTA C - LAVANDERIA / ÁREA GOURMET**
Esc: 1/20


ENGENHARIA
ESTRUTURANDO SONHOS

LAVANDERIA E ÁREA GOUMET - VISTA D




36 **VISTA D - LAVANDERIA / ÁREA GOURMET**
Esc: 1/20


LAVANDERIA E ÁREA GOUMET - DETALHAMENTO

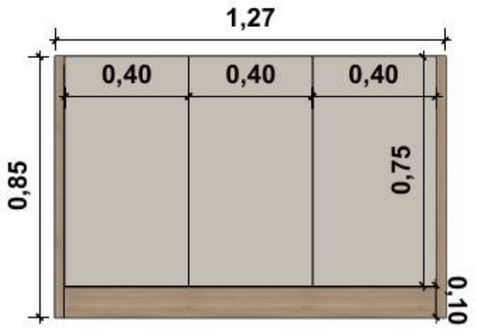


VISTA FRONTAL - ARM. 01

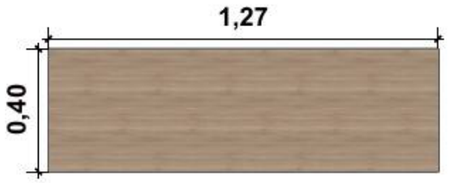


VISTA EM PLANTA - PRATELEIRA

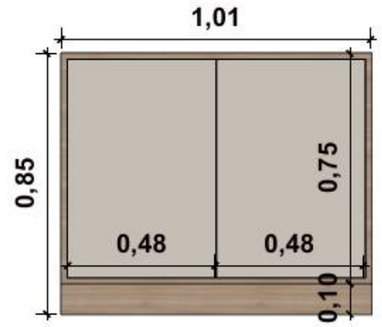

VISTA FRONTAL - ARM. 02

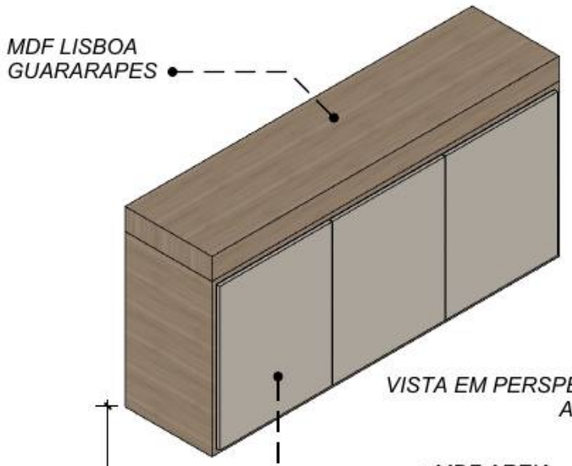

VISTA EM PERSPECTIVA
ARM. 03

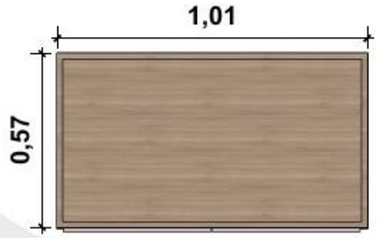


VISTA EM PLANTA - ARM. 02




VISTA EM PLANTA - ARM. 01




VISTA EM PERSPECTIVA
PRATELEIRA

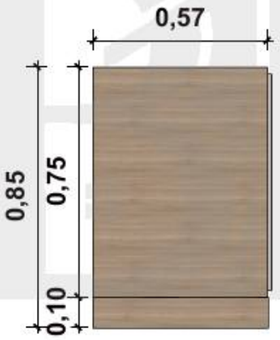


VISTA LATERAL
ARM. 02

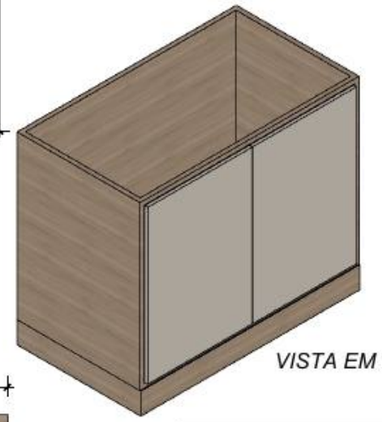


VISTA EM PERSPECTIVA
ARM. 02

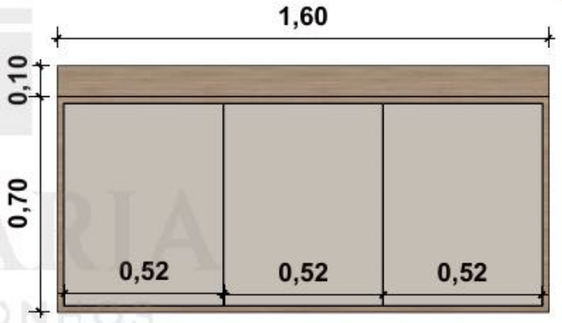


VISTA FRONTAL - ARM. 03

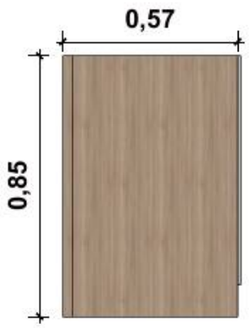

VISTA LATERAL - ARM. 01

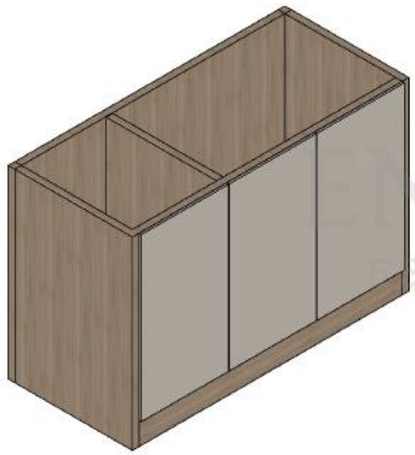


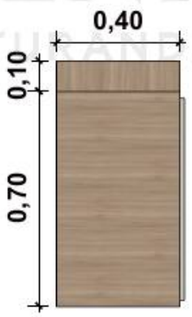

VISTA LATERAL
ARM 03



VISTA EM PLANTA - ARM. 03

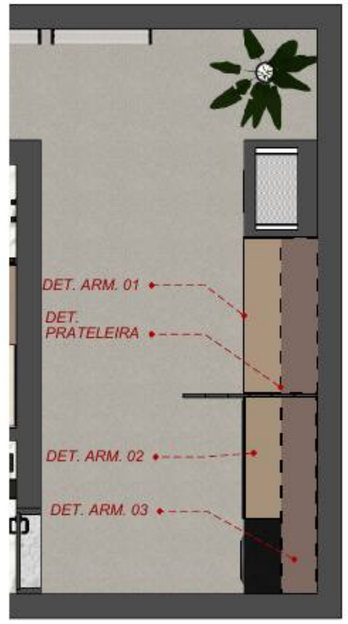

37 **DETALHAMENTO - LAVANDERIA / ÁREA GOURMET**
Esc: 1/20


ENGENHARIA
ESTRUTURANDO SONHOS

PRANCHA
37/60

LAVABO - PLANTA BAIXA / VISTA A




38 **PLANTA BAIXA - LAVABO**
Esc: 1/20

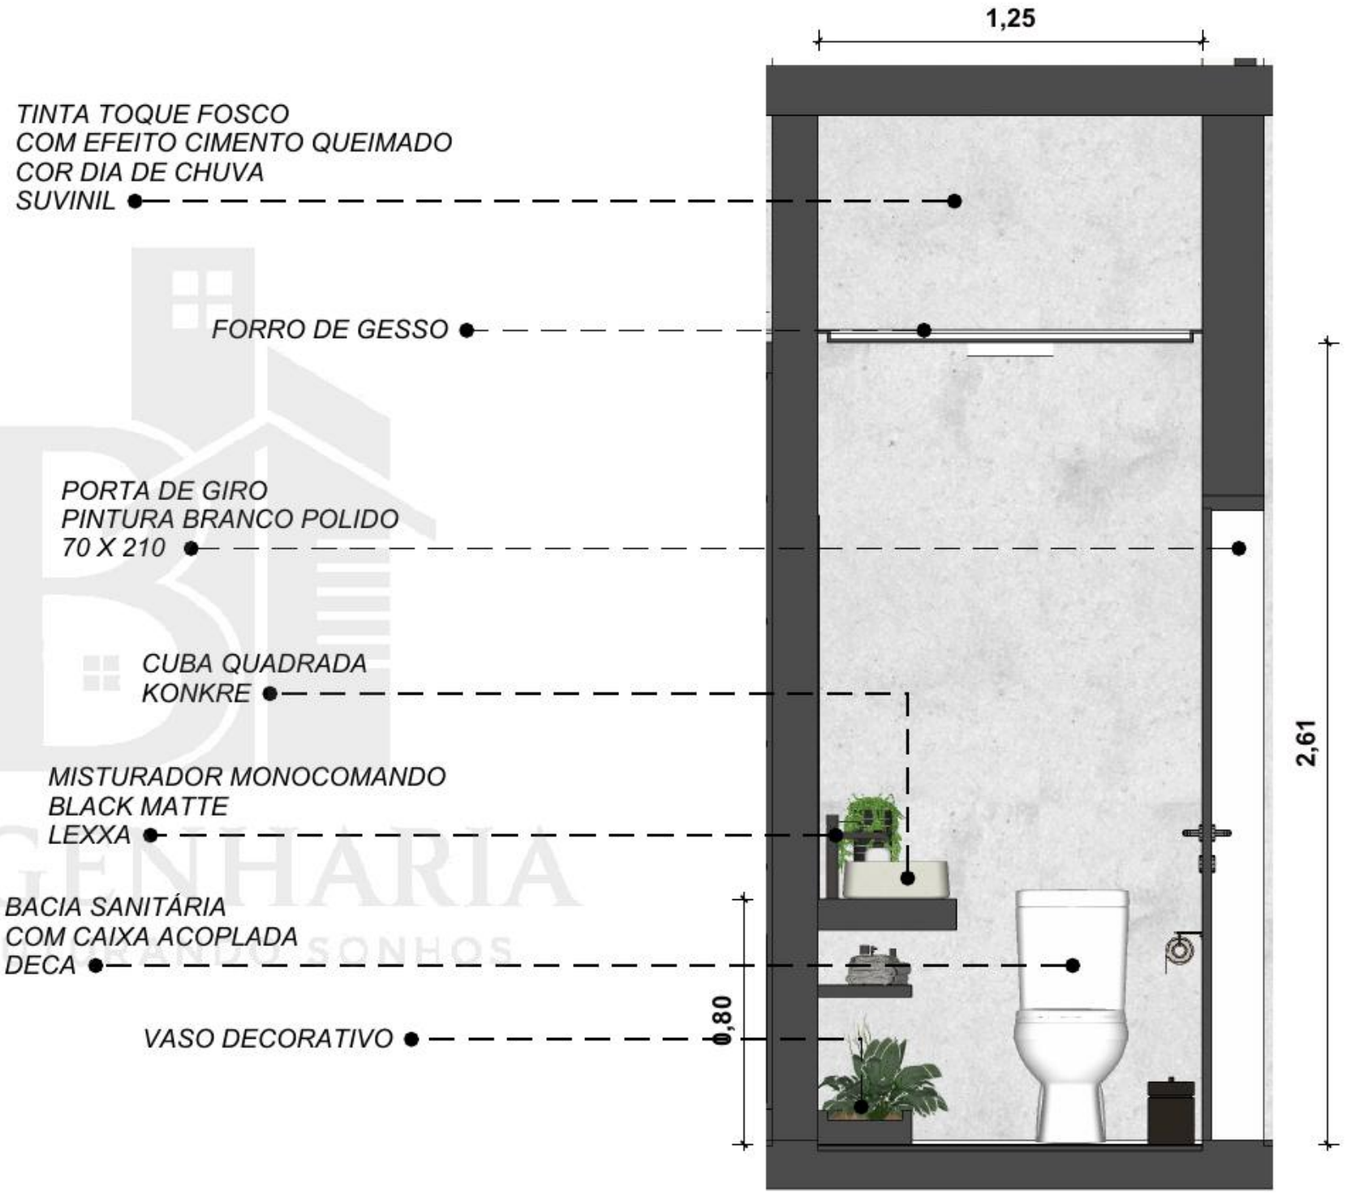


39 **VISTA A - LAVABO**
Esc: 1/20

ENGENHARIA
ESTRUTURA DE SONHOS

LAVABO - VISTAS B,C

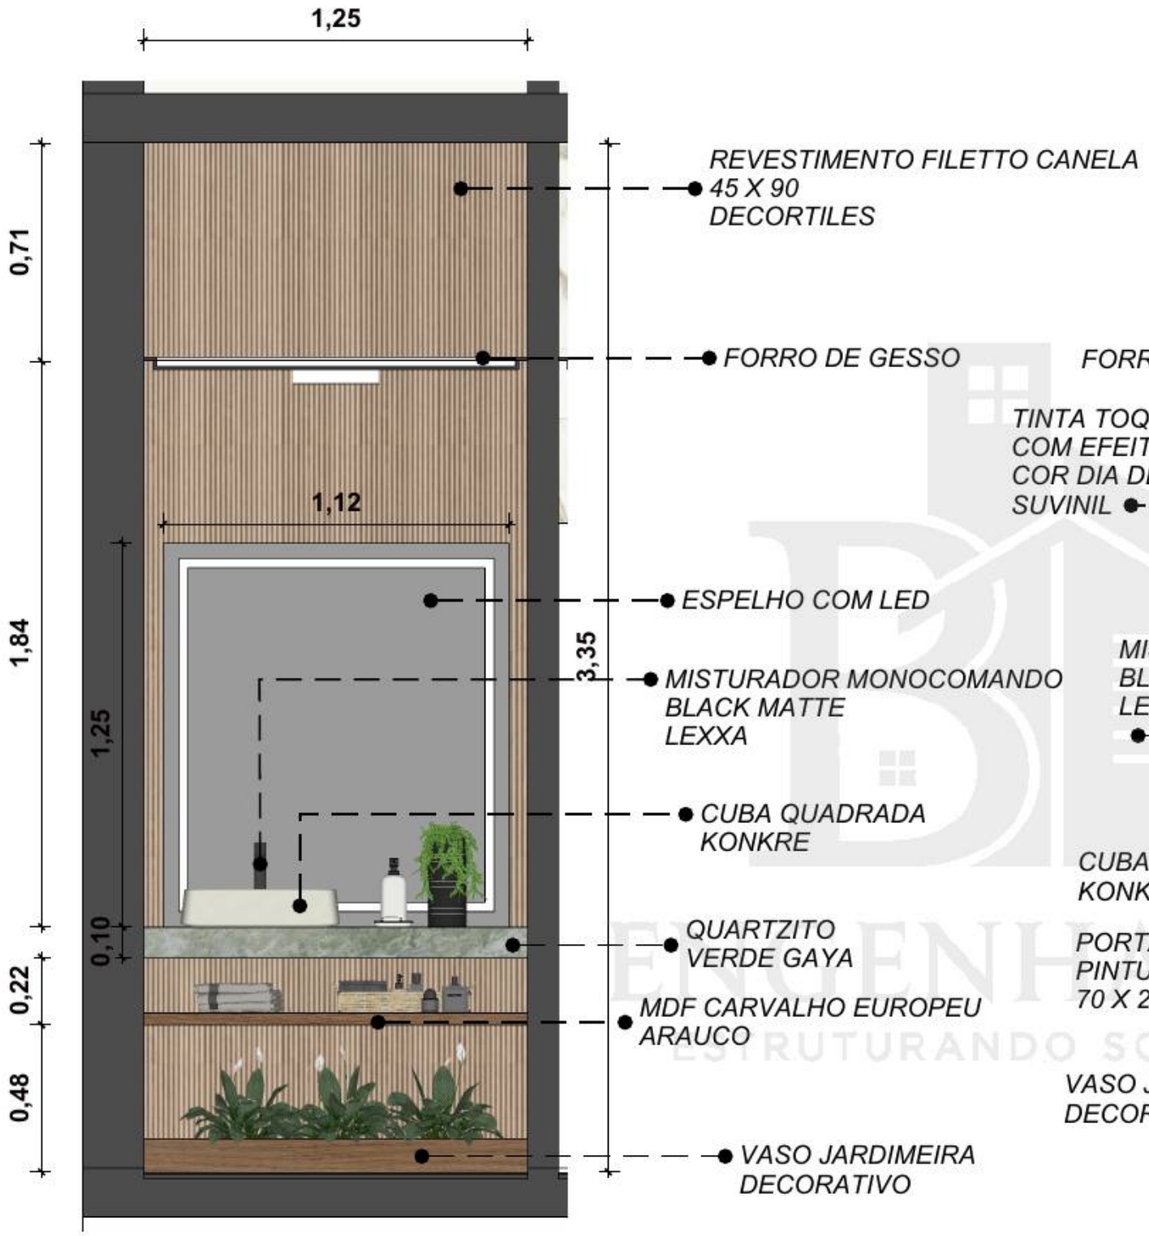


40 **VISTA B - LAVABO**
Esc: 1/20

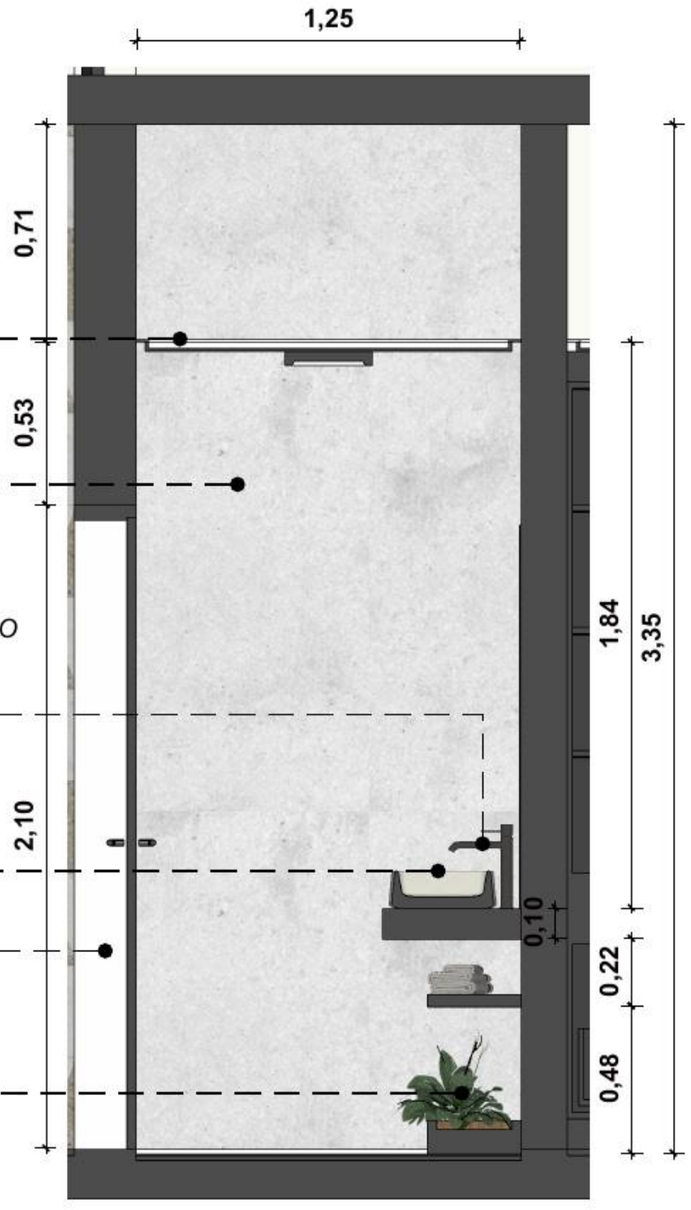


41 **VISTA C - LAVABO**
Esc: 1/20

ENGENHARIA
ESTRUTURANDO SONHOS

LAVABO - VISTAS D / DETALHAMENTO

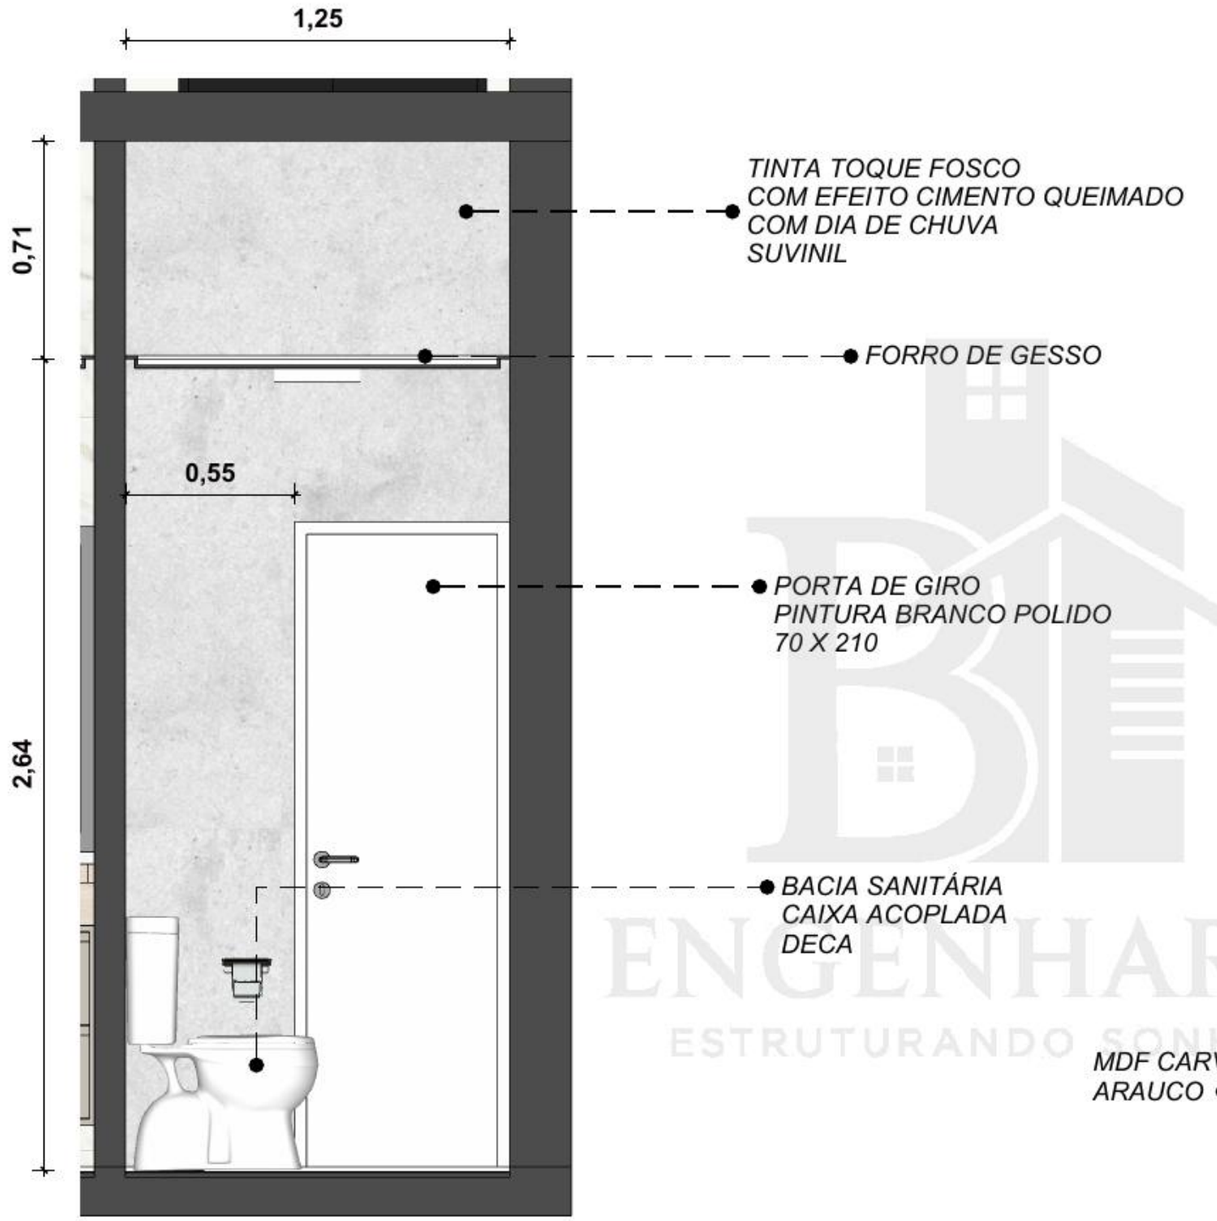


42 **VISTA D - LAVABO**
Esc: 1/20

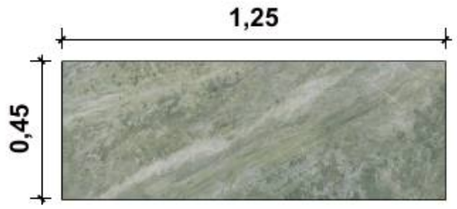

VISTA EM PLANTA - BANCADA



VISTA EM PLANTA - PRATELEIRA

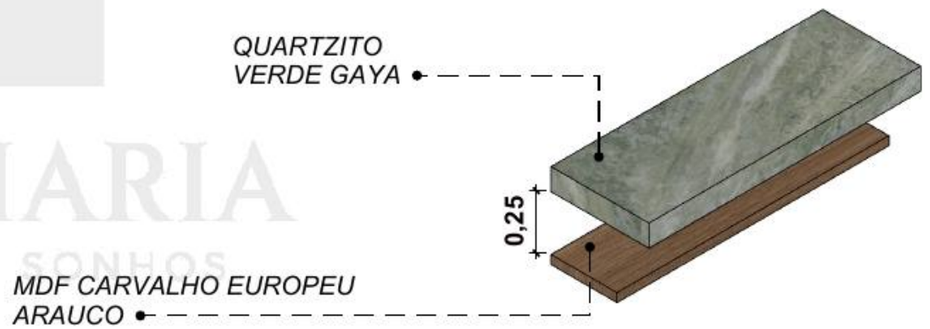


VISTA EM PERSPECTIVA
BANCADA E PRATELEIRA

43 **DETALHAMENTO- LAVABO**
Esc: 1/20

ENGENHARIA
ESTRUTURANDO SONHOS


SUÍTE - PLANTA BAIXA

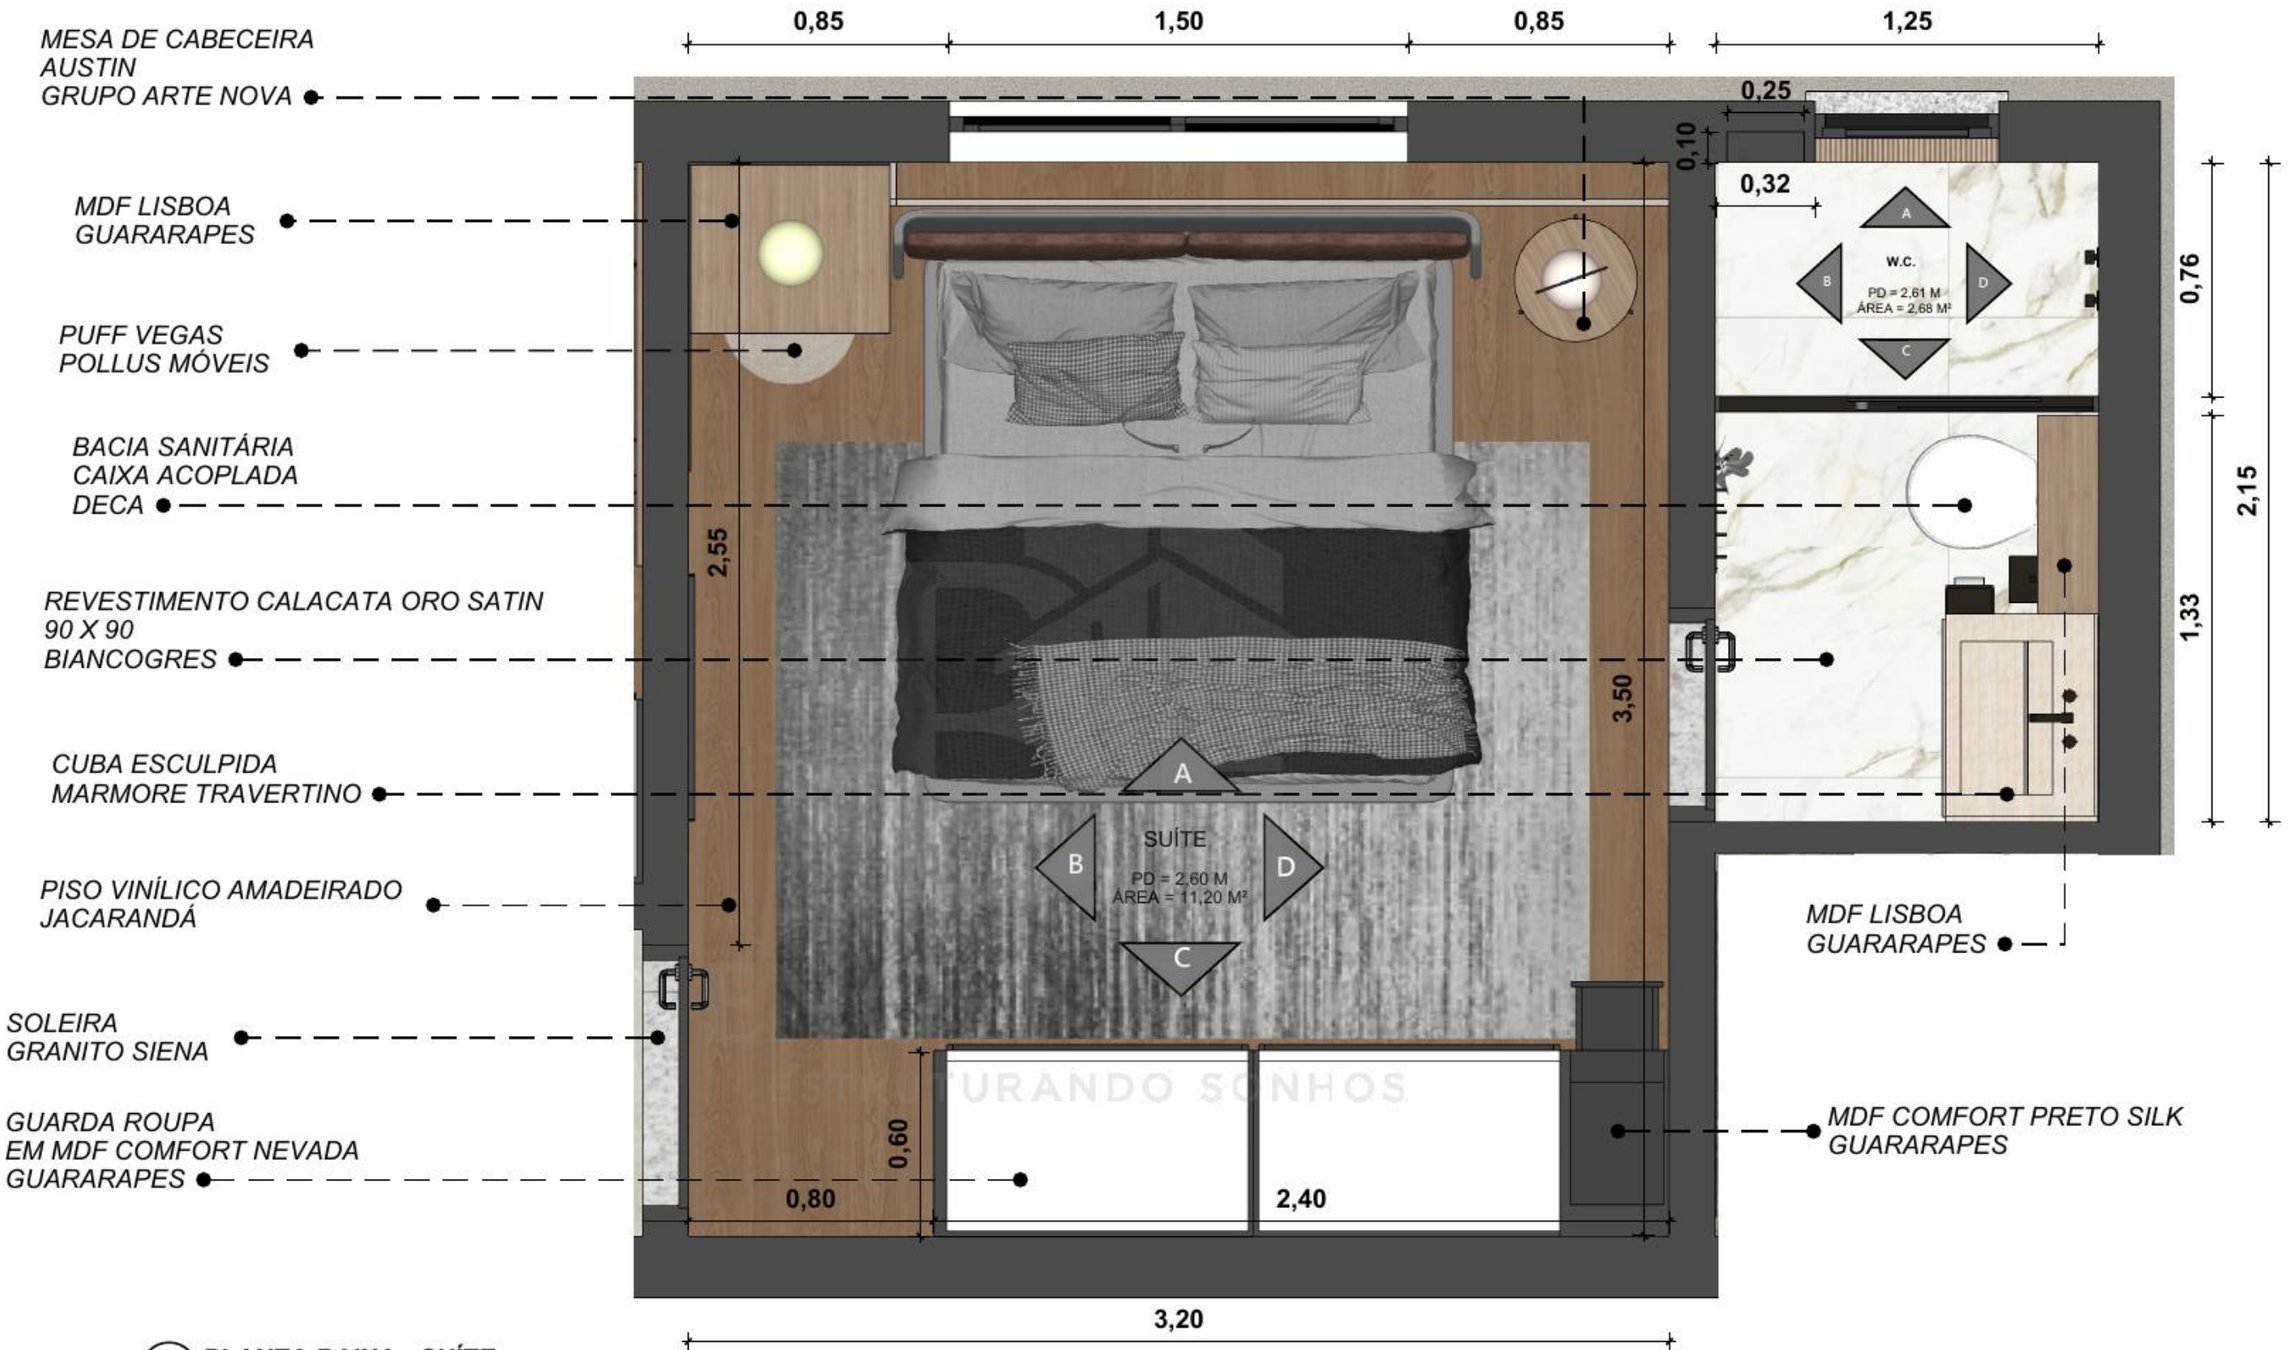

44 **PLANTA BAIXA - SUÍTE**
Esc: 1/20


CRIANDO E MATURANDO SONHOS

SUÍTE - VISTA A

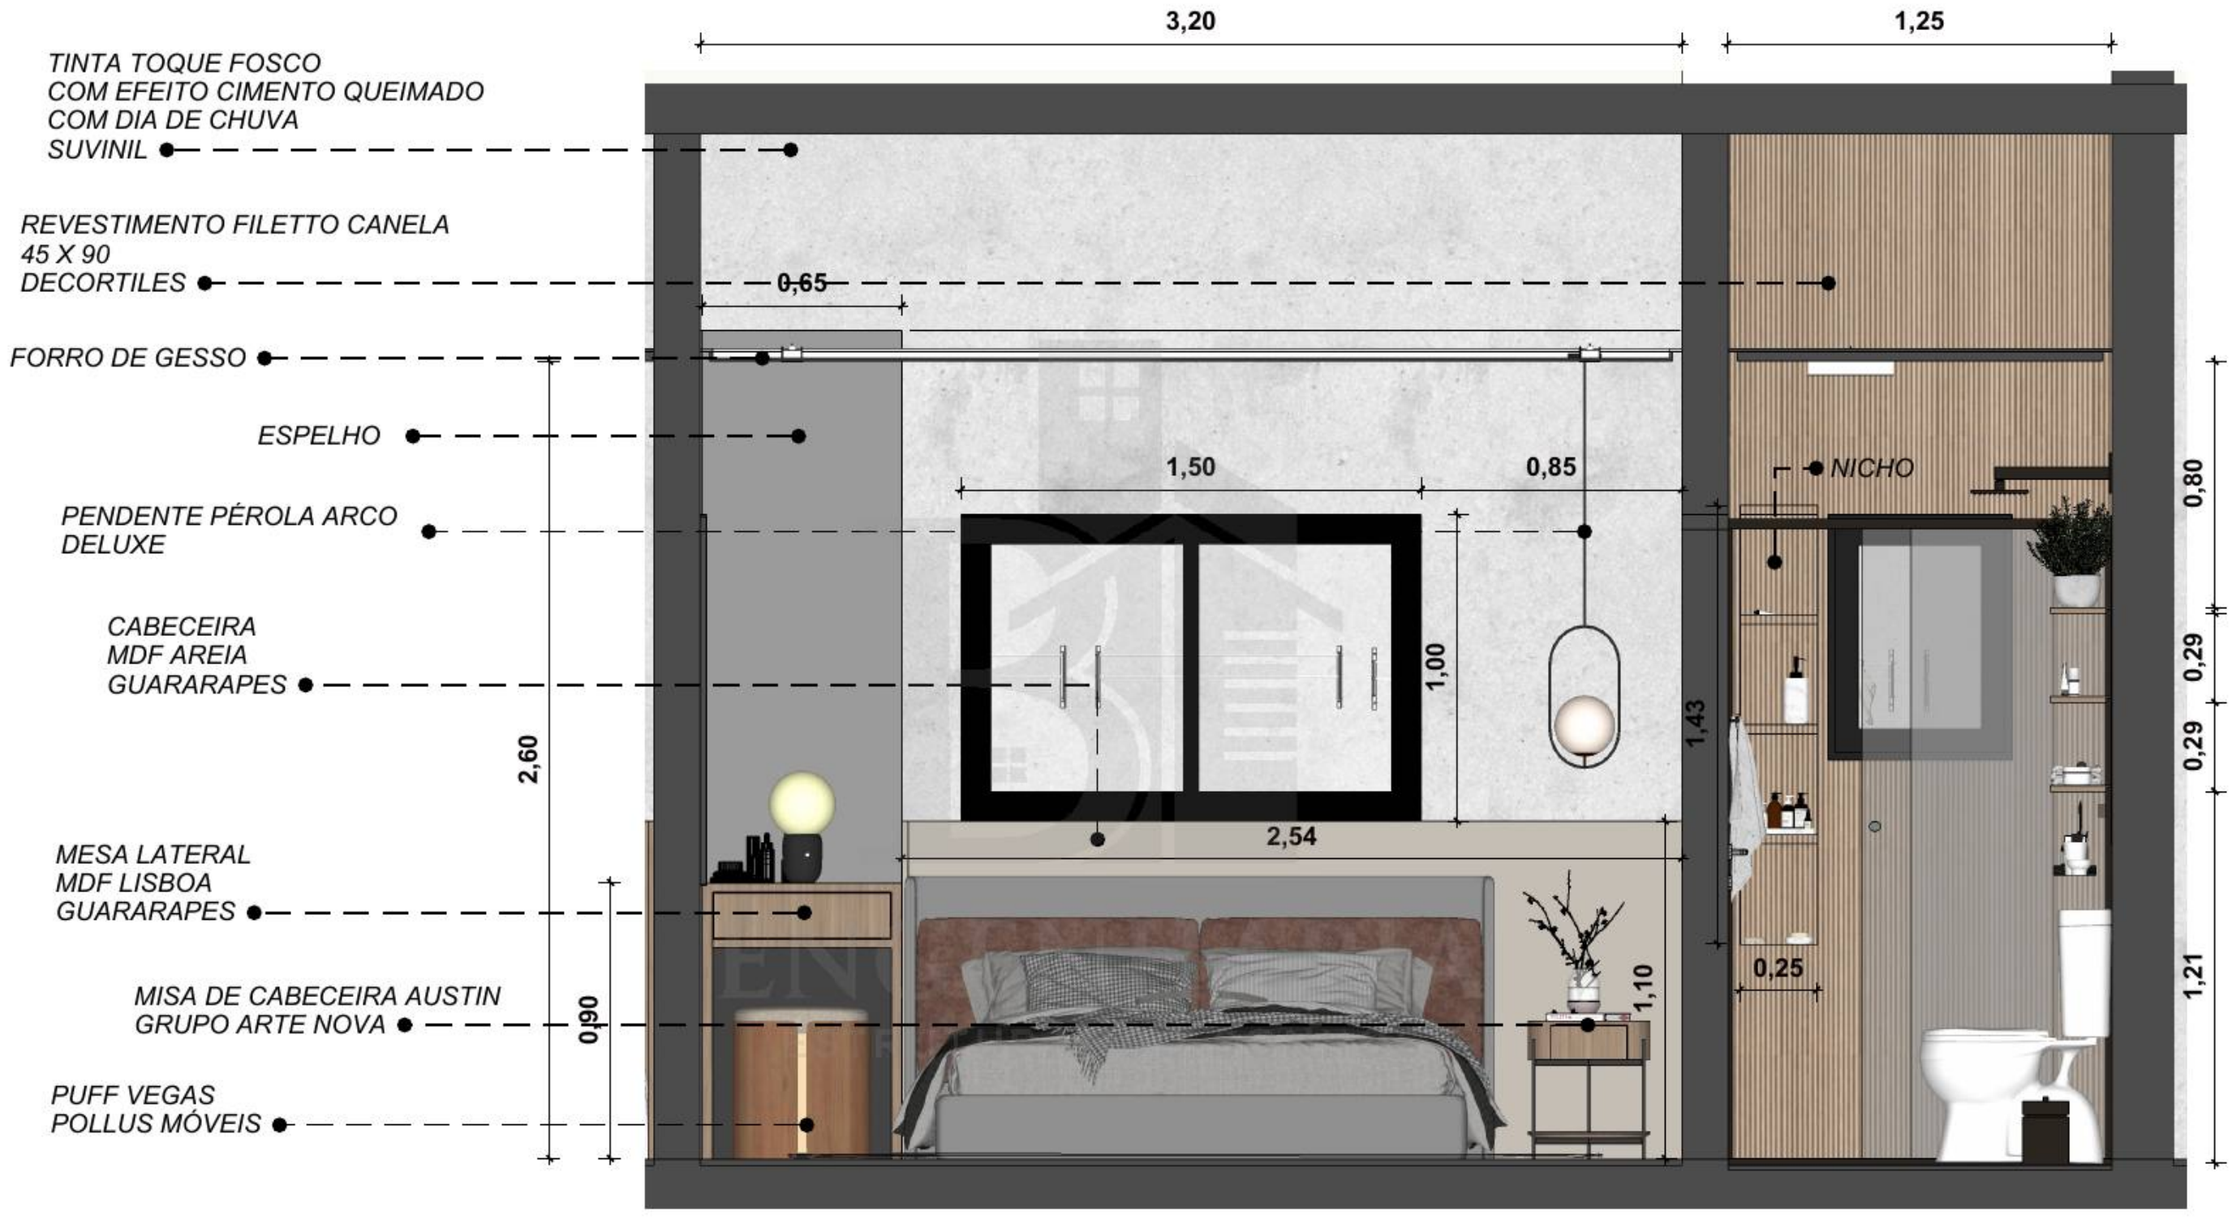

45 **VISTA A - SUÍTE**
Esc: 1/20


SUÍTE - VISTA B

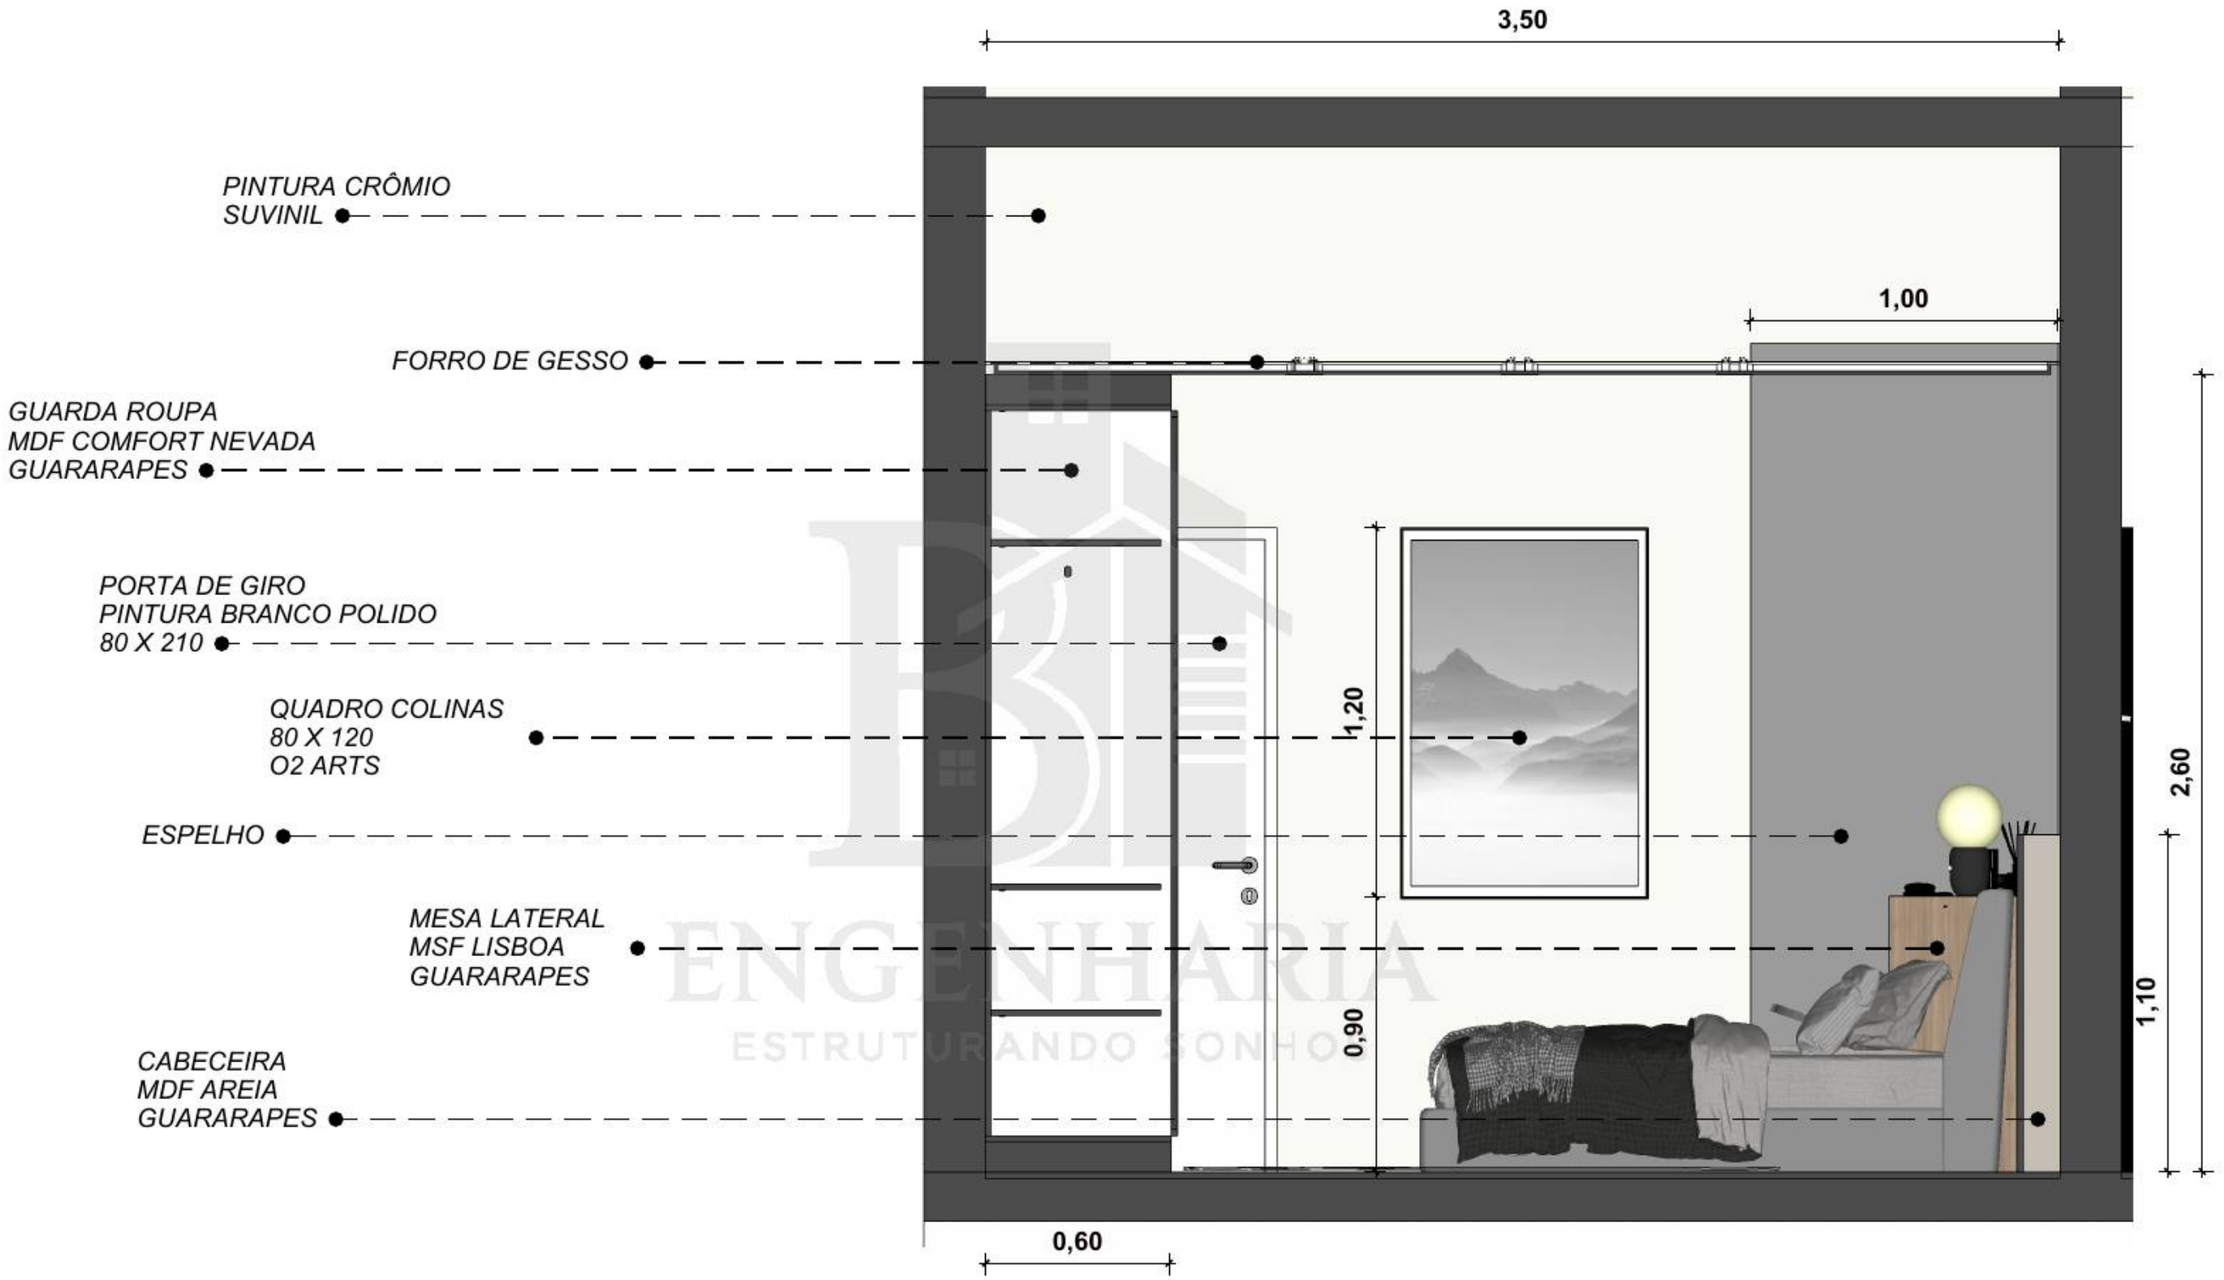

46 **VISTA B - SUÍTE**
Esc: 1/20

DF ENGENHARIA
ESTRUTURANDO SONHOS


W.C. SUÍTE - VISTA B

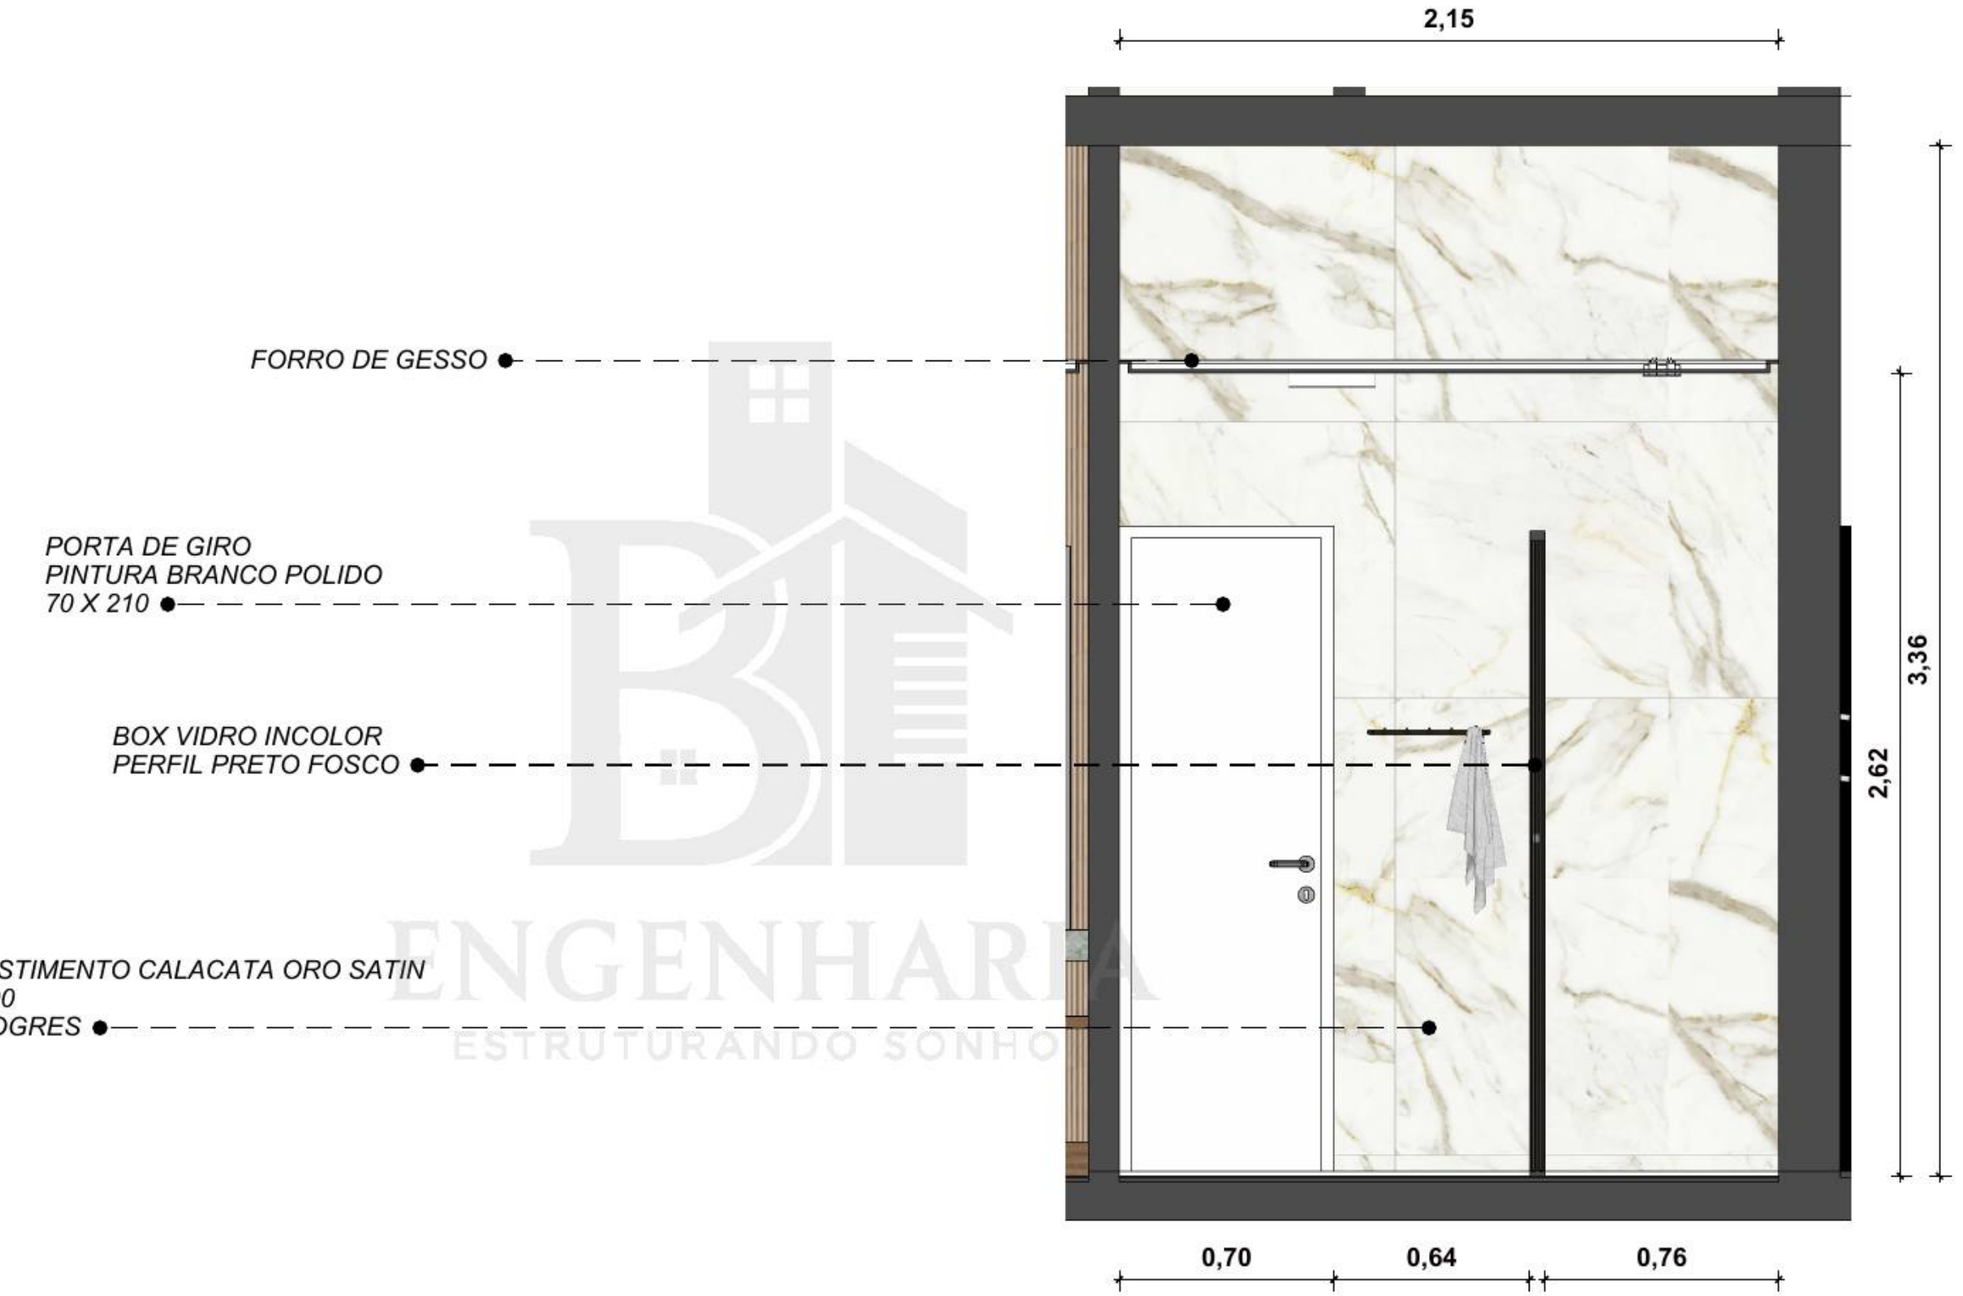

47 **VISTA B - W.C. SUÍTE**
Esc: 1/20

ENGENHARIA
ESTRUTURANDO SONHOS


SUÍTE - VISTA C

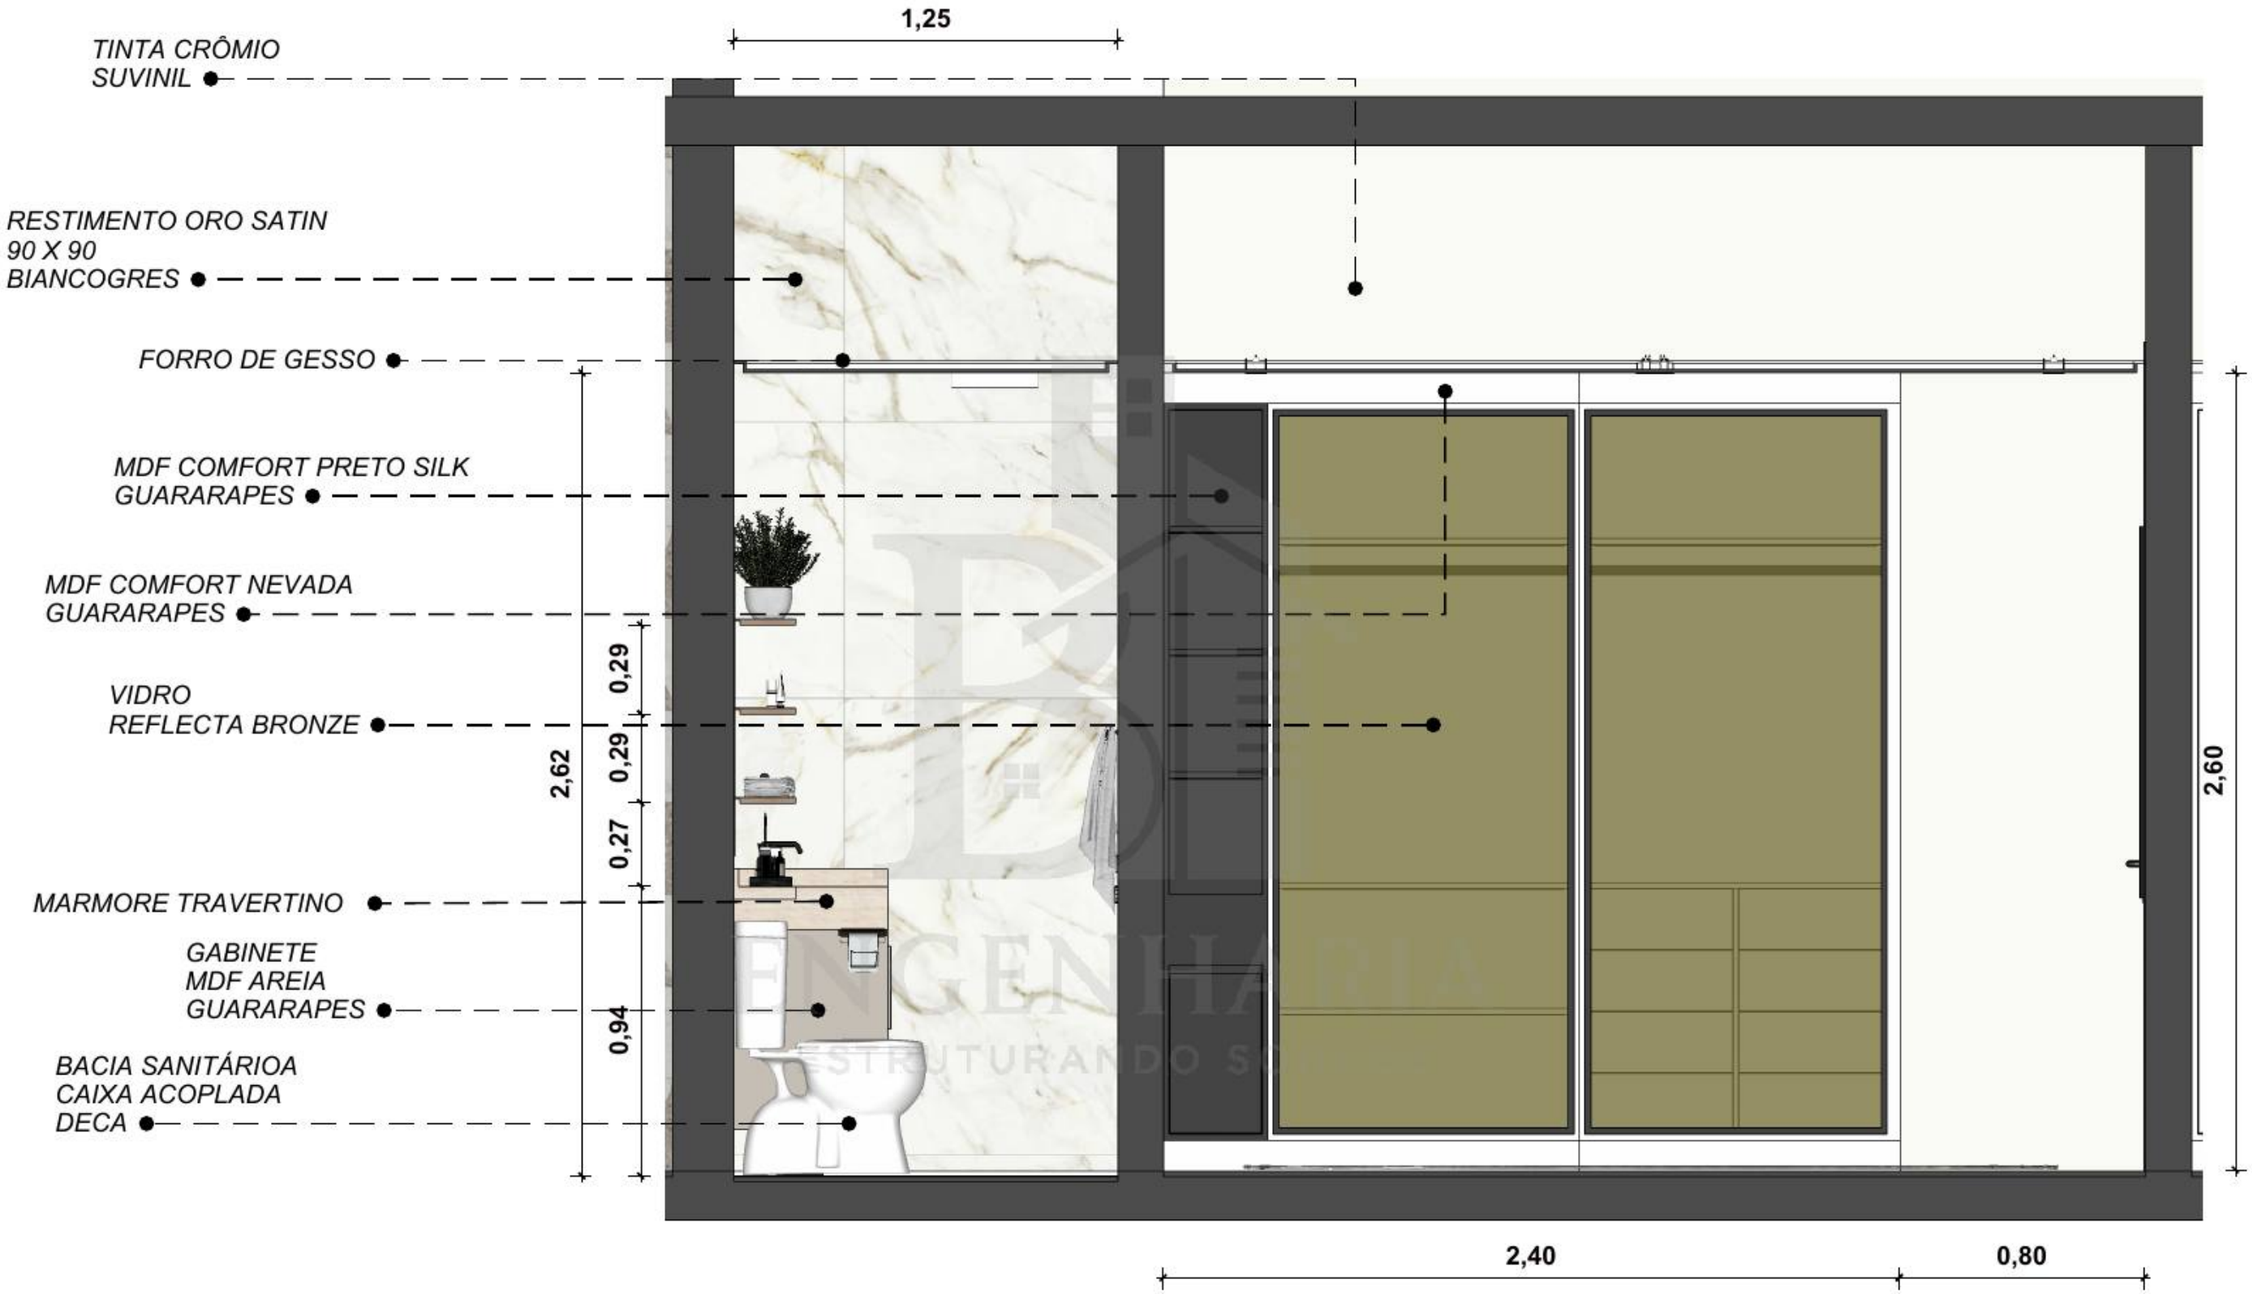

48 **VISTA C - SUÍTE**
Esc: 1/20

PRANCHA
45/60


SUÍTE - VISTA D

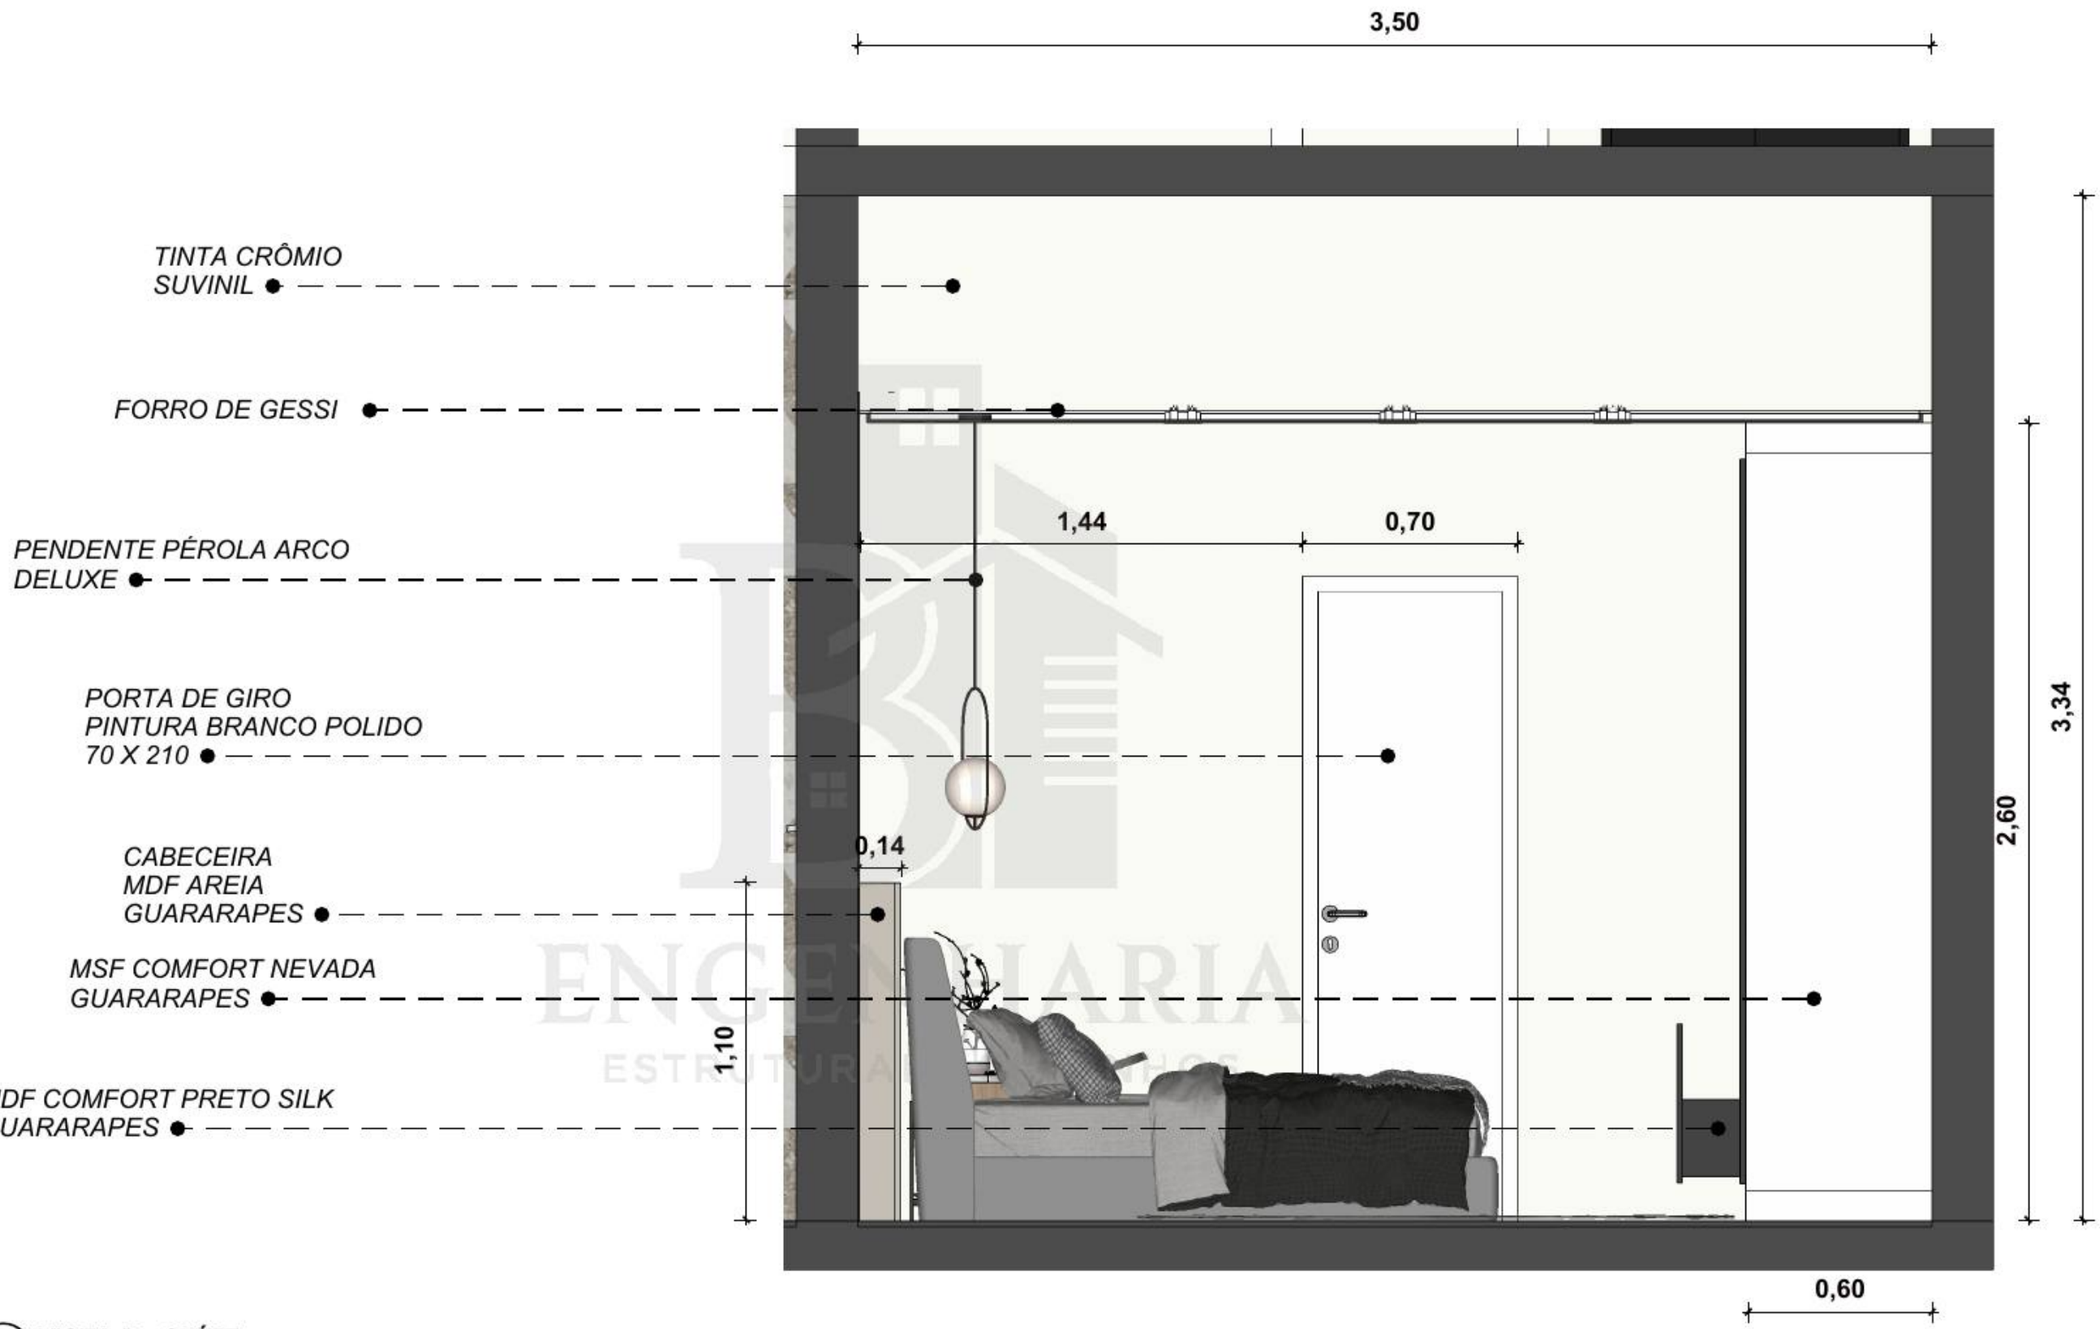

49 **VISTA D - SUÍTE**
Esc: 1/20

ENGENHARIA
ESTRUTURAIS


W.C. SUÍTE - VISTA D

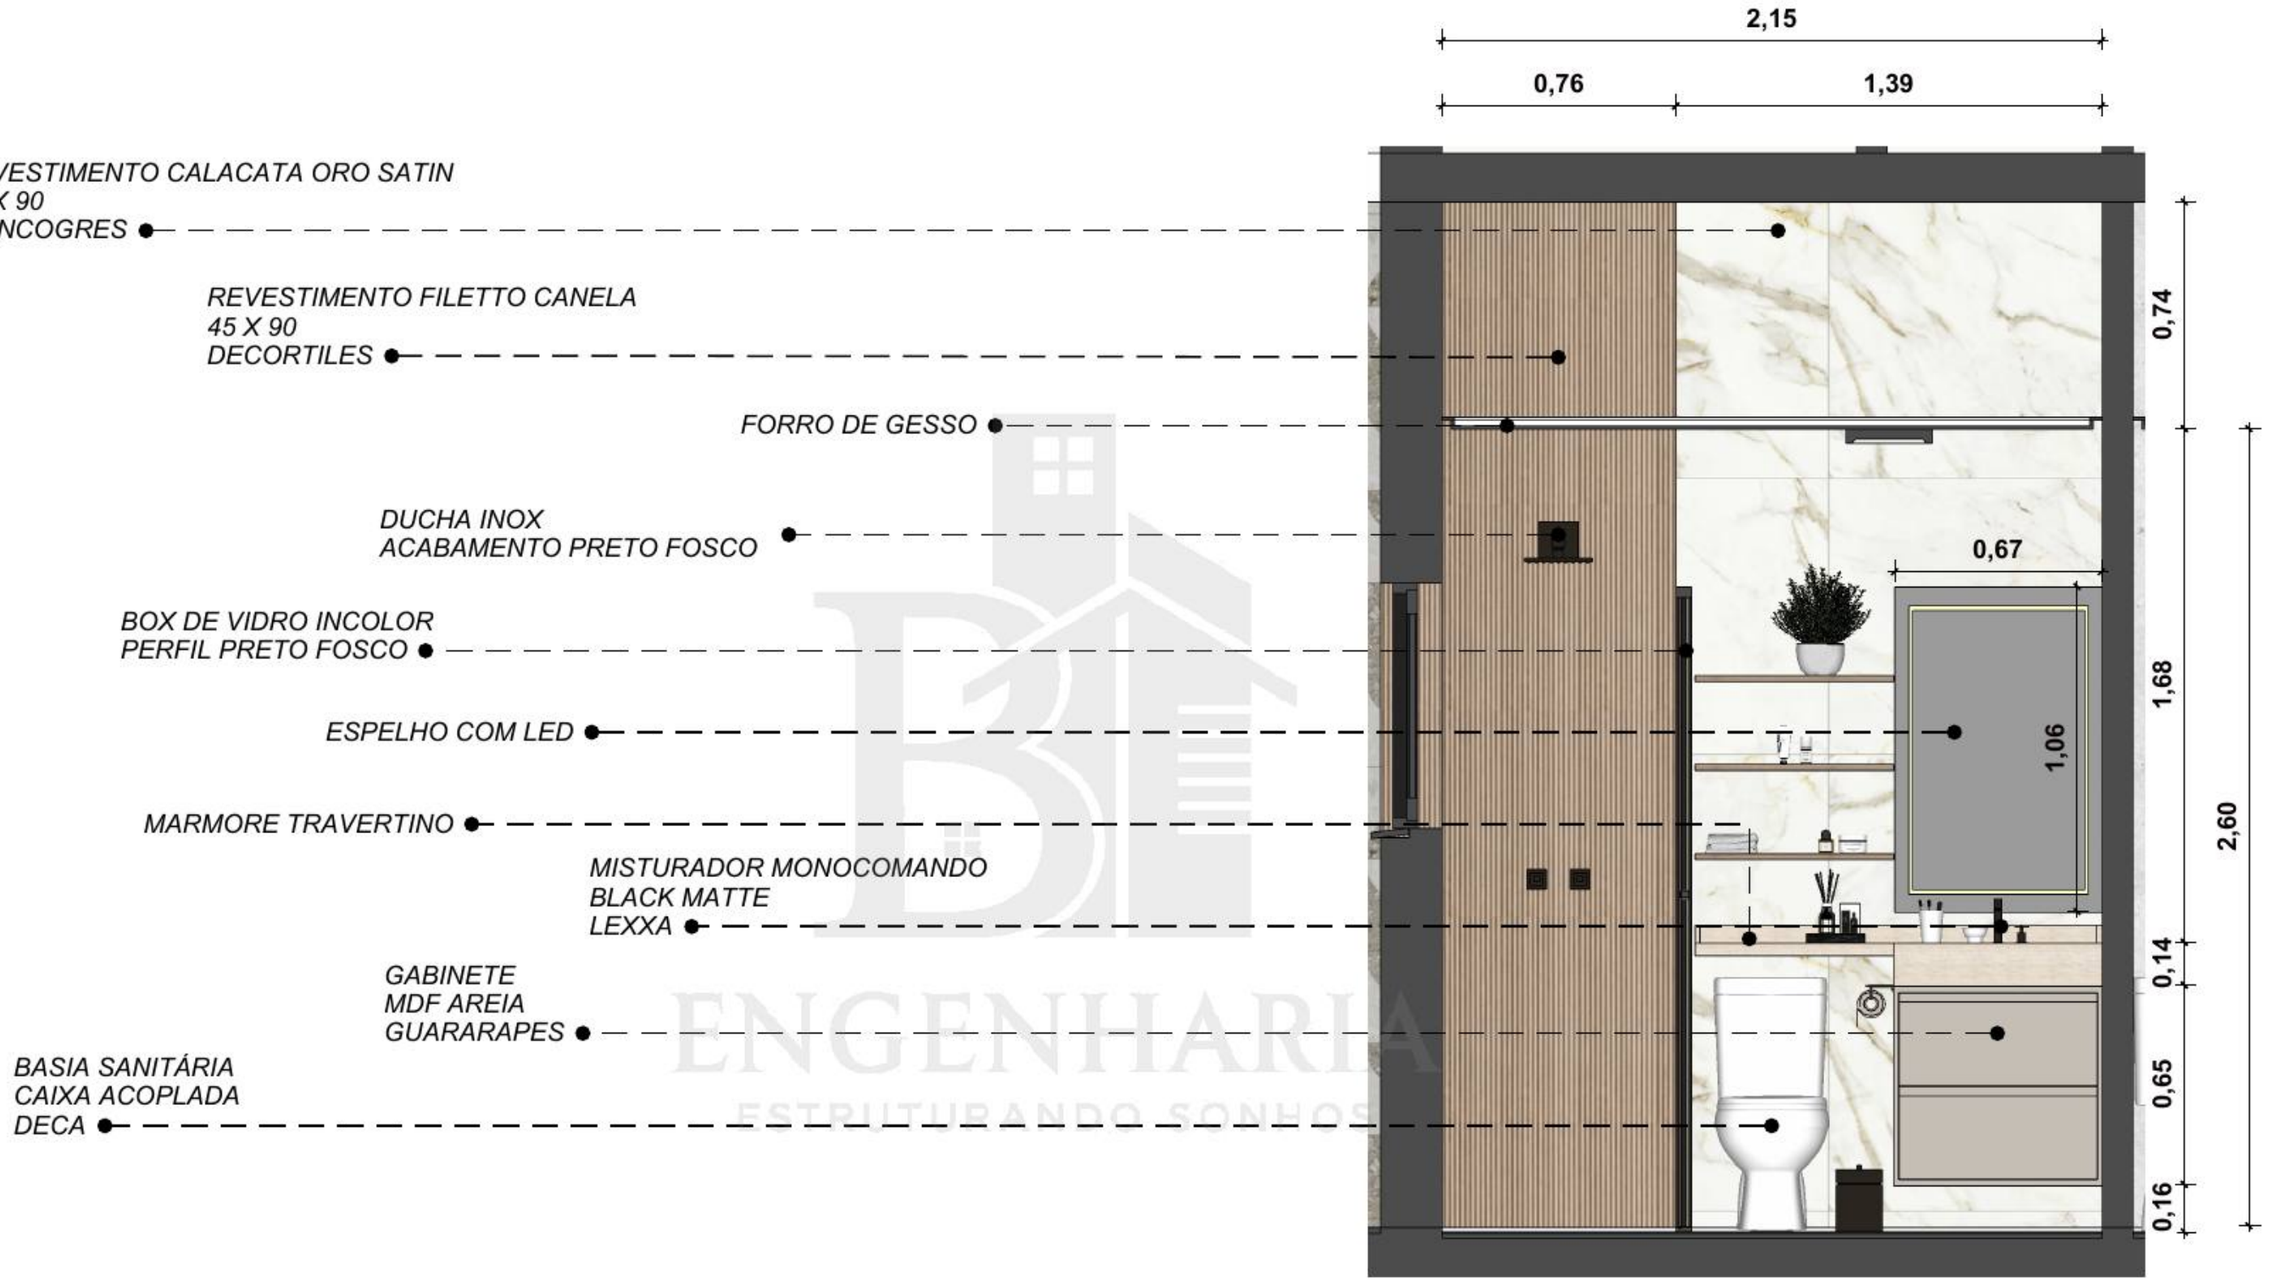


50 **VISTA D - W.C. SUÍTE**
Esc: 1/20

ENGENHARIA
ESTRUTURANDO SONHOS


W.C. SUÍTE - DETALHAMENTO

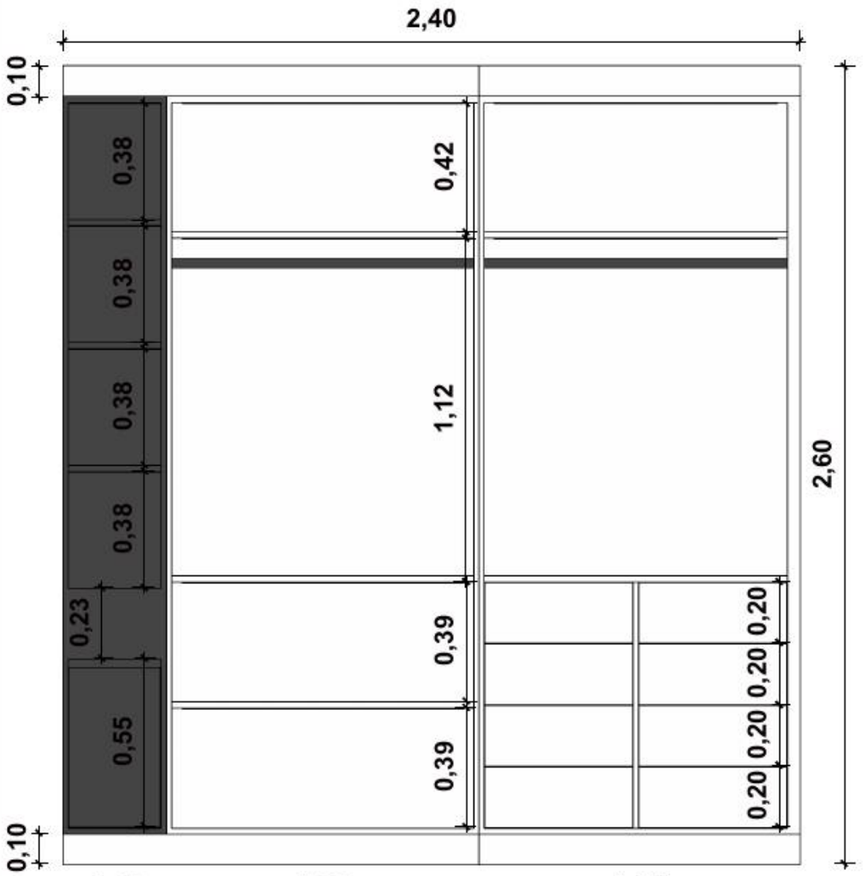


VISTA FRONTAL - GUARDA ROUPA

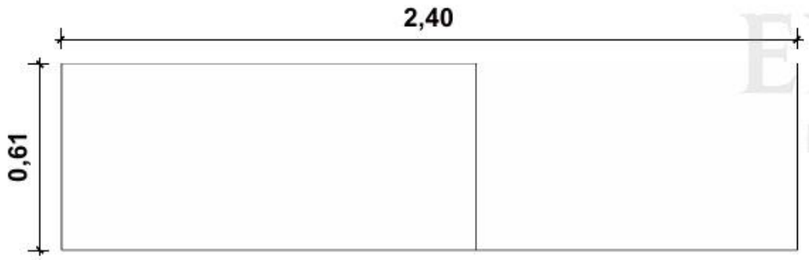


VISTA EM PLANTA - GUARDA ROUPA

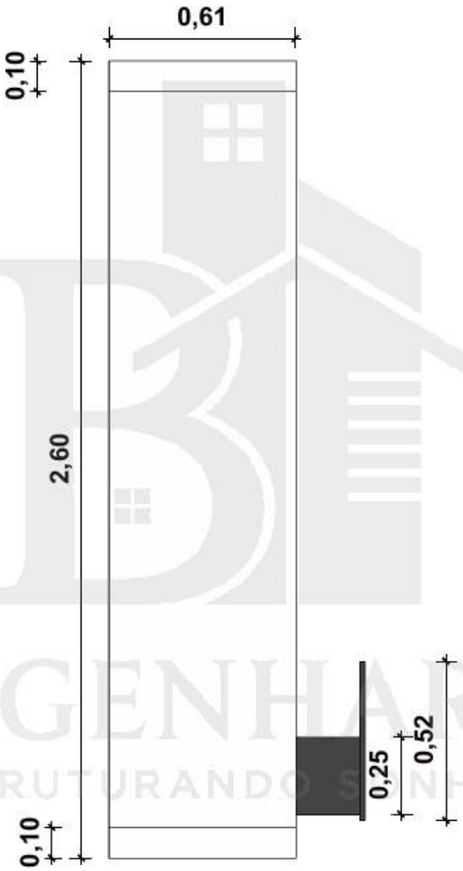

VISTA LATERAL
GUARDA ROUPA

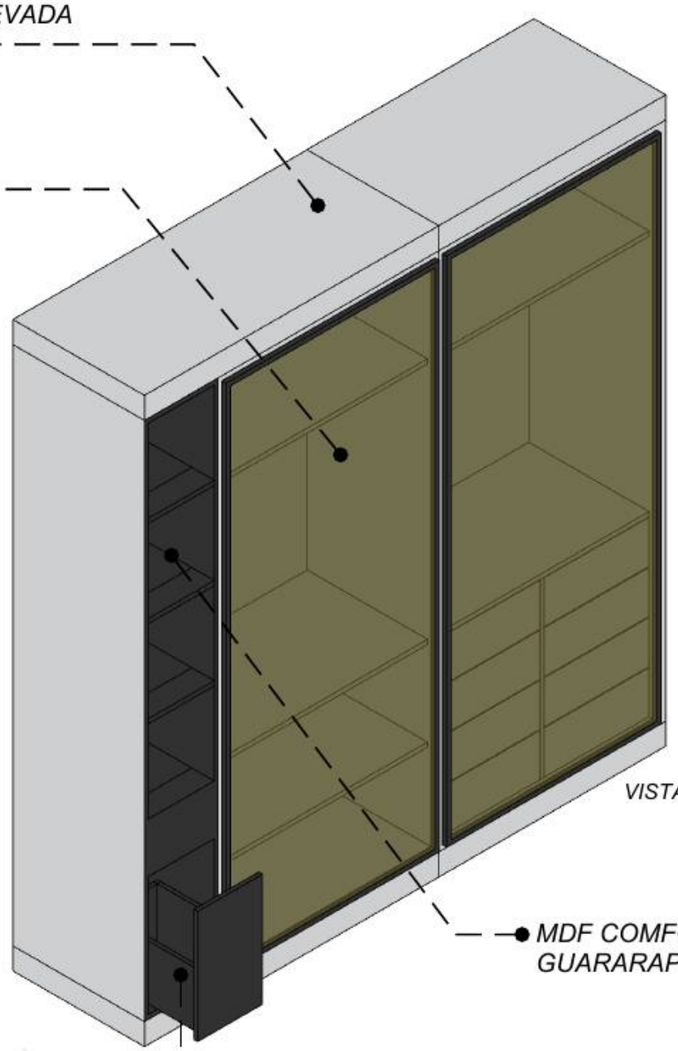


VISTA EM PERSPECTIVA
GUARDA ROUPA

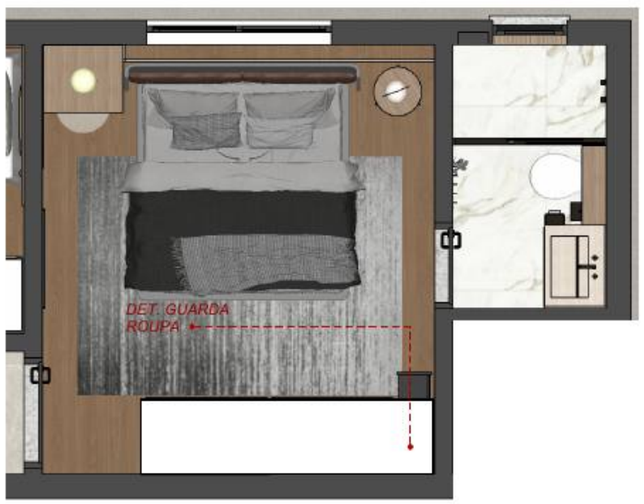


51 **DETALHAMENTO - SUÍTE**
Esc: 1/20

ENGENHARIA
ESTRUTURANDO SONHOS


W.C. SUÍTE - DETALHAMENTO

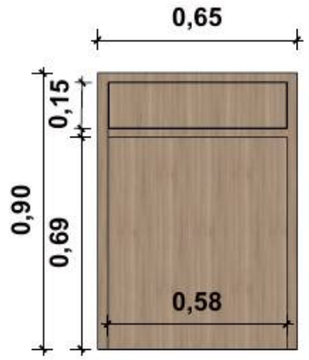


VISTA FRONTAL
MESA DE CABECEIRA

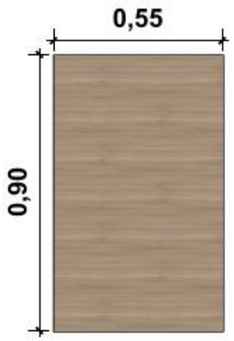


VISTA LATERAL
MESA DE CABECEIRA

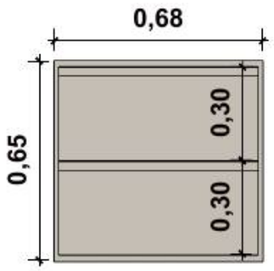


VISTA FRONTAL - GABINETE

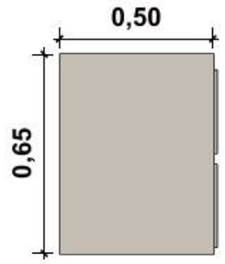


VISTA LATERAL - GABINETE

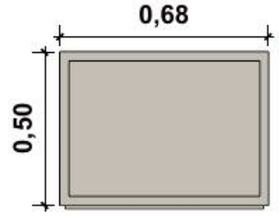


VISTA EM PLANTA - GABINETE

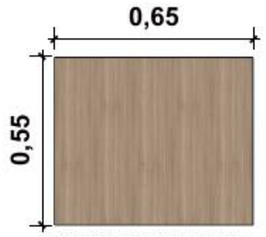


VISTA EM PLANTA
MESA DE CABECEIRA

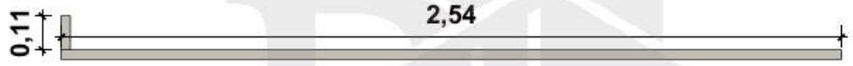


VISTA EM PLANTA - CABECEIRA

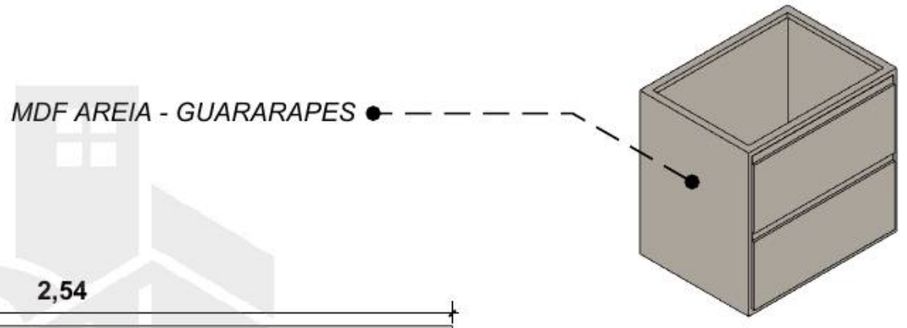


VISTA EM PERSPECTIVA
GABINETE

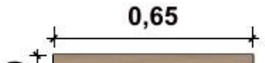


VISTA EM PLANTA
PRATELEIRA

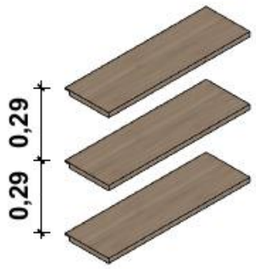


VISTA EM PERSPECTIVA
PRATELEIRA

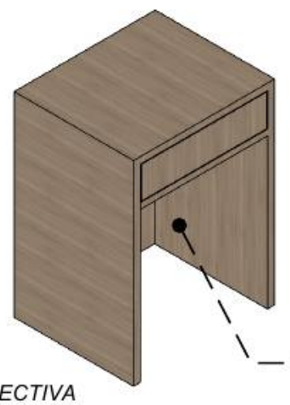

VISTA EM PERSPECTIVA
MESA DE CABECEIRA

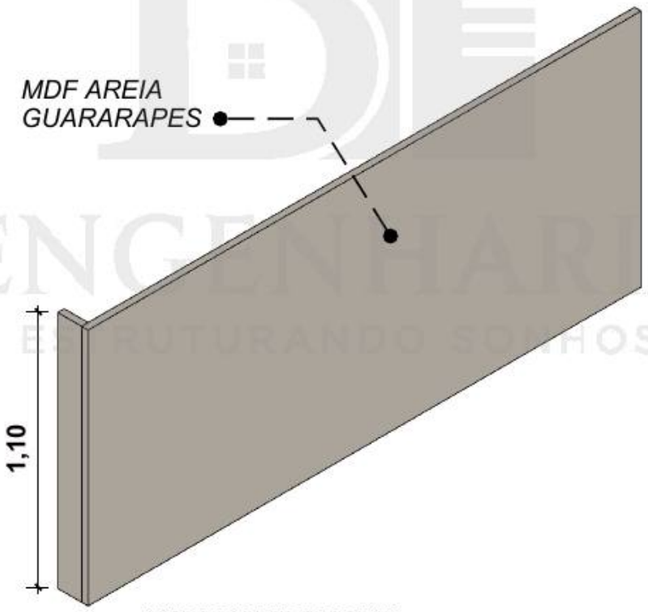


VISTA EM PERSPECTIVA
CABECEIRA

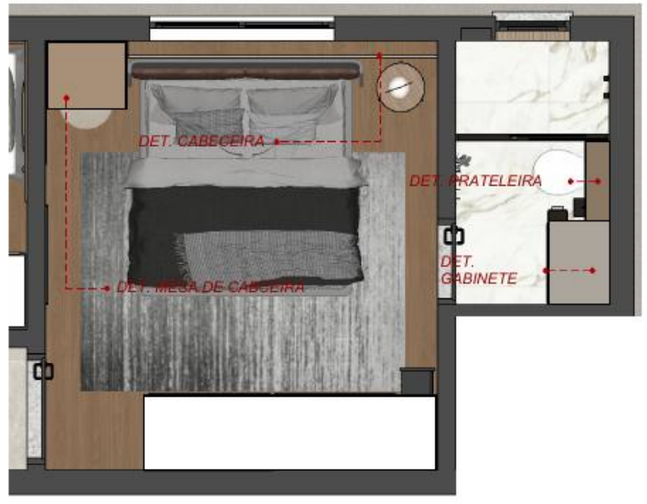

52 **DETALHAMENTO - SUÍTE**
Esc: 1/20

ENGENHARIA
ESTRUTURANDO SONHOS


QUARTO - PLANTA BAIXA

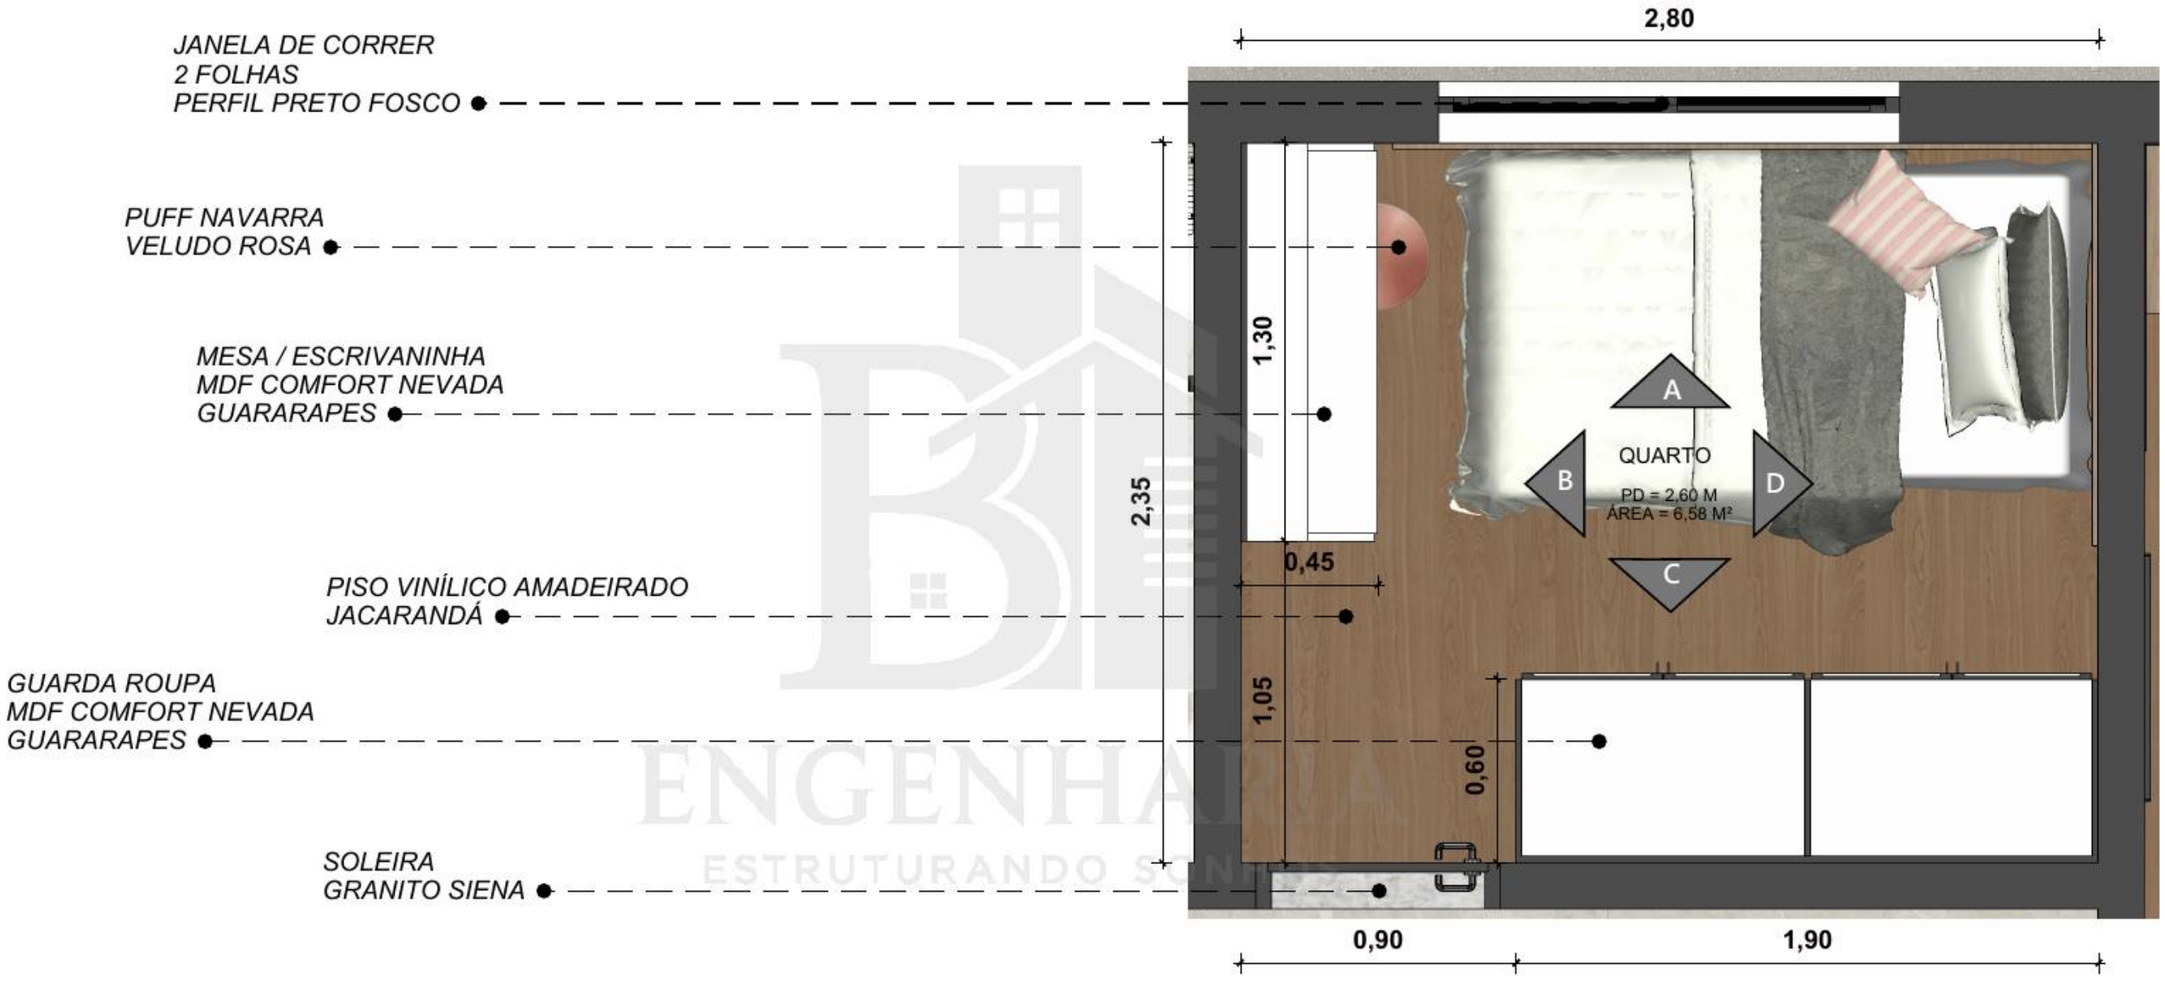

53 **PLANTA BAIXA - QUARTO**
Esc: 1/20

ENGENHARIA
ESTRUTURANDO SONHOS


QUARTO - VISTA A

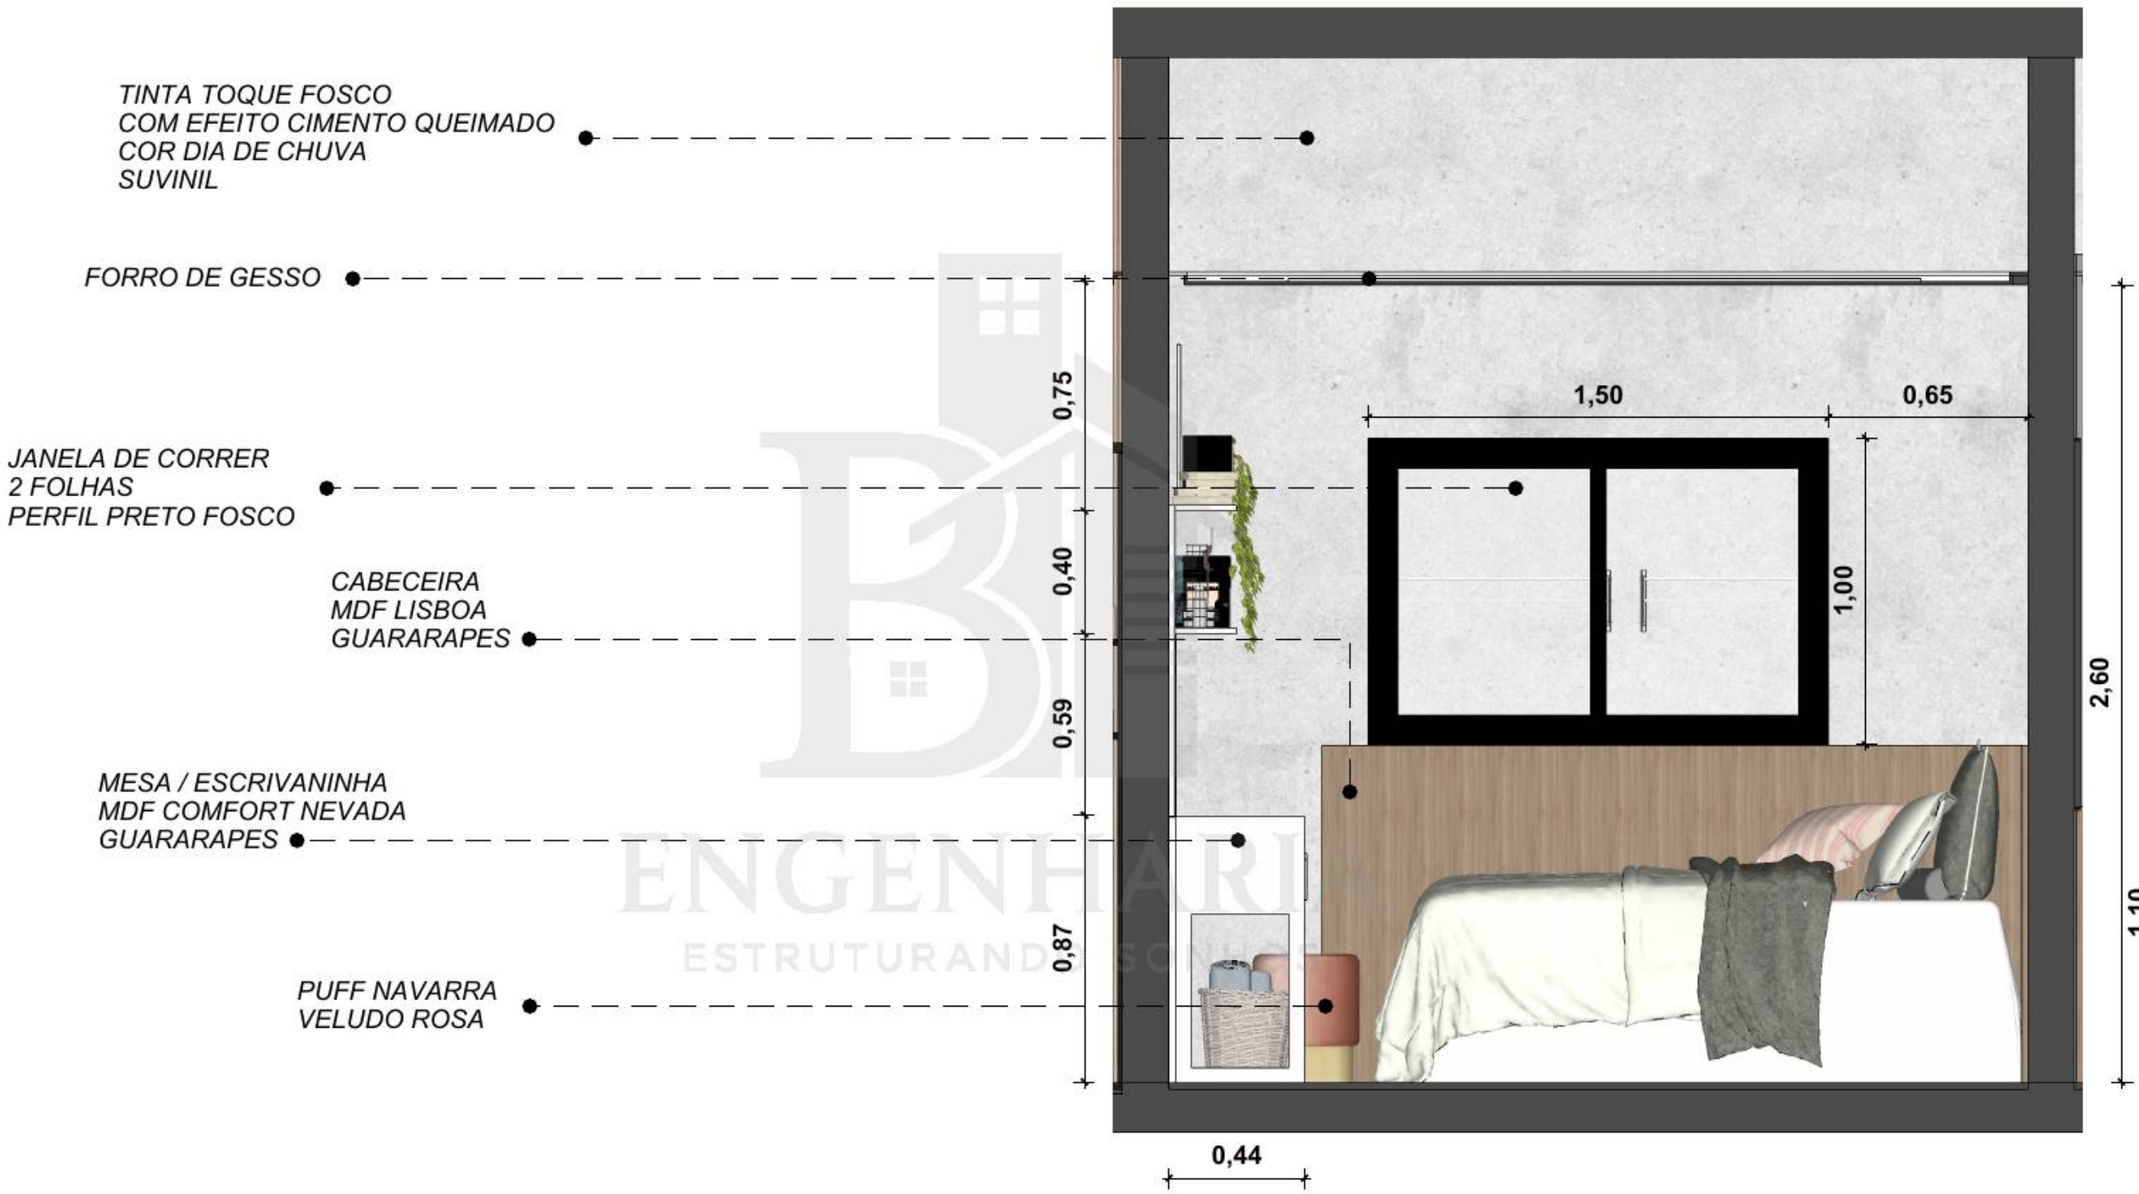

54 **VISTA A - QUARTO**
Esc: 1/20

ENGENHARIA
ESTRUTURANDO SONHOS


QUARTO - VISTA B

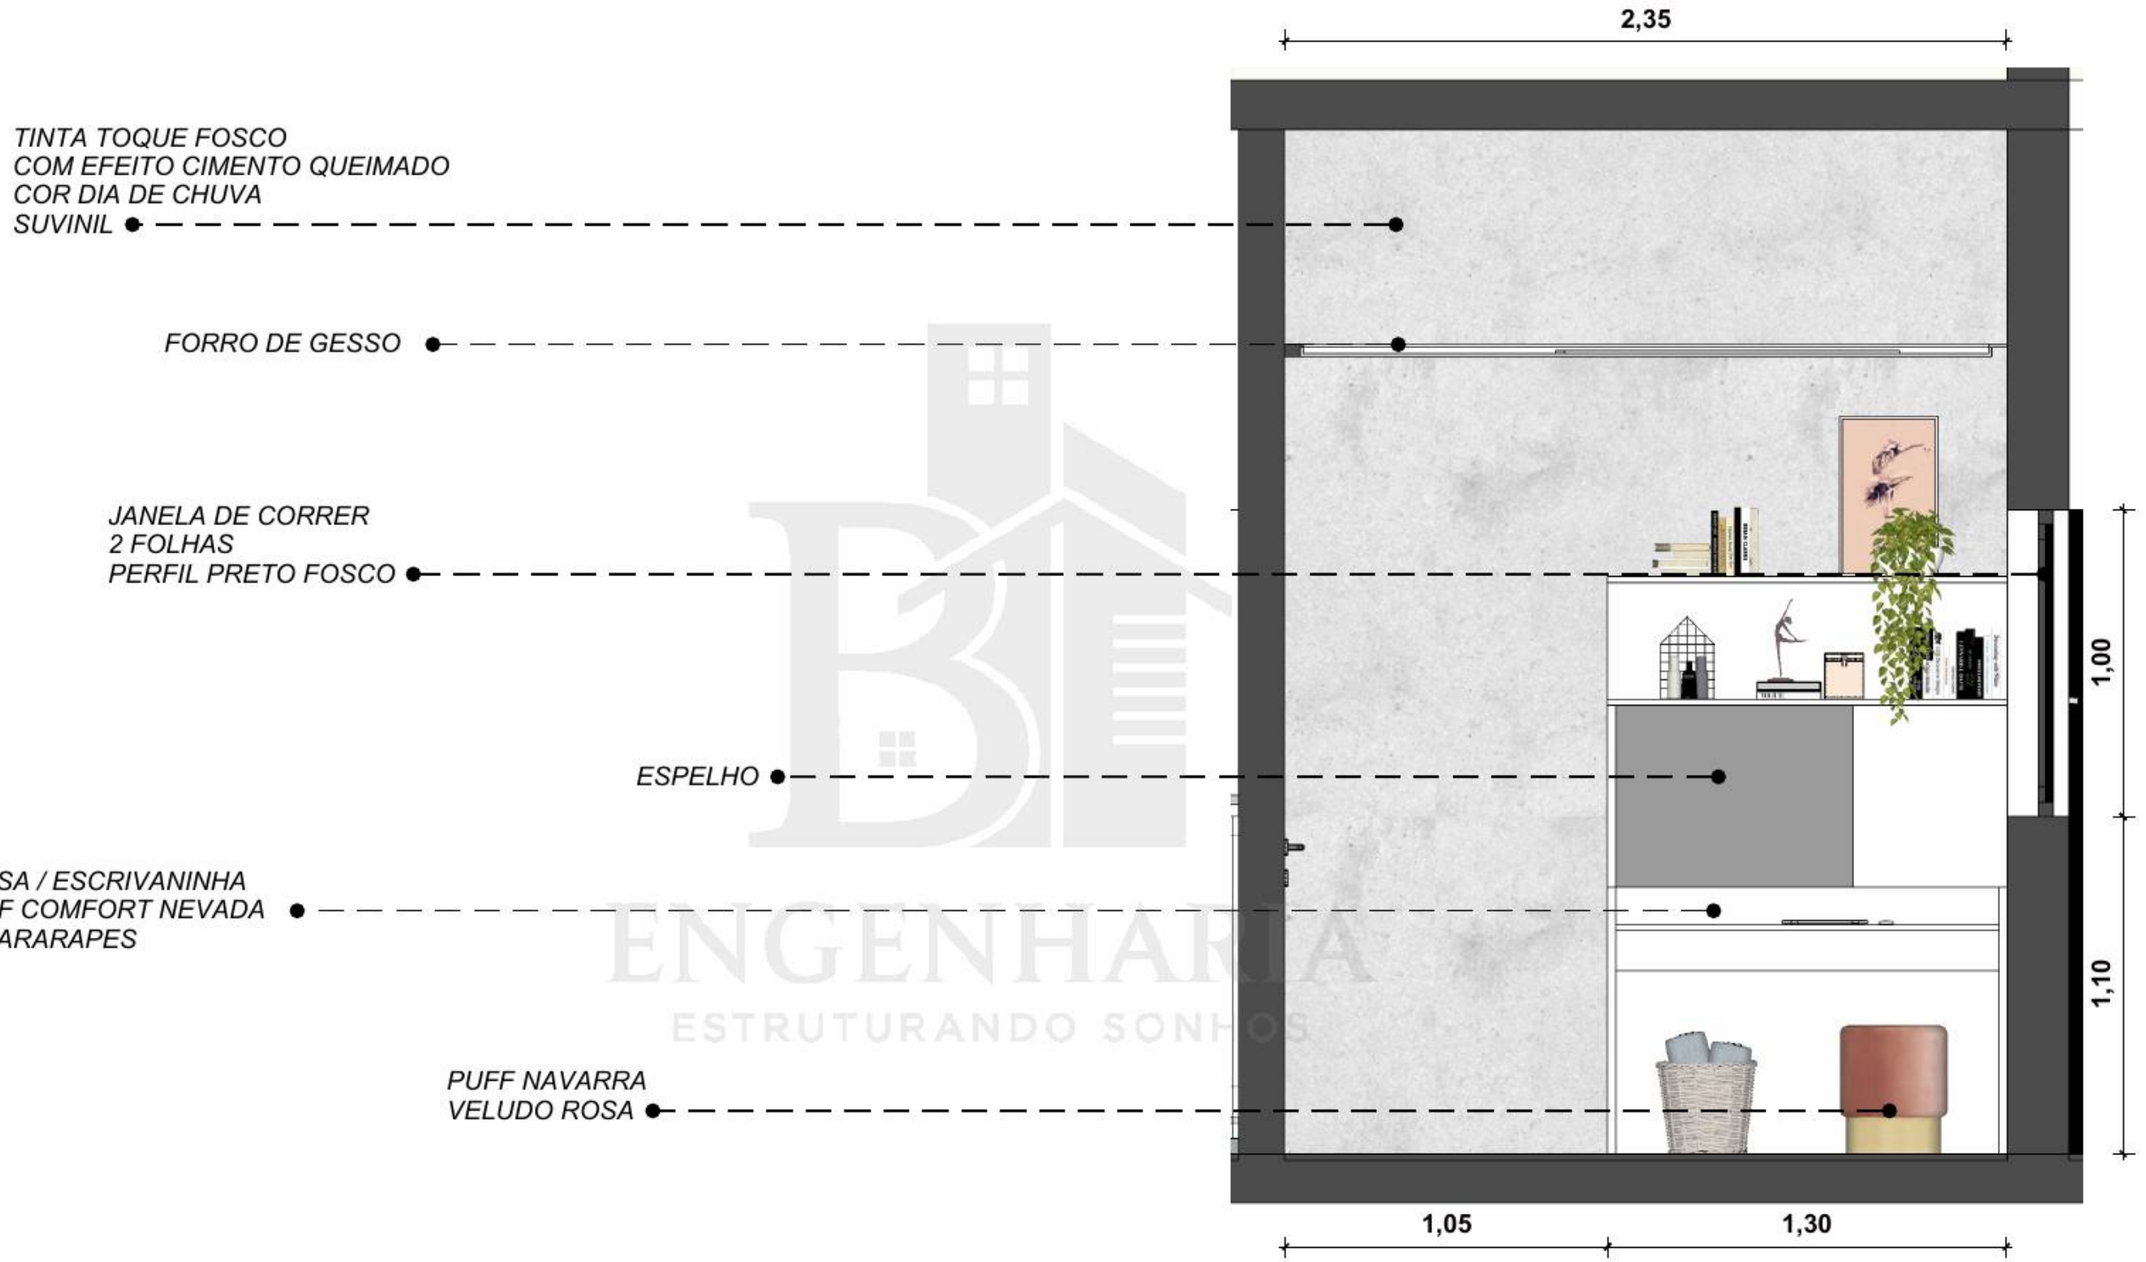

55 **VISTA B - QUARTO**
Esc: 1/20

ENGENHARIA
ESTRUTURANDO SONHOS


QUARTO - VISTA C

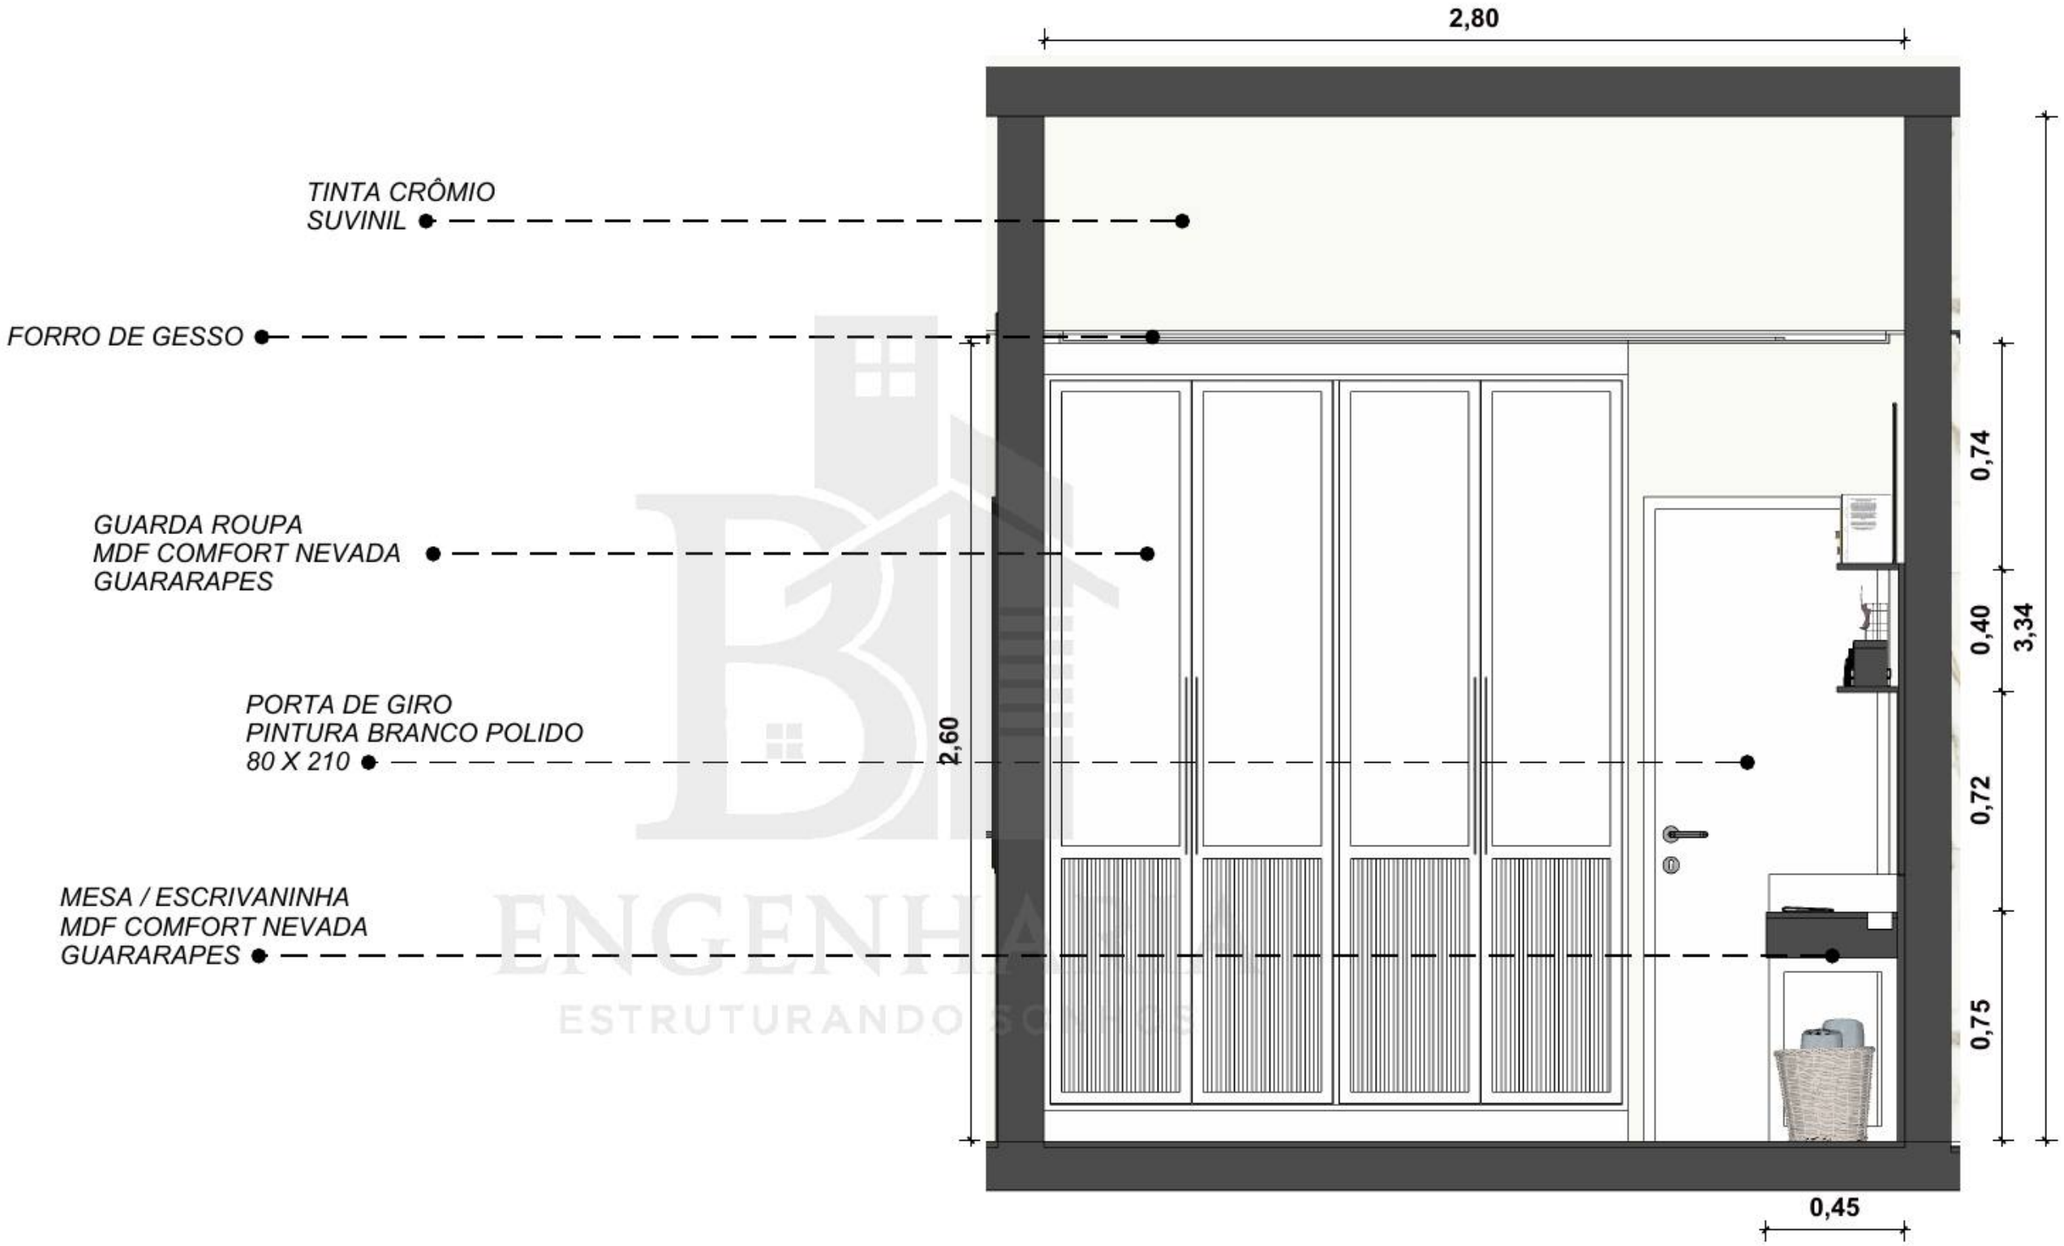

56 **VISTA C - QUARTO**
Esc: 1/20

ENGENHARIA
ESTRUTURANDO SONHOS


QUARTO - VISTA D

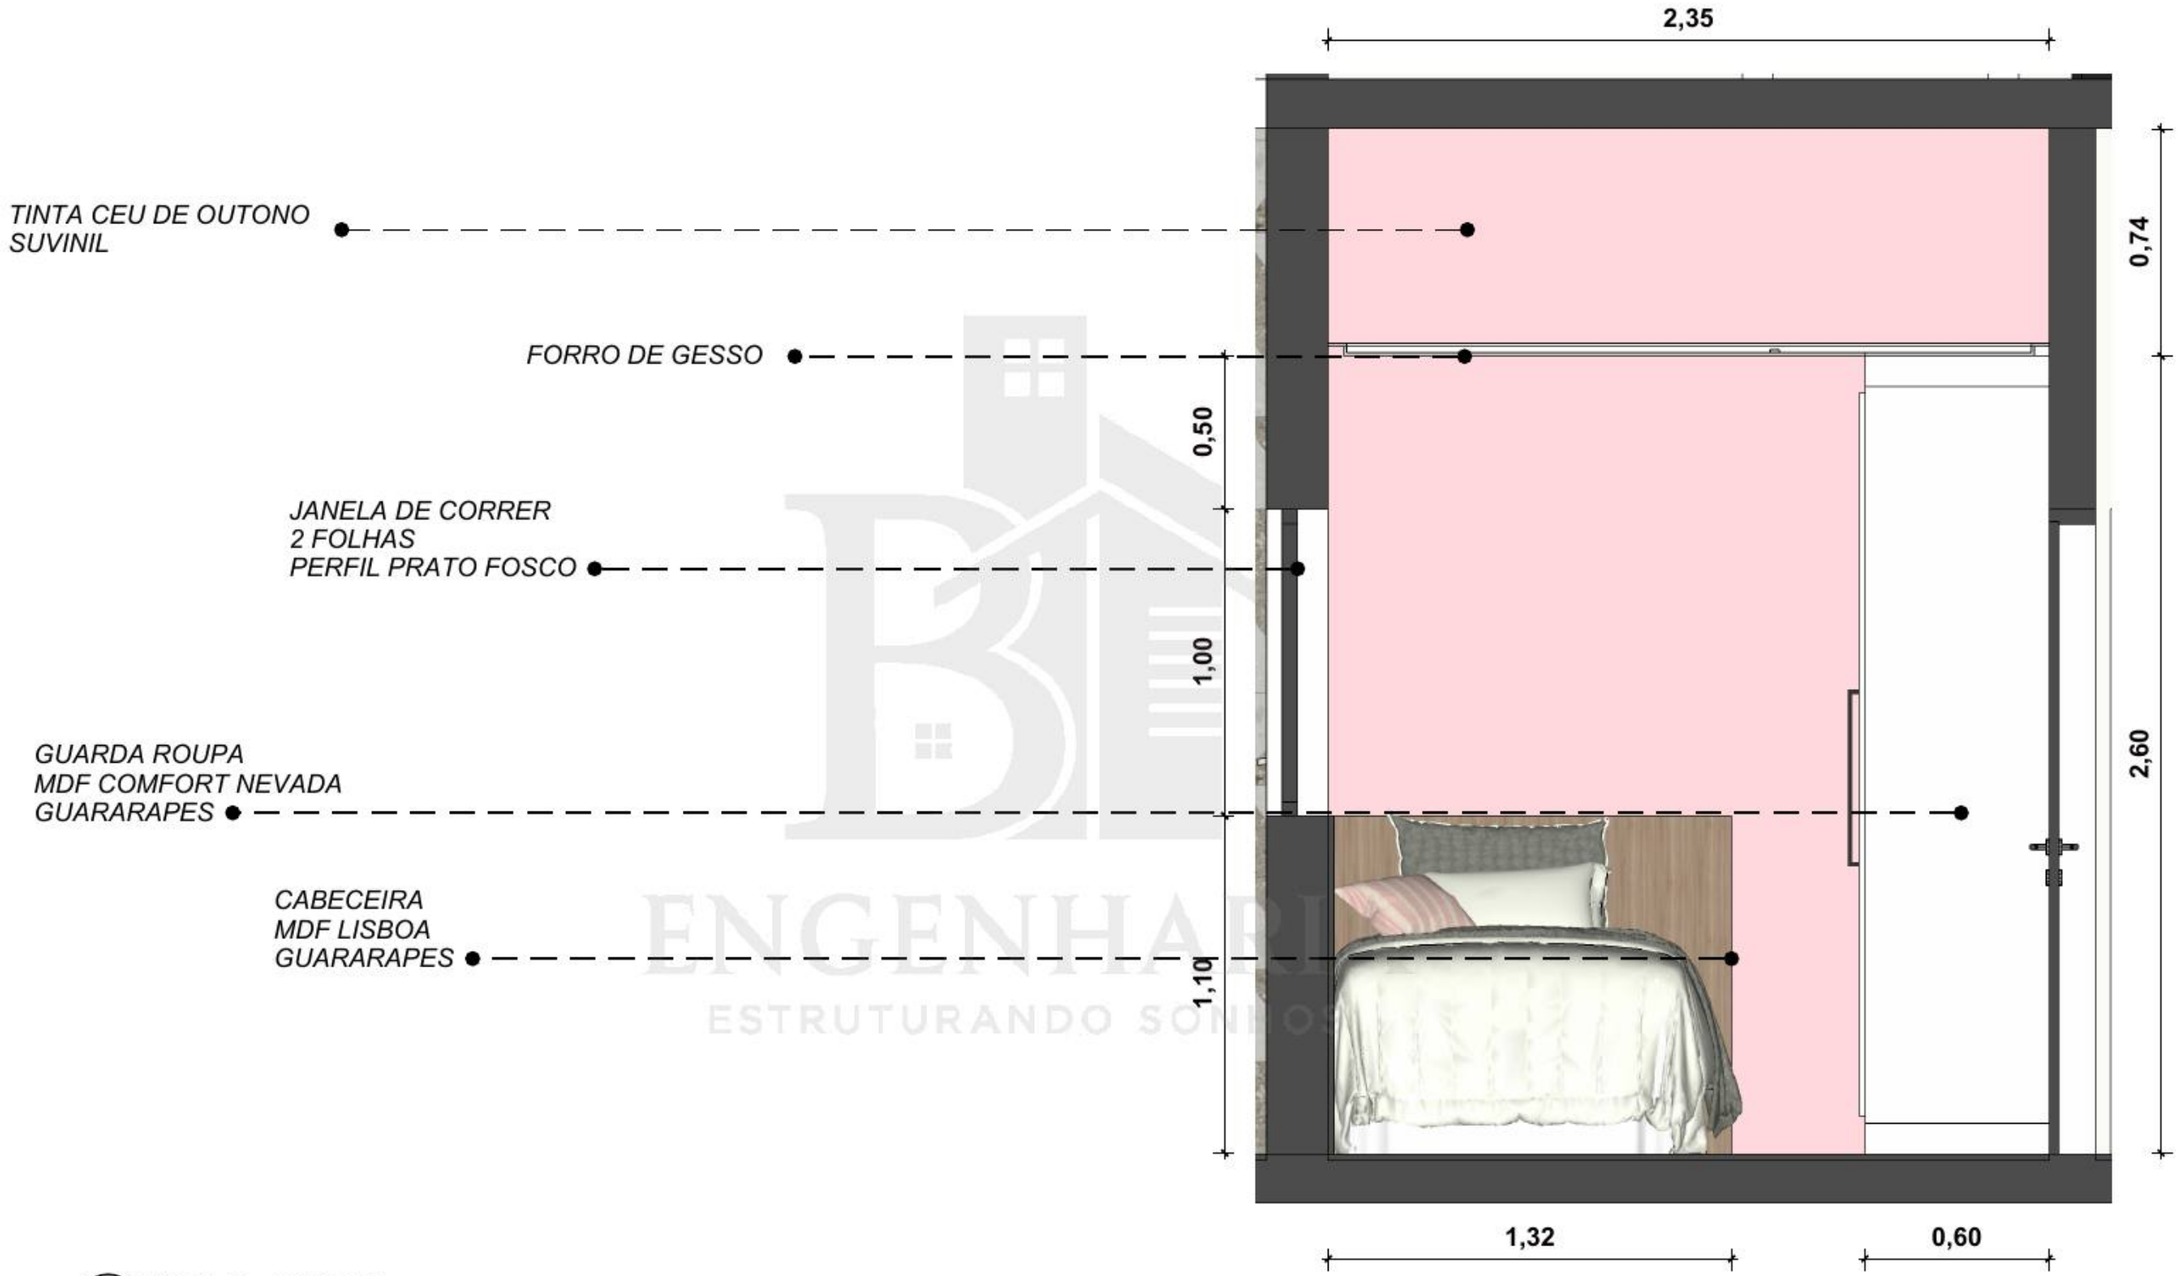


57 **VISTA D - QUARTO**
Esc: 1/20

ENGENHARIA
ESTRUTURANDO SONHOS


QUARTO - DETALHAMENTO

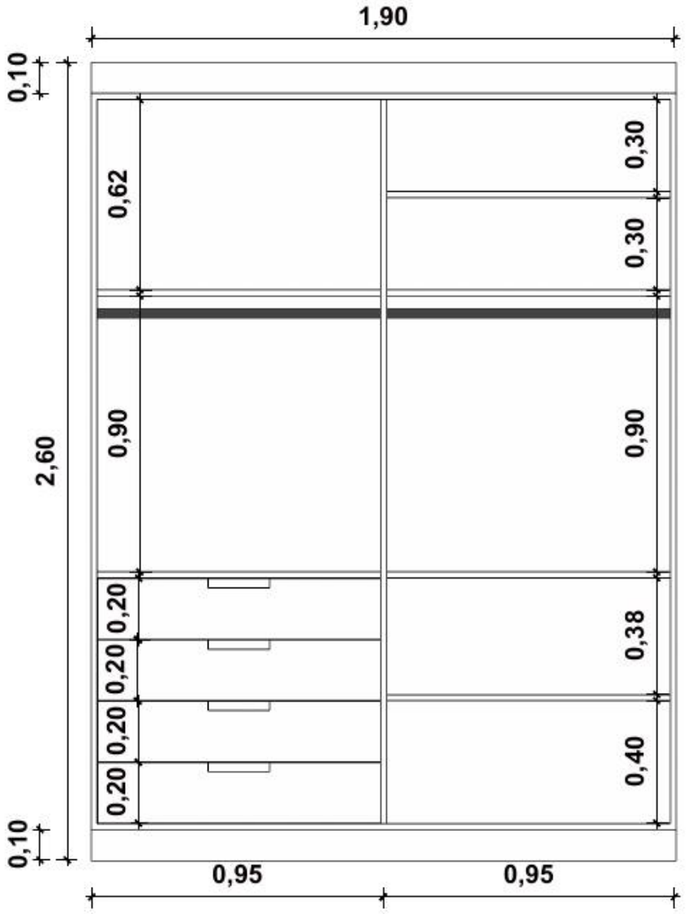


VISTA FRONTAL - GUARDA ROUPA

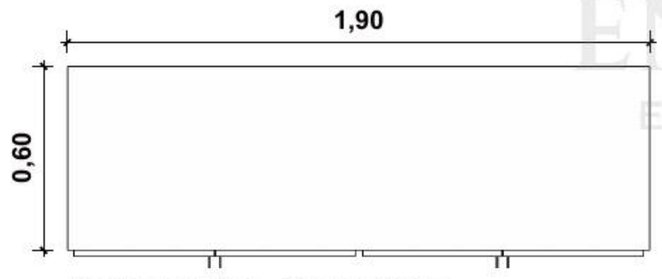


VISTA EM PLANTA - GUARDA ROUPA

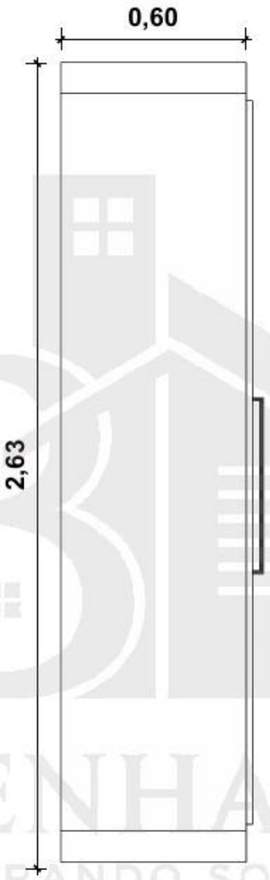

VISTA LATERAL
GUARDA ROUPA

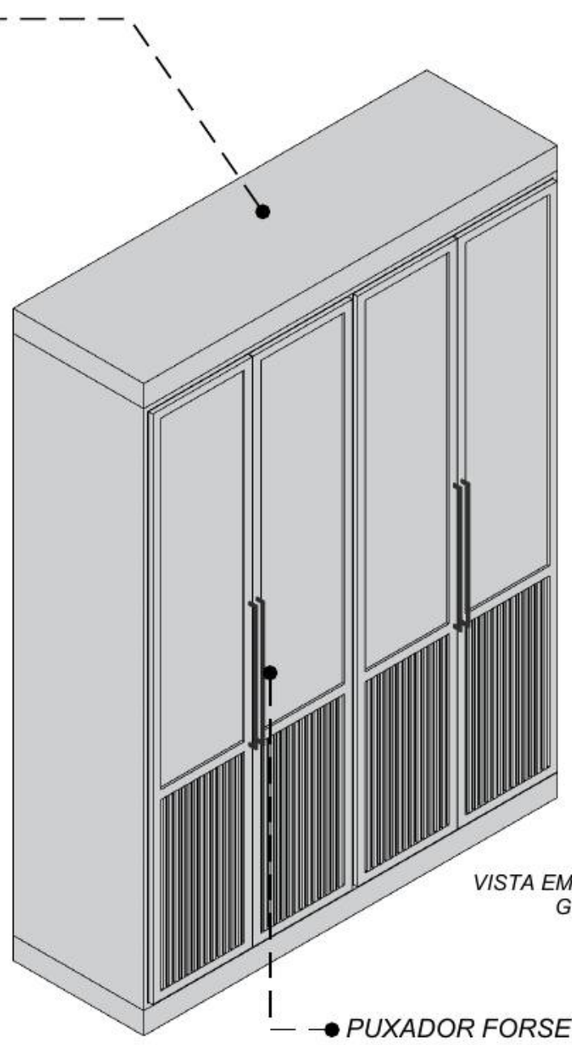


VISTA EM PERSPECTIVA
GUARDA ROUPA

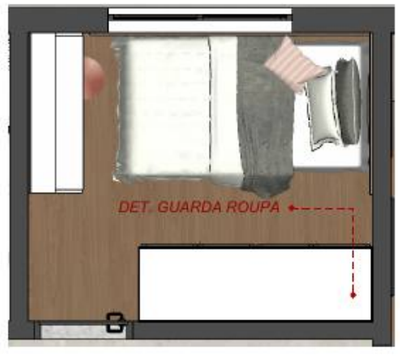


58 **DETALHAMENTO - QUARTO**
Esc: 1/20

ENGENHARIA
ESTRUTURANDO SONHOS


QUARTO - DETALHAMENTO

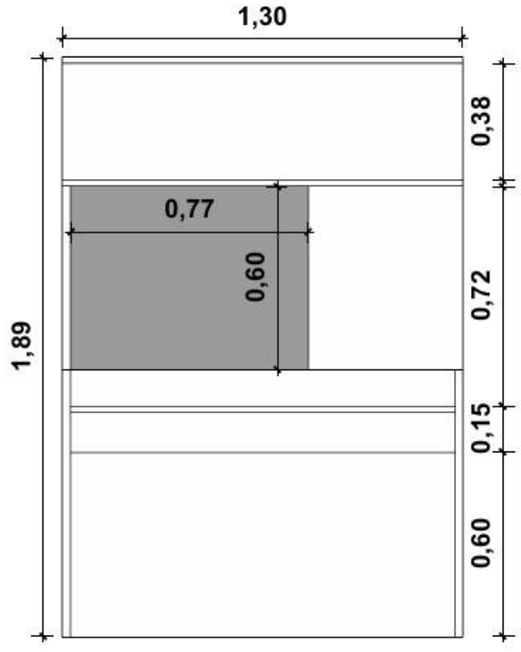


VISTA FRONTAL - ESCRIVANINHA

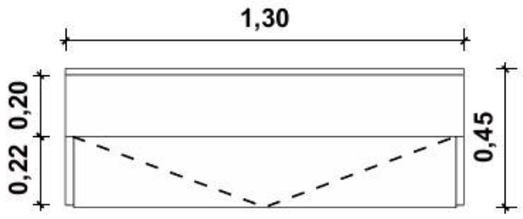


VISTA EM PLANTA
ESCRIVANINHA

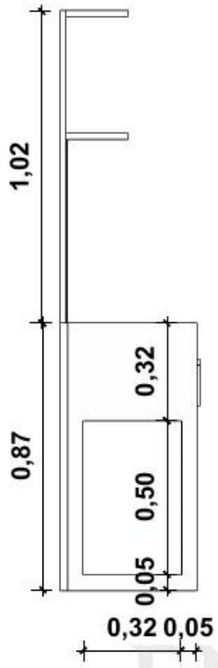


VISTA LATERAL
ESCRIVANINHA

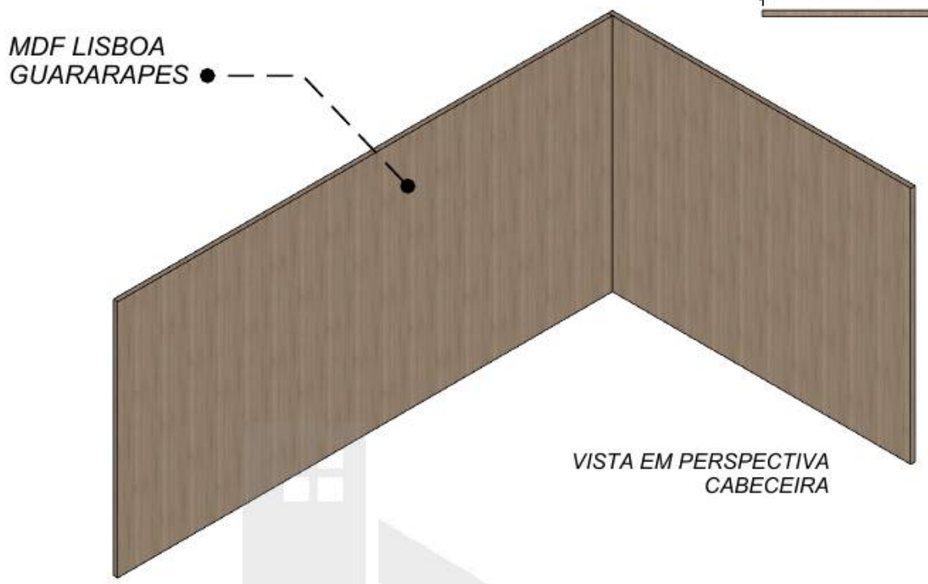


VISTA EM PERSPECTIVA
CABECEIRA

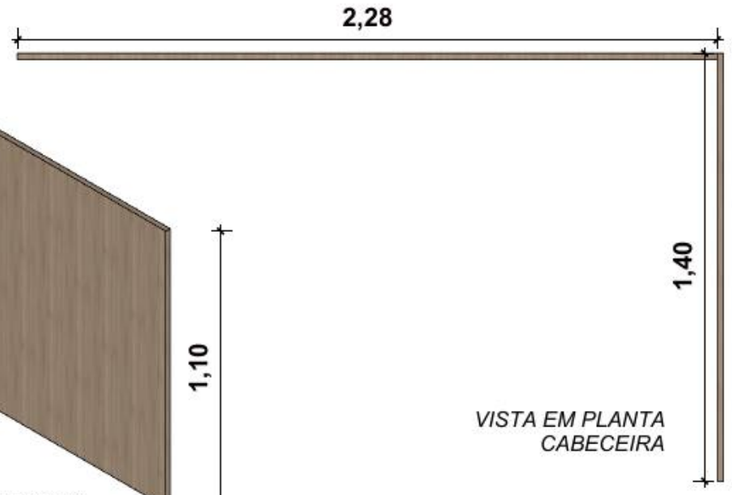

VISTA EM PLANTA
CABECEIRA

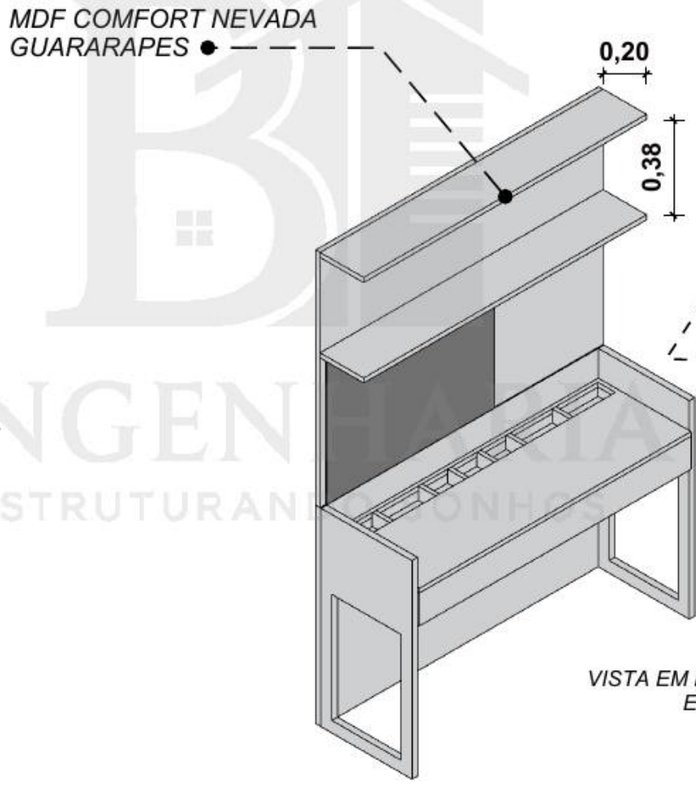

VISTA EM PERSPECTIVA
ESCRIVANINHA

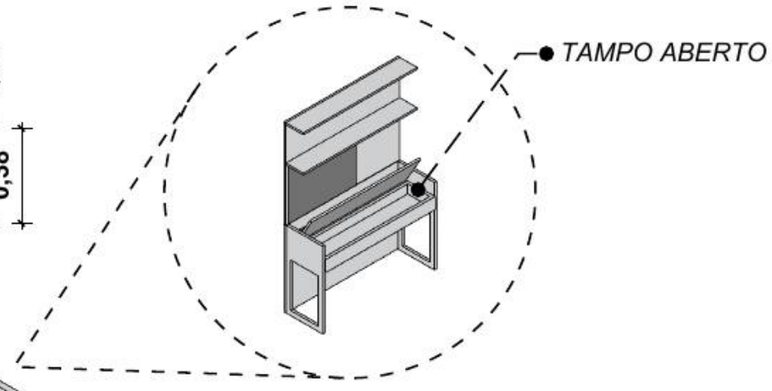



59 **DETALHAMENTO - QUARTO**
Esc: 1/20

ENGENHARIA
ESTRUTURANDO SONHOS

BANHEIRO - PLANTA BAIXA / VISTA A



REVESTIMENTO CALACATA ORO SATIN
90 X 90
BIANCOGRES

PRATELEIRA
MDF LISBOA
GUARARAPES

CUBA ESCUPIDA
MARMORE TRAVERTINO

SOLEIRA
GRANITO SIENA

60 **PLANTA BAIXA - BANHEIRO**
Esc: 1/20



FORRO DE GESSO

REVESTIMENTO FILETTO CANELA
45 X 90
DECORTILES

BOX DE VIDRO INCOLOR
PERFIL PRETO FOSCO

BACIA SANITÁRIA
CAIXA ACOPLADA
DECA

61 **VISTA A - BANHEIRO**
Esc: 1/20

ENGENHARIA
ESTRUTURANDO SONHOS

BANHEIRO - VISTA B,C



REVESTIMENTO CALACATA ORO SATIN
90 X 90
BIANCOGRES

FORRO DE GESSO

REVESTIMENTO FILETTO CANELA
45 X 90
DECORTILES

PORTA DE GIRO
PINTURA BRANCO POLIDO
70 X 210


ESPELHO
CAMARIM RAVINA

MISTURADOR MONOCOMANDO
BLACK MATTE
LEXXA

CUBA ESCUPIDA
MARMORE TRAVERTINO

GABINETE
MDF VERDE FLORESTA
DURATEX

BACIA SANITÁRIA
CAIXA ACOPLADA
DECA

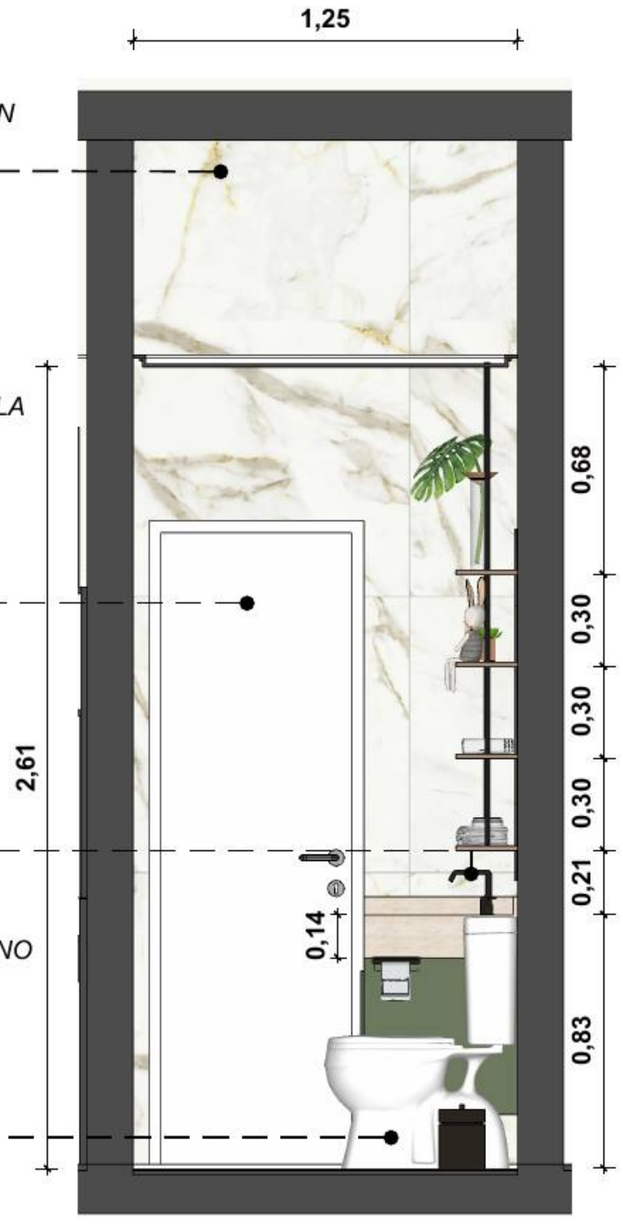

62 **VISTA B - BANHEIRO**
Esc: 1/20

63 **VISTA C - BANHEIRO**
Esc: 1/20

BANHEIRO - VISTA D

REVESTIMENTO CALACATAORO SATIN
90 X 90
BIANCOGRES

FORRO DE GESSO

REVESTIMENTO FILETTO CANELA
45 X 90
DECORTILES

JANELA MAXIM AR
ALUMÍNIO PRETO FOSCO

PORTA DE GIRO
PINTURA BRANCO POLIDO
70 X 210


BOX VIDRO INCOLOR
PERFIL PRETO FOSCO




64 **VISTA D - BANHEIRO**
Esc: 1/20

ENGENHARIA
ESTRUTURANDO SONHOS


BANHEIRO - DETALHAMENTO

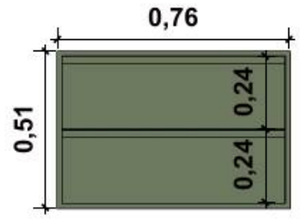


VISTA FRONTAL - GABINETE

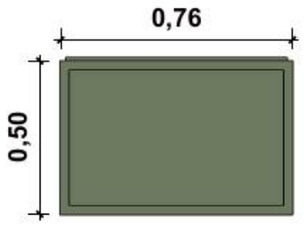

VISTA EM PLANTA - GABINETE

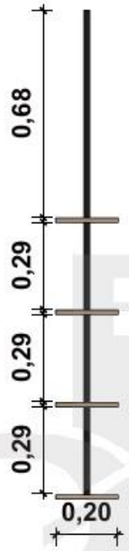

VISTA LATERAL
PRATELEIRA

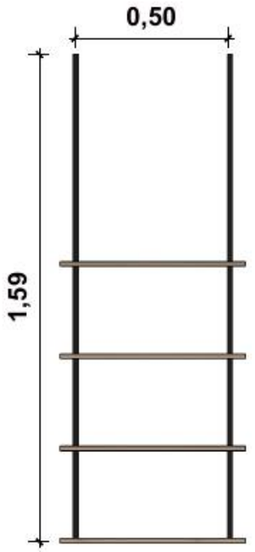


VISTA FRONTAL
PRATELEIRA

PERFIL EM ALUMÍNIO
PRETO FOSCO




VISTA EM PERSPECTIVA
PRATELEIRA

MDF LISBOA
GUARARAPES

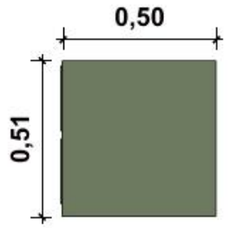


VISTA LATERAL
GABINETE

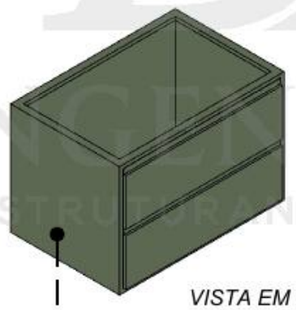

VISTA EM PERSPECTIVA
GABINETE

MDF VERDE FLORESTA
DURATEX

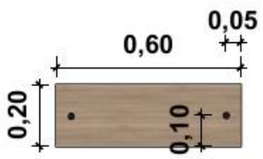

VISTA EM PLANTA
PRATELEIRA



65 **DETALHAMENTO - BANHEIRO**
Esc: 1/20

DF ENGENHARIA
ESTRUTURANDO SONHOS

PRANCHA
60/60