

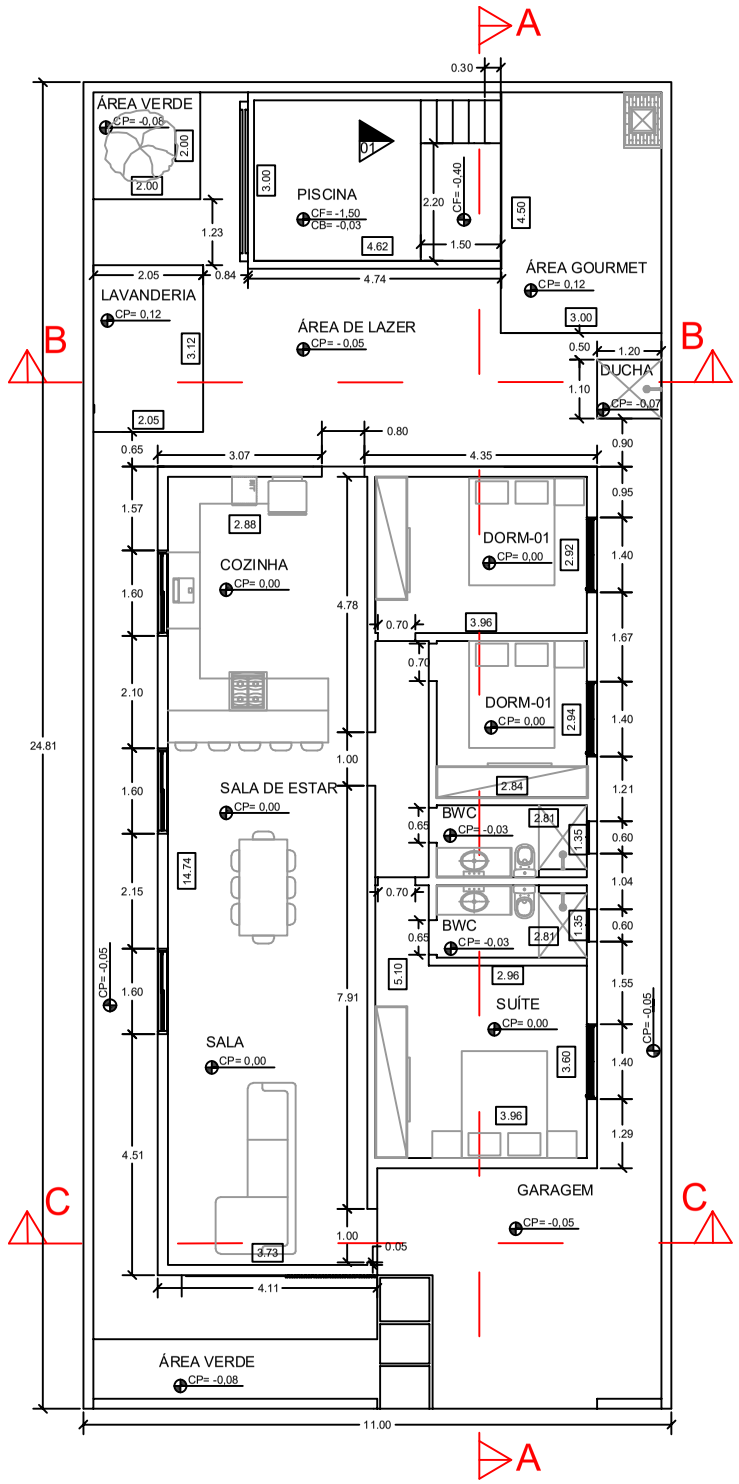



PLANTA BAIXA

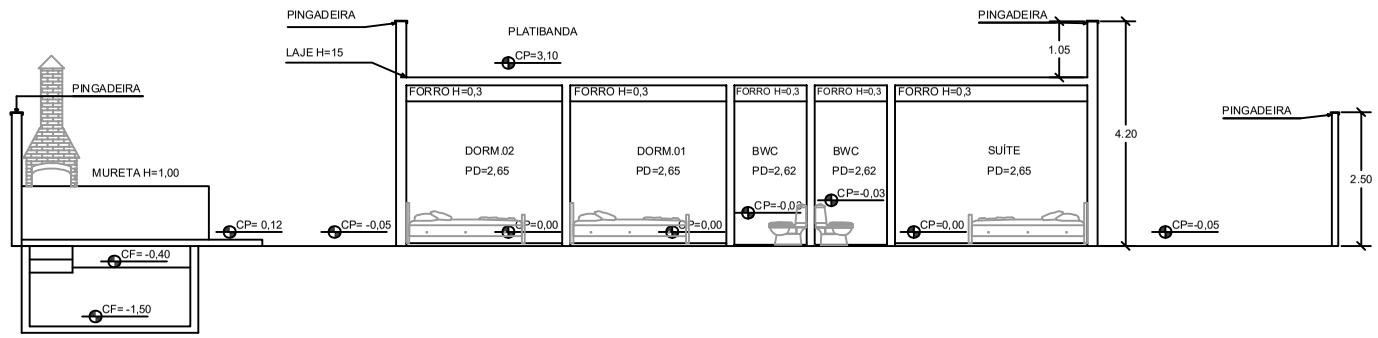


CORTE AA

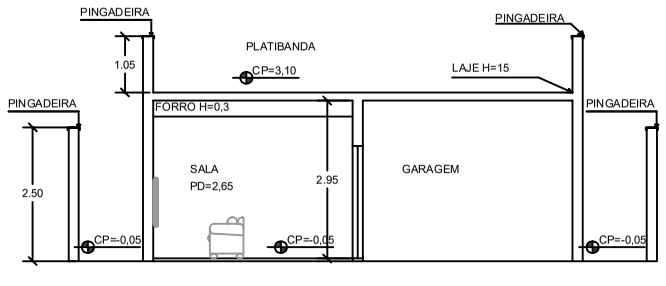

CORTE CC

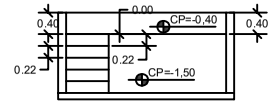

VISTA PISCINA

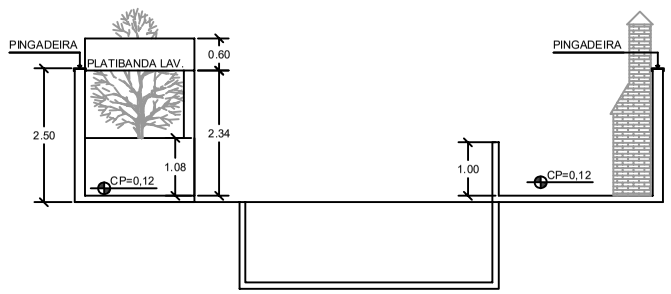

CORTE BB

LEGENDA:

- ⊳X CORTE
- VISTA
- CP= X,XX COTA PISO ACABADO
- CF= X,XX COTA FUNDO PISCINA
- CB= X,XX COTA BORDA PISCINA

CONSTRUTORA E COORDENAÇÃO DE PROJETOS:
BENGENHARIA

LOCAL:
GOIÂNIA

PROJETO:
ARQUITETURA

DESCRIÇÃO:
DESCRIÇÃO: PLANTA BAIXA, CORTES E DETALHE PISC.

REV:	DATA:
00	11-01-25
FOLHA:	ESC:
A2	1:100